


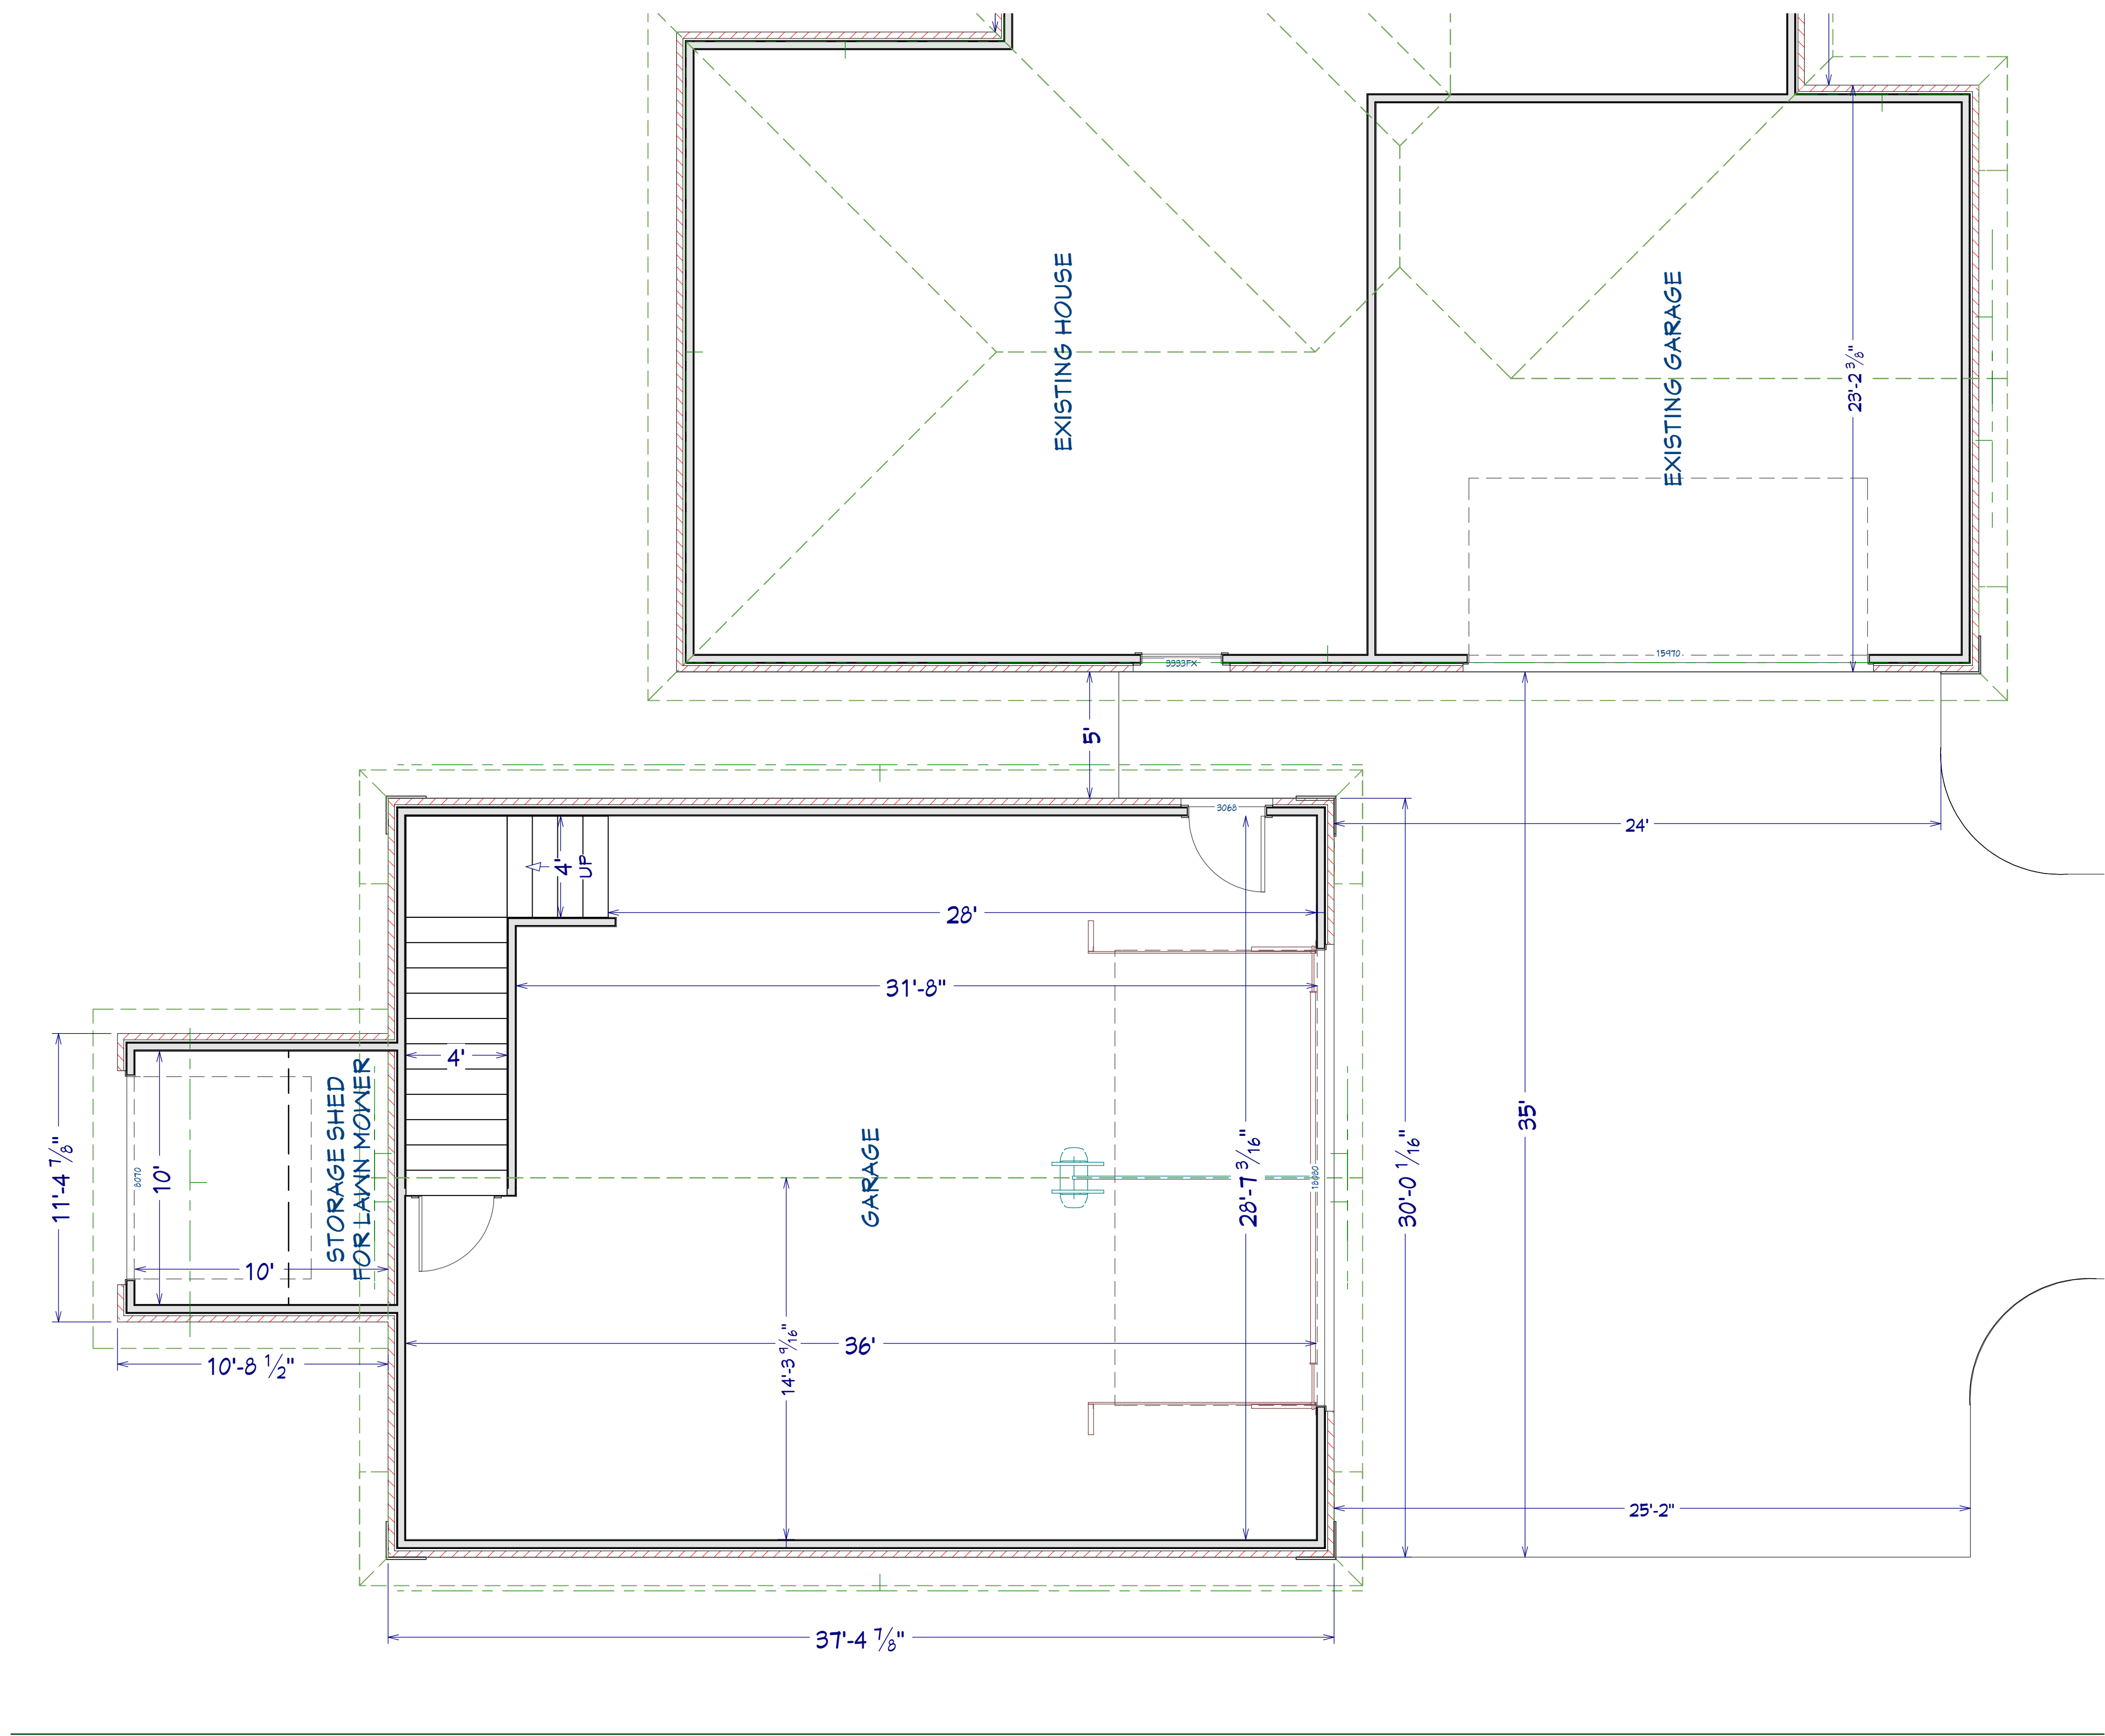


227 MARENGO DR.
RICHMOND, KY 40475

DEBOARD RESIDENCE

PROPOSED 1ST FLOOR PLAN

DATE
JUNE 12,
2025

SHEET #
A01

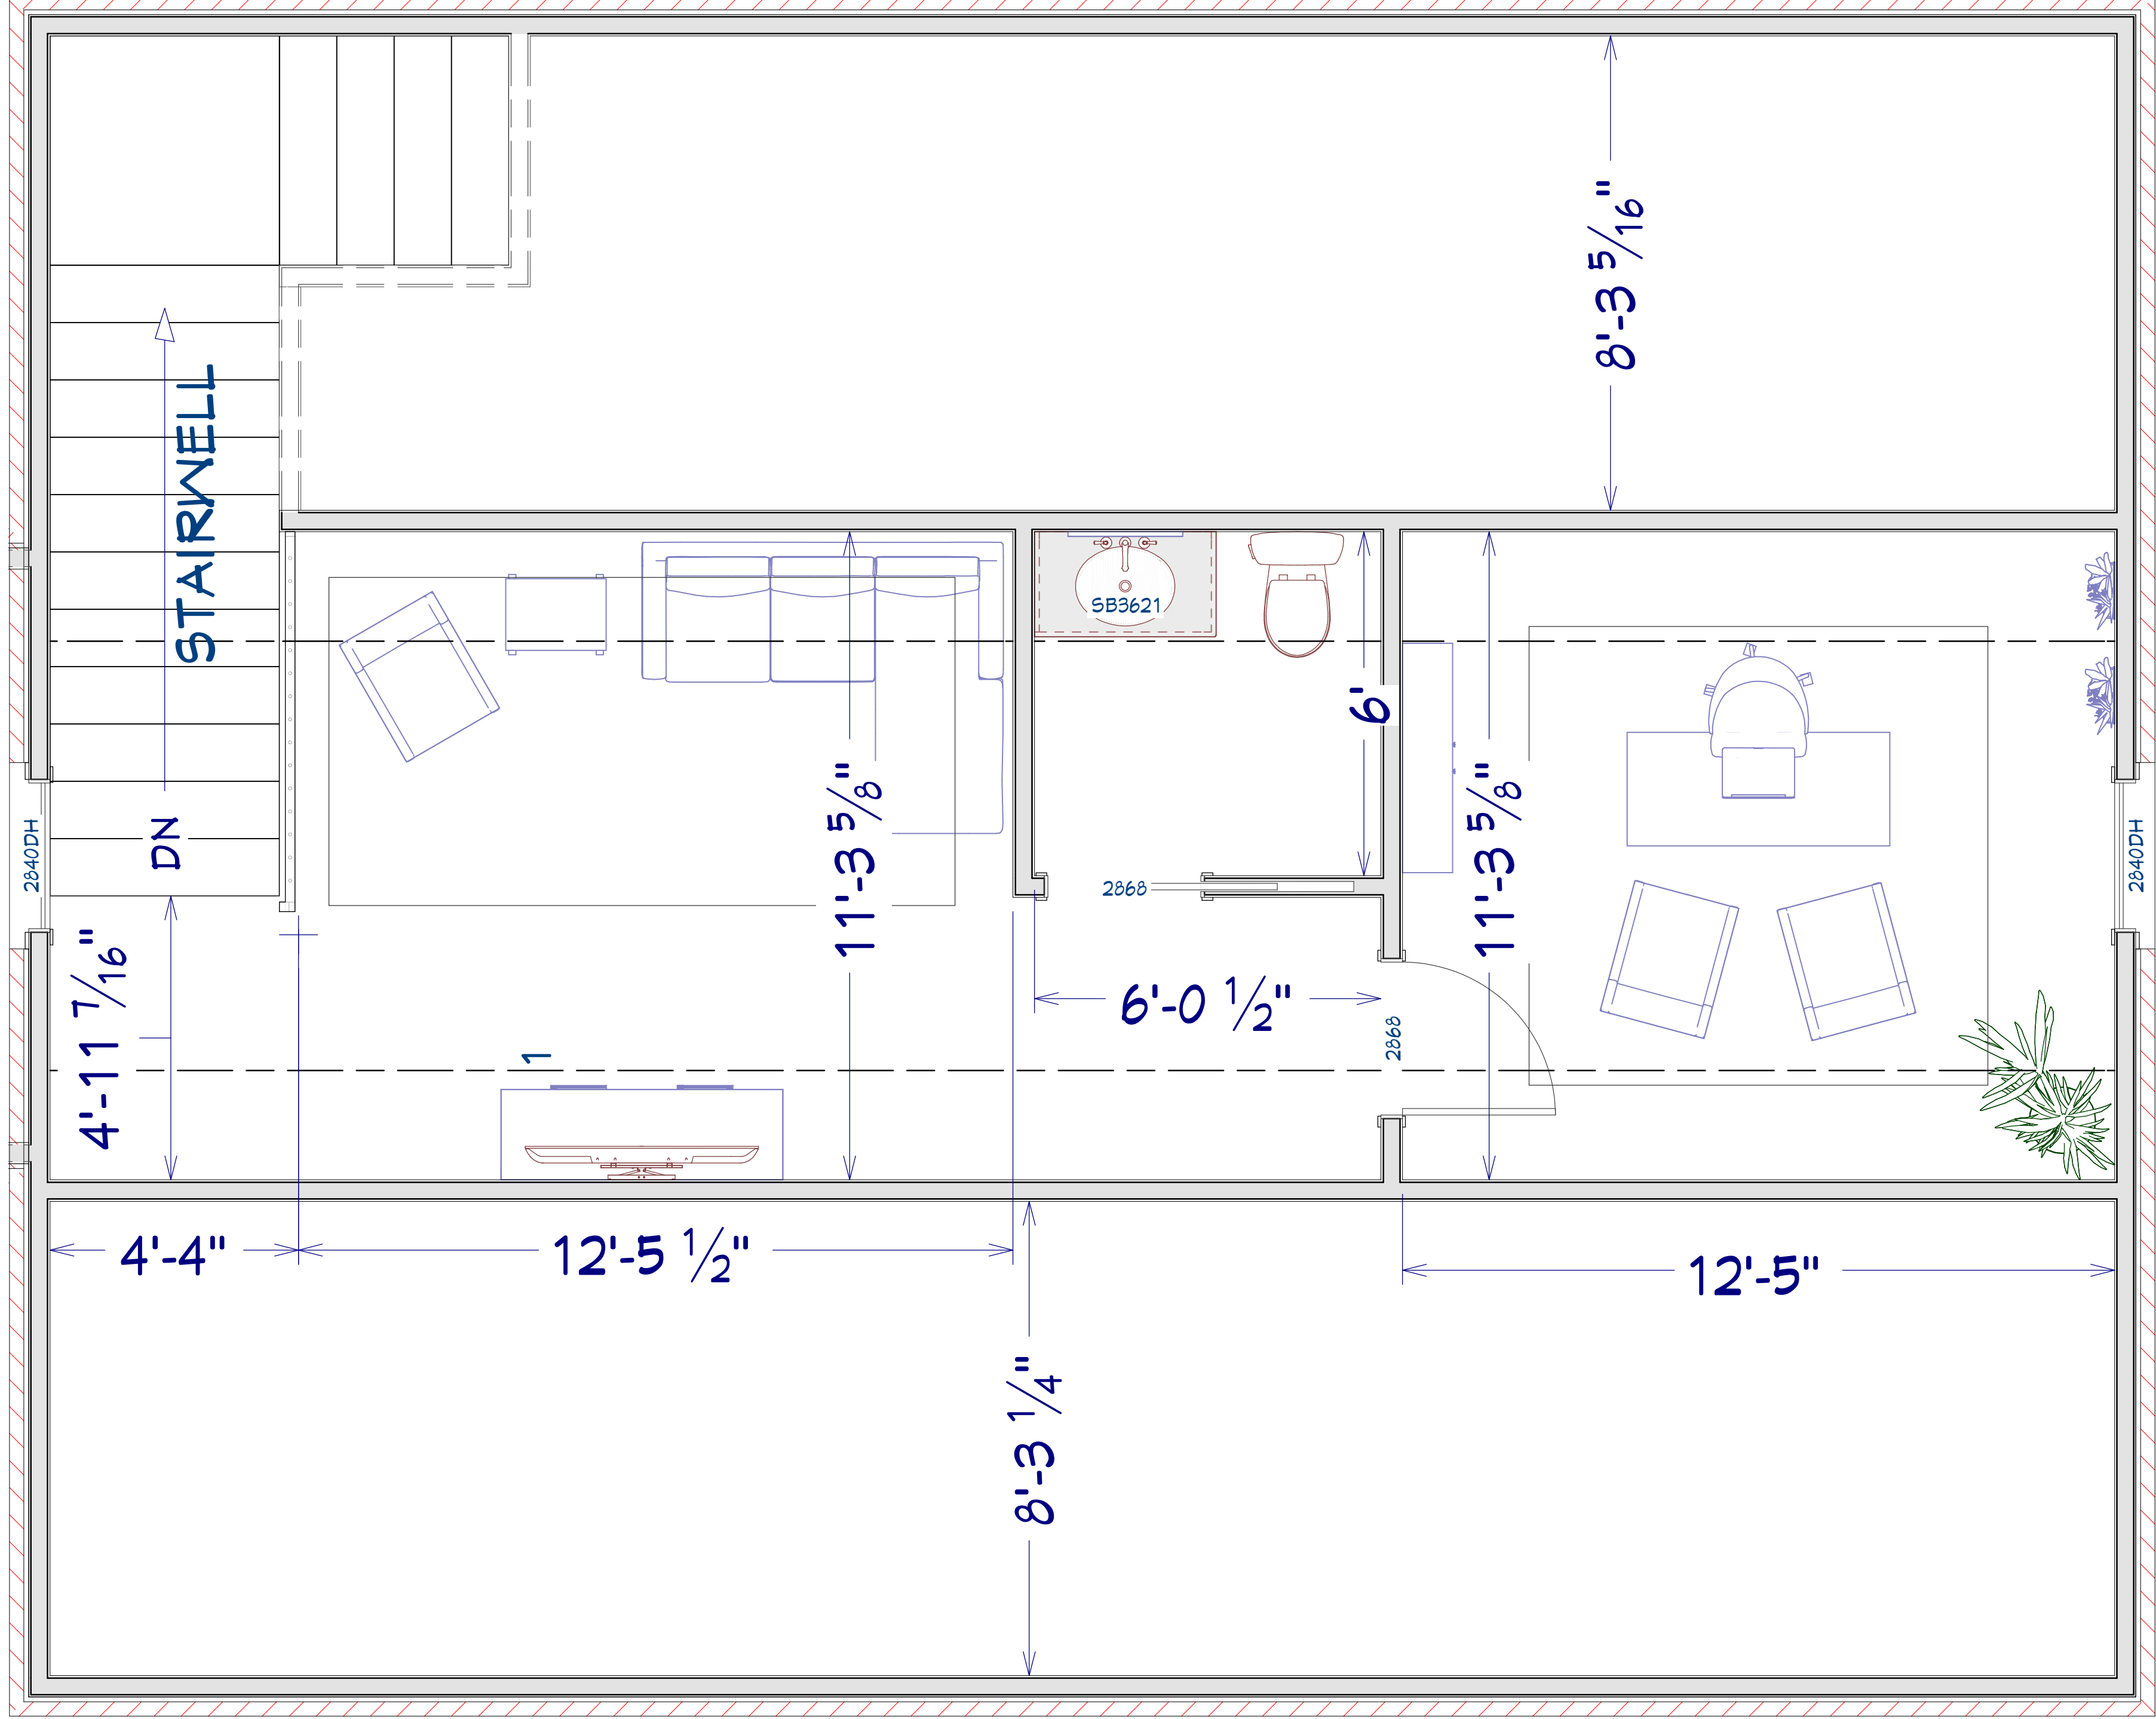


227 MARENGO DR.
RICHMOND, KY 40475


DEBOARD RESIDENCE

PROPOSED
ATTIC PLAN

DATE
JUNE 12,
2025

SHEET #
A02

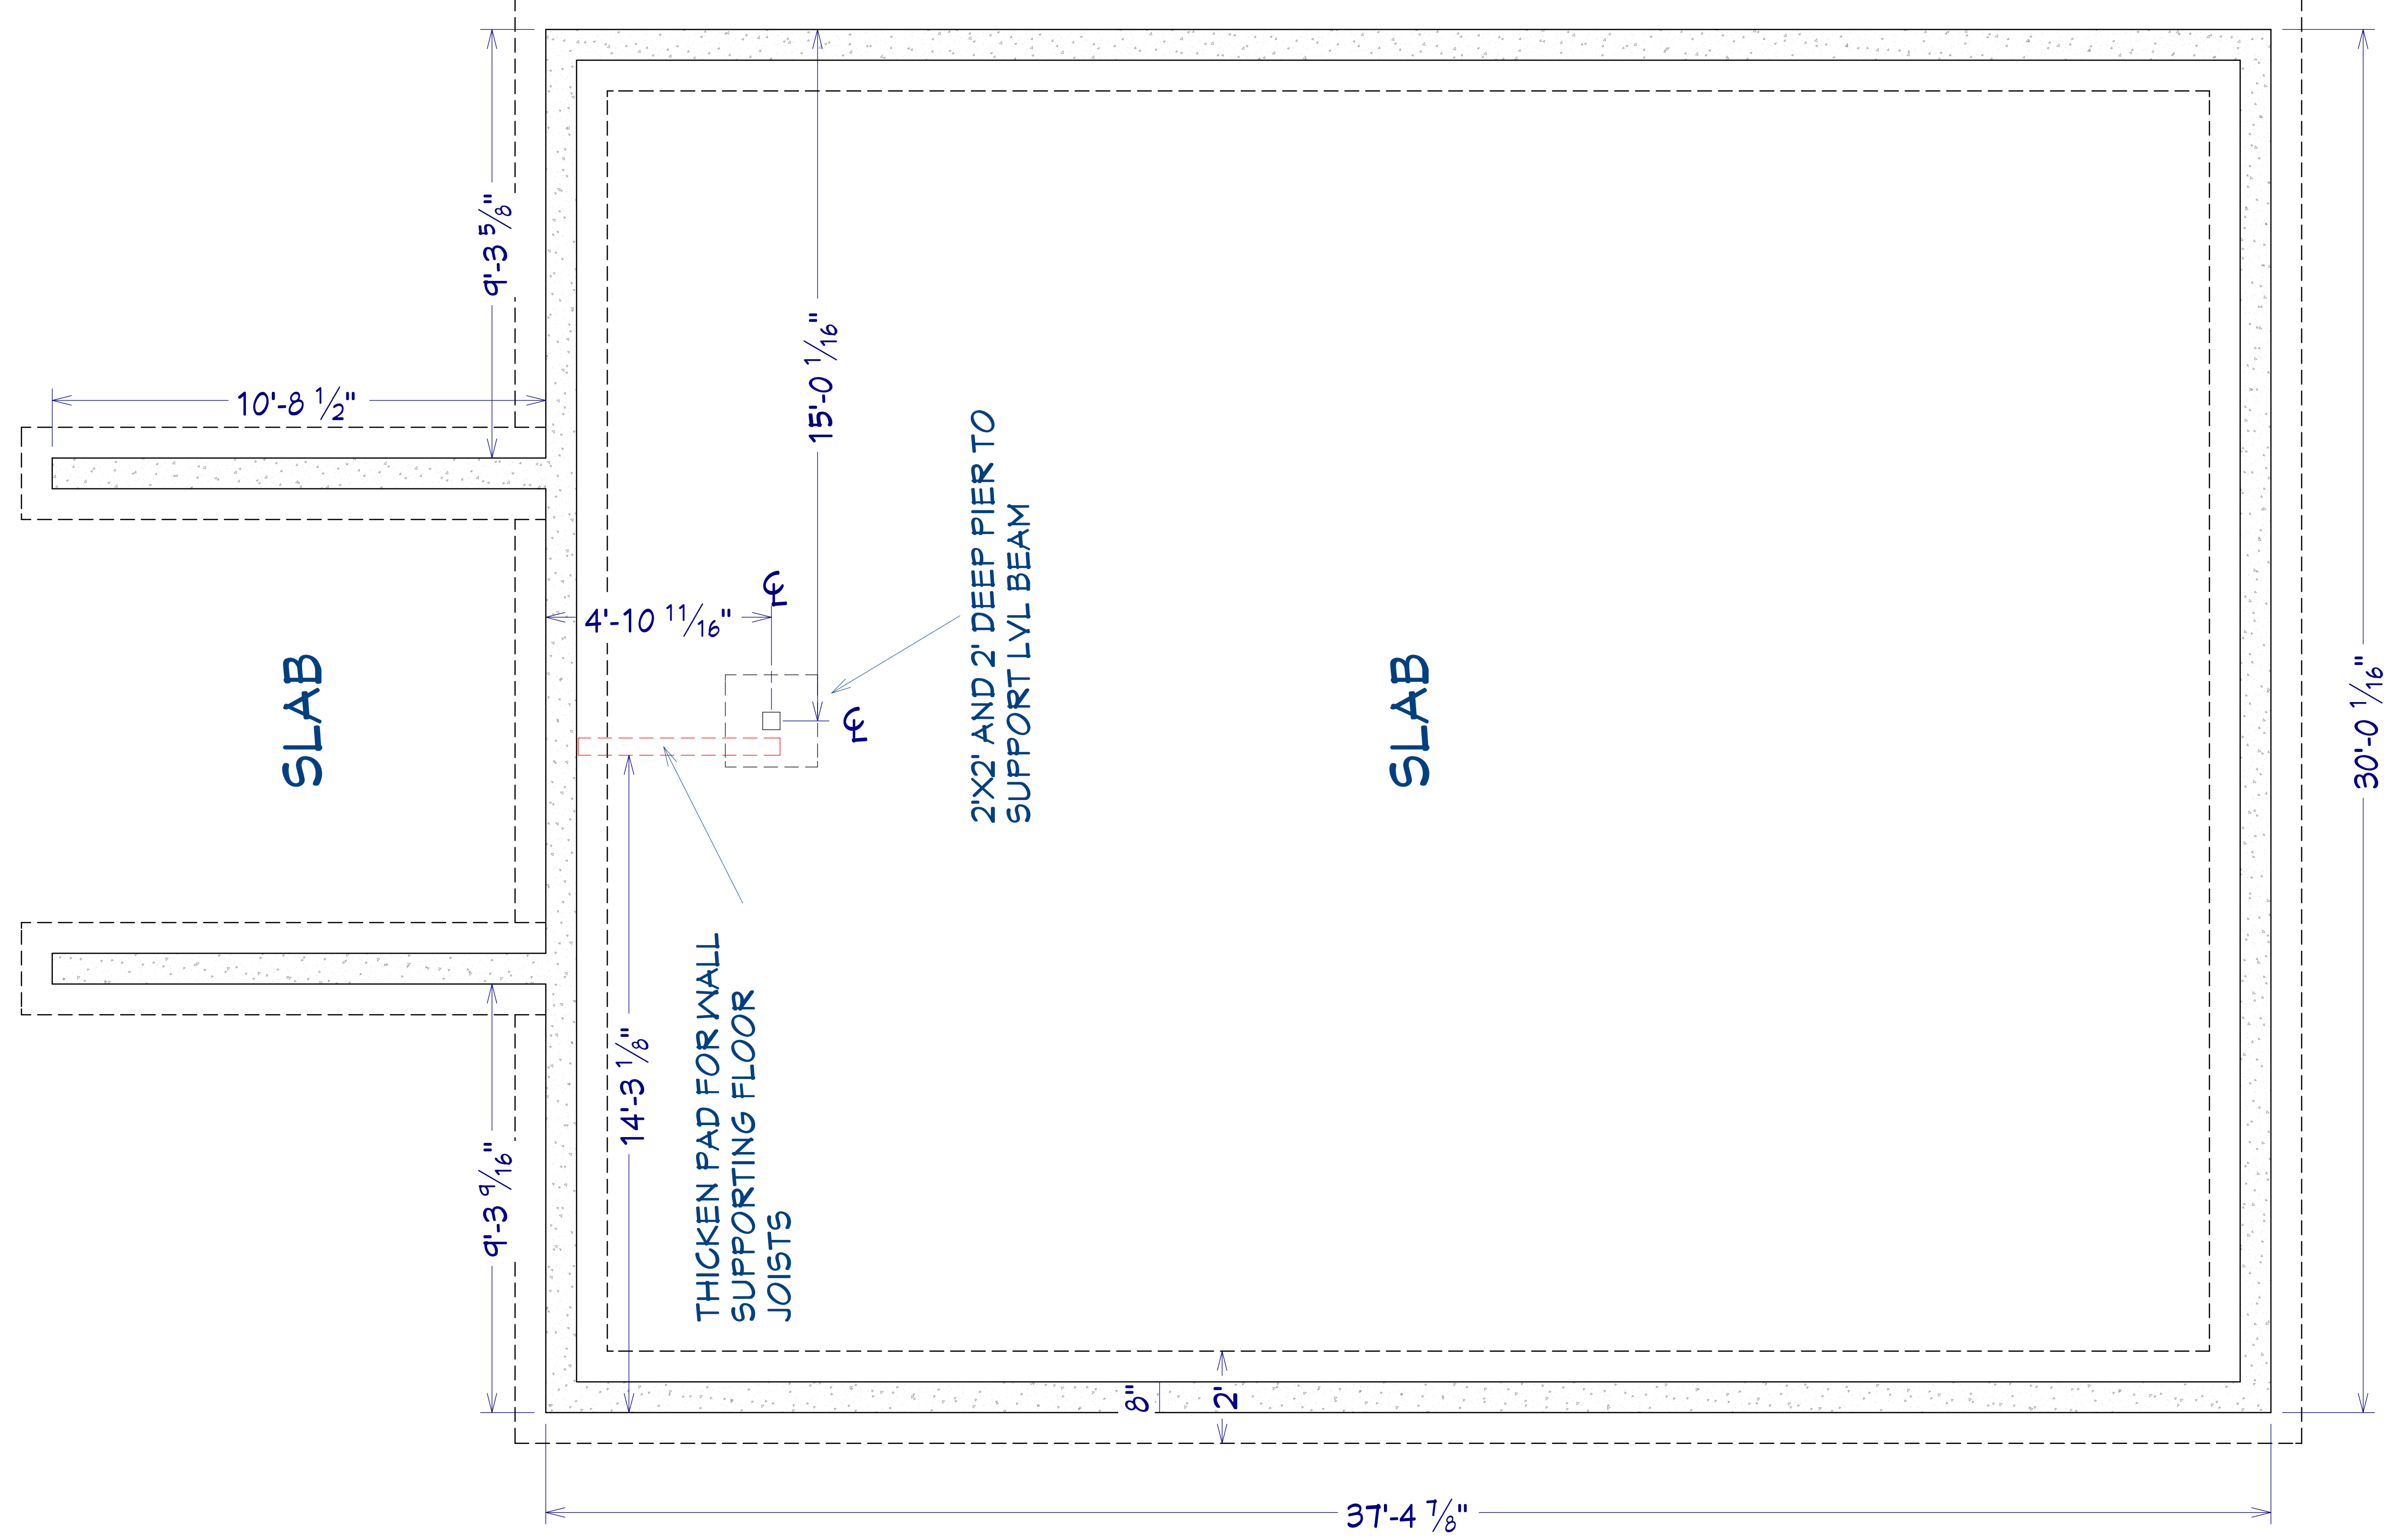

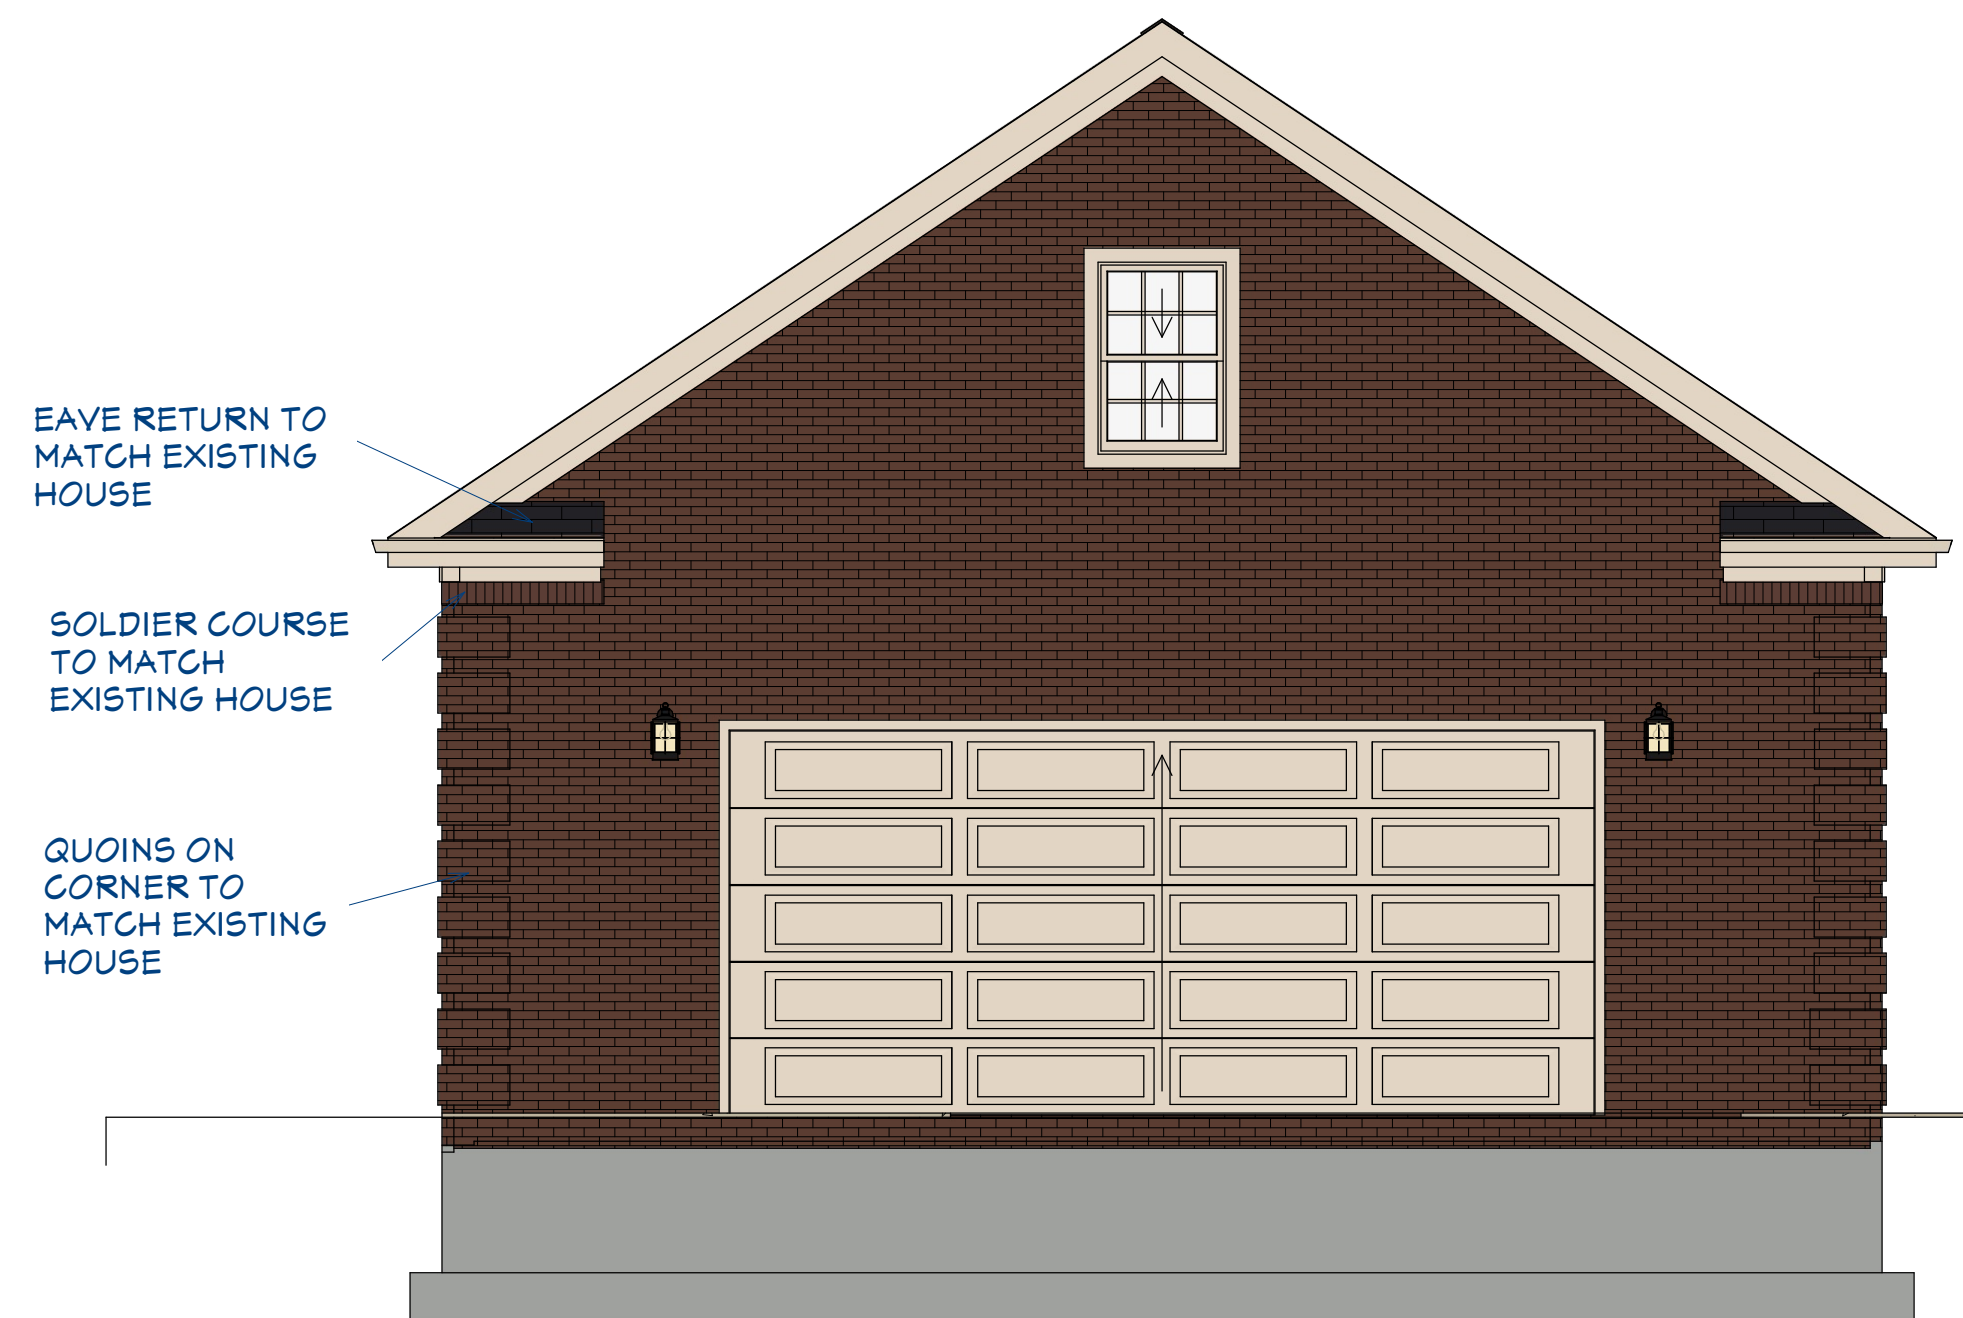

FRONT



RIGHT SIDE



ADJUST SHED HEIGHT AS
NEEDED FOR DROP IN GRADE

BACK



LEFT SIDE

SHEET #

A04

DATE


JUNE 12,
2025


ELEVATIONS

227 MARENGO DR.
RICHMOND, KY 40475

DEBOARD RESIDENCE


J&R Construction
DESIGN - BUILD - REMODEL

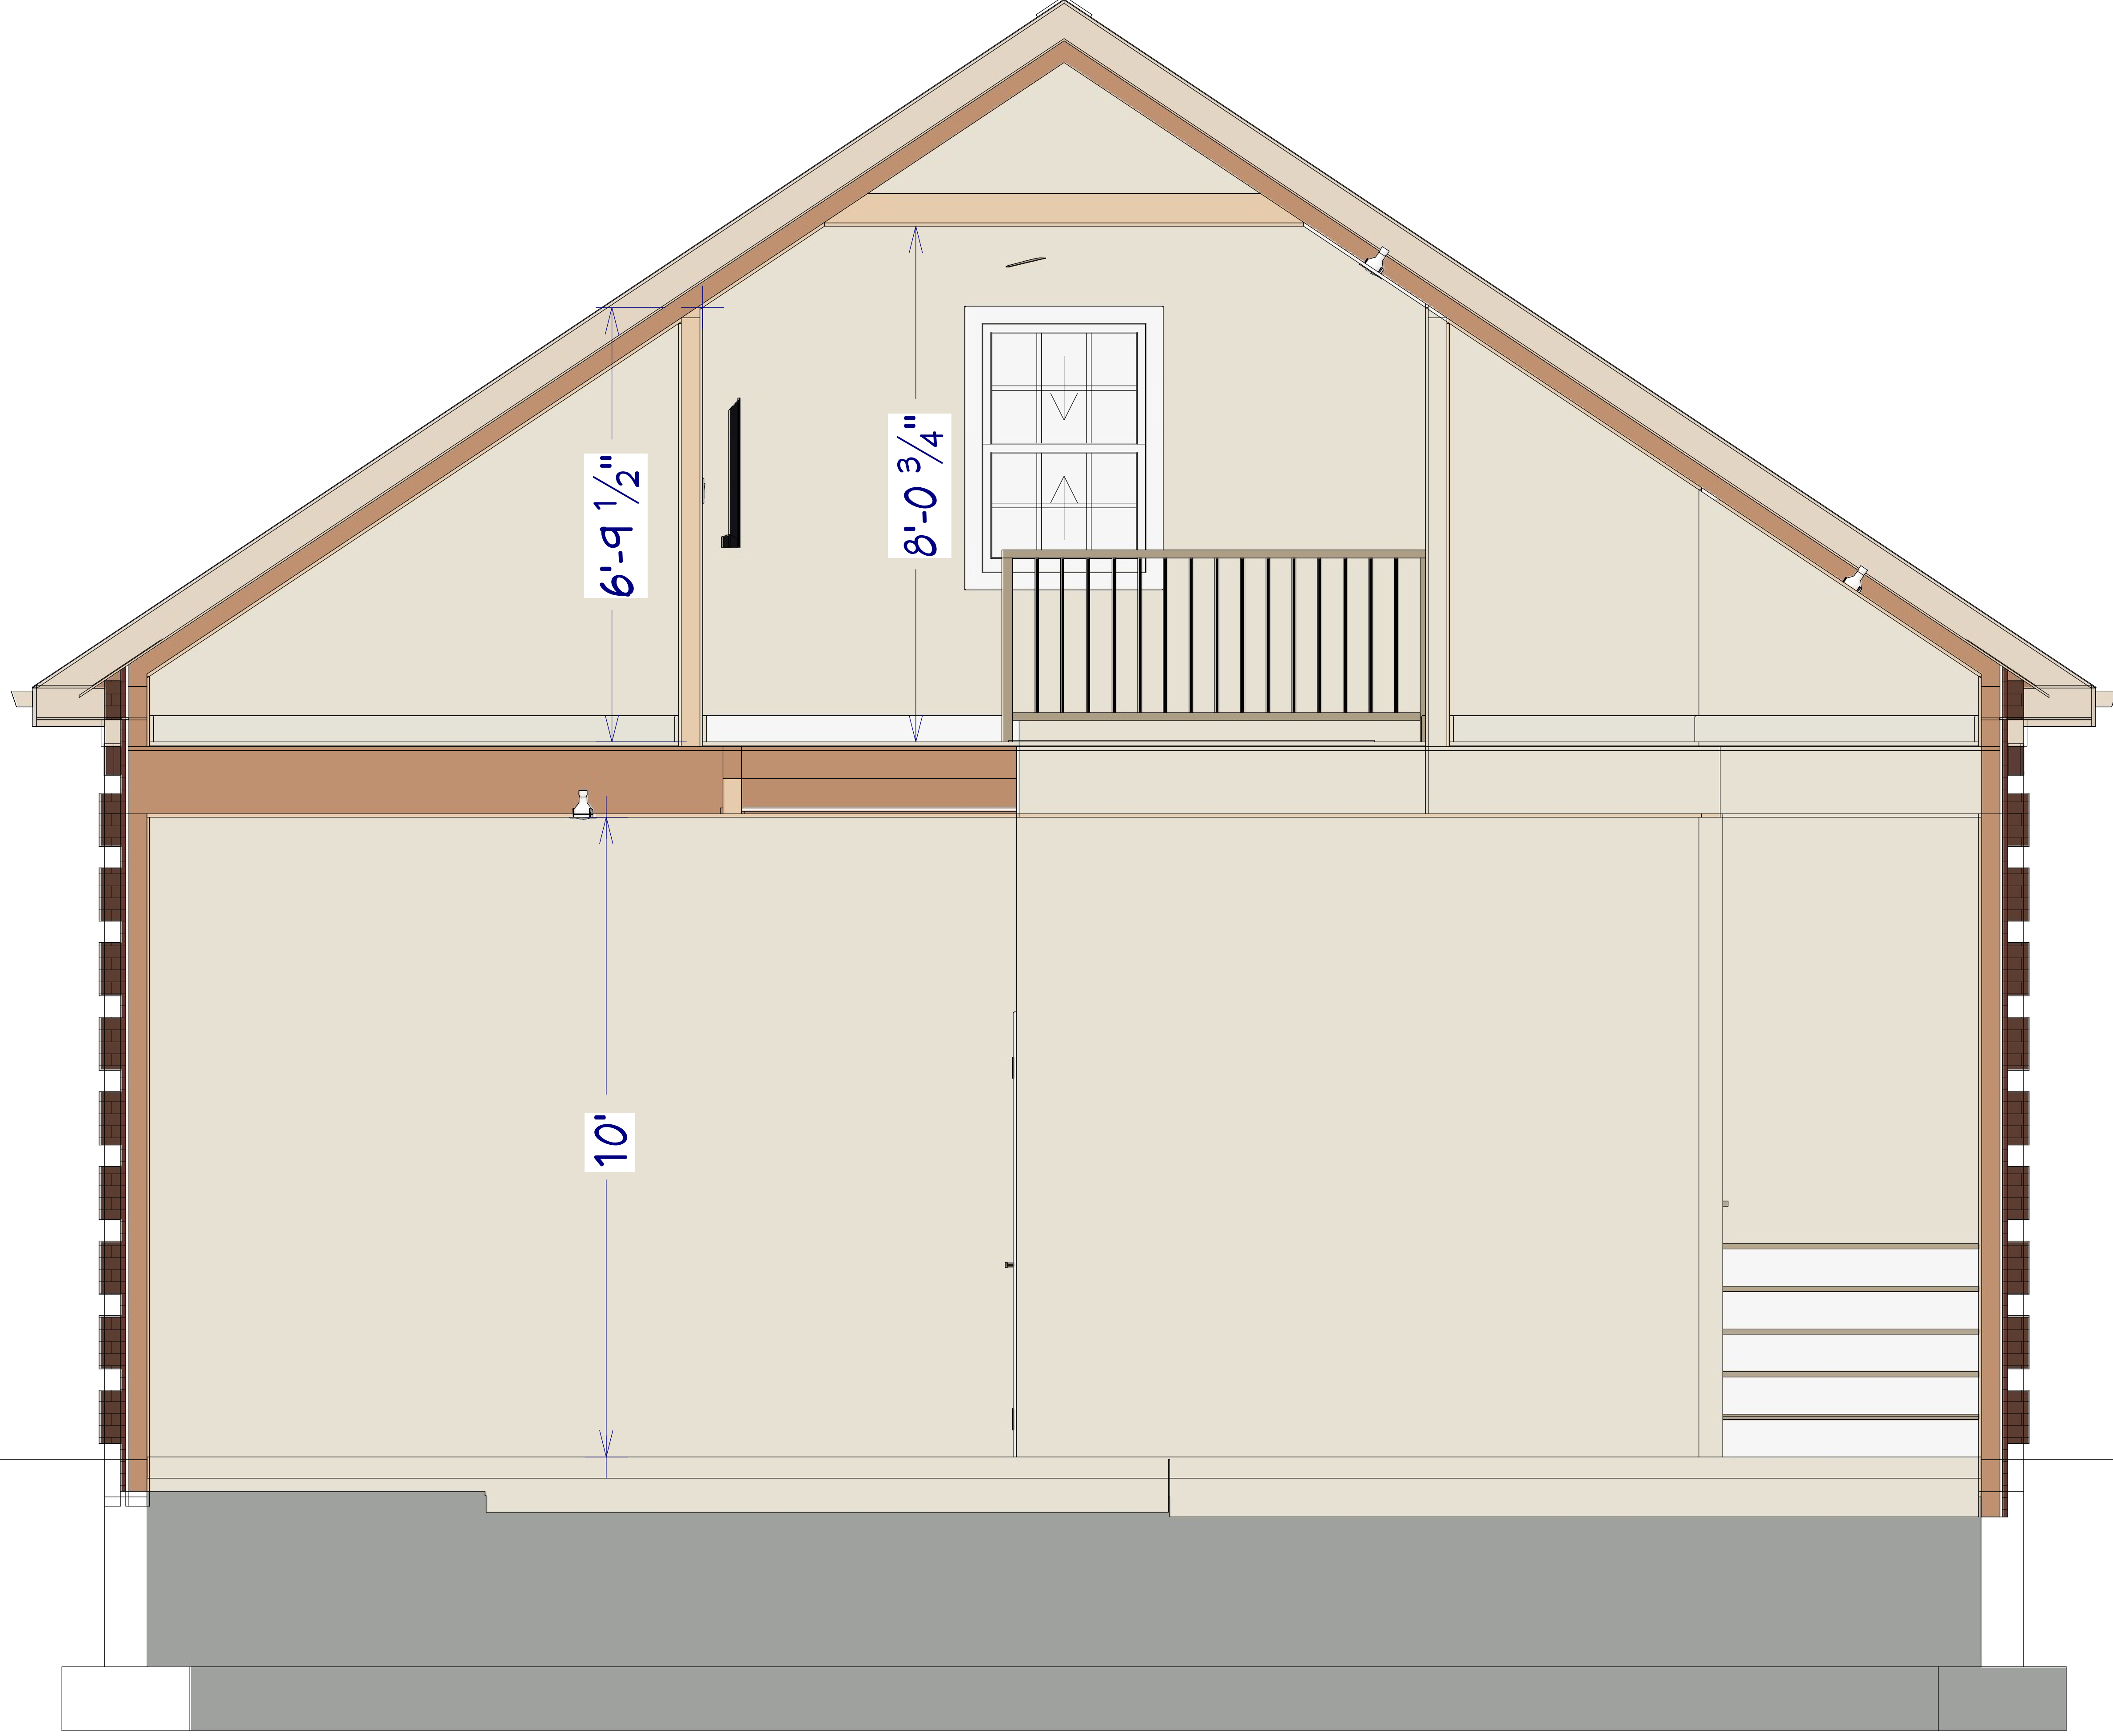

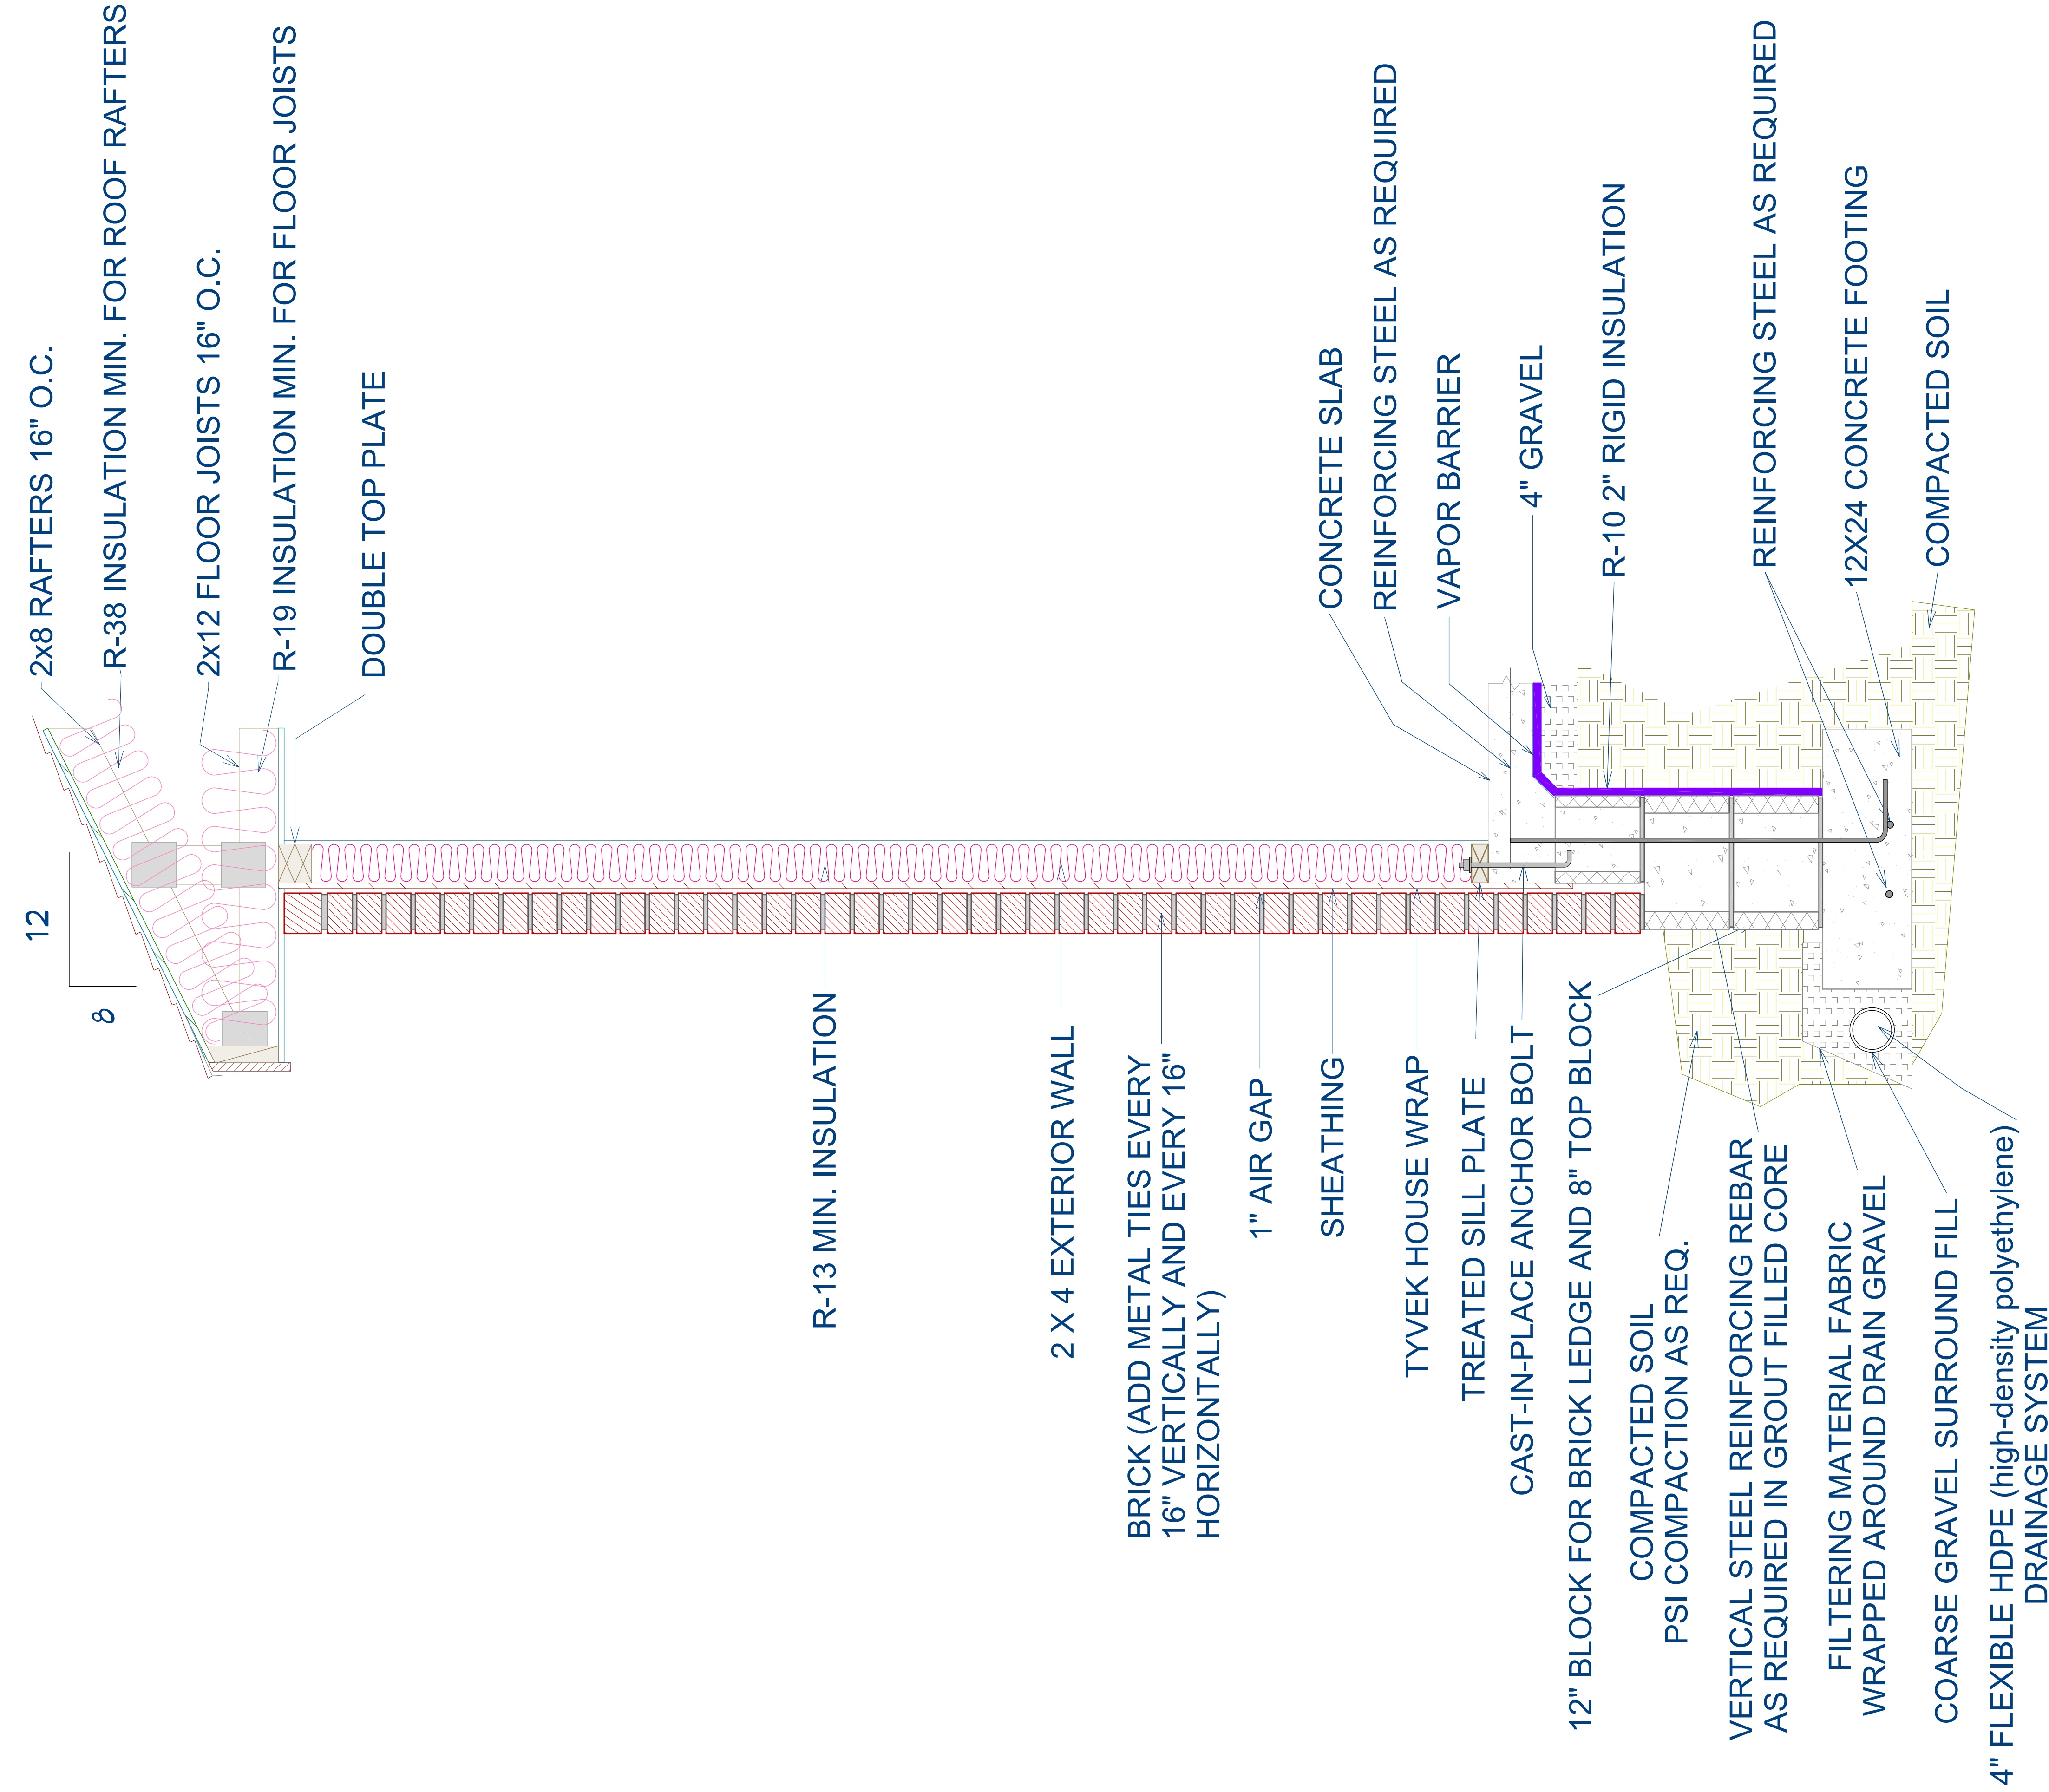

FIELD VERIFY BLOCK HEIGHT

NOTE: SLOPE GROUND AWAY FROM HOUSE AT MINIMUM 5% SLOPE FOR 10'. IF PHYSICAL OBSTRUCTIONS PREVENT 10' DISTANCE, AN ALTERNATIVE METHOD FOR DIVERTING WATER AWAY MUST BE USED

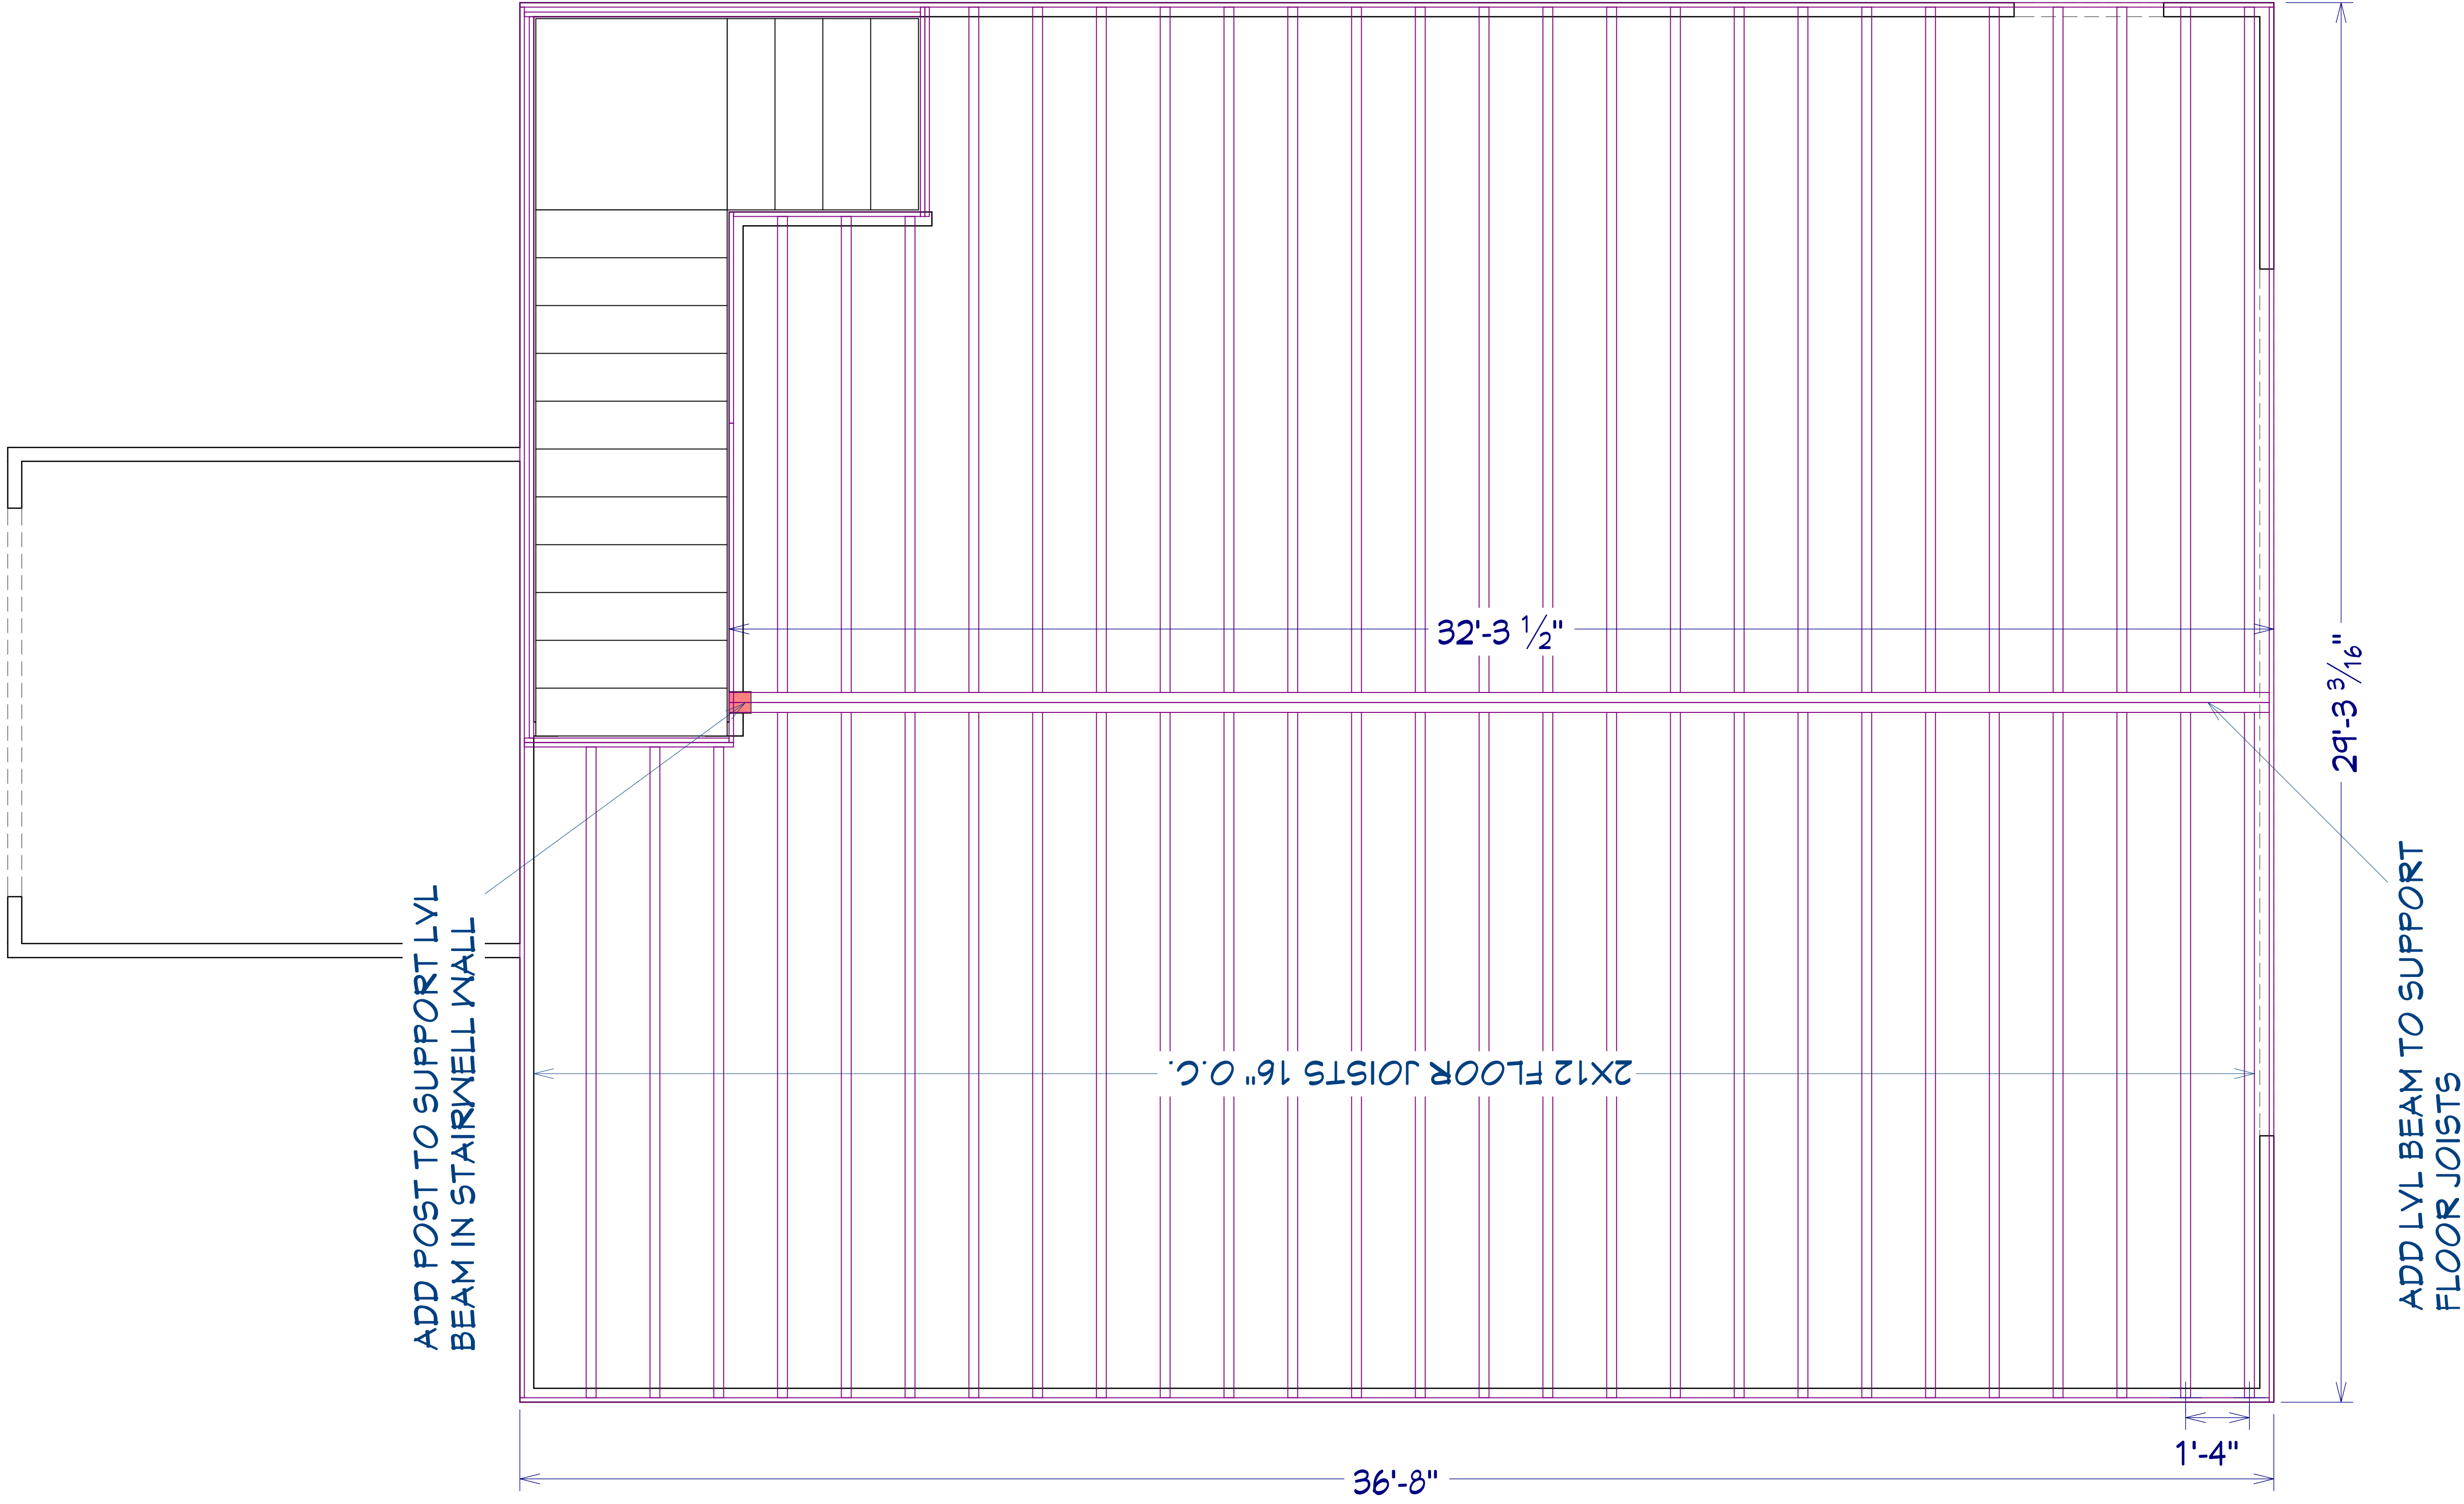


227 MARENGO DR.
RICHMOND, KY 40475

DEBOARD RESIDENCE

ATTIC
FLOOR
FRAMING

DATE
JUNE 12,
2025

SHEET #
A07

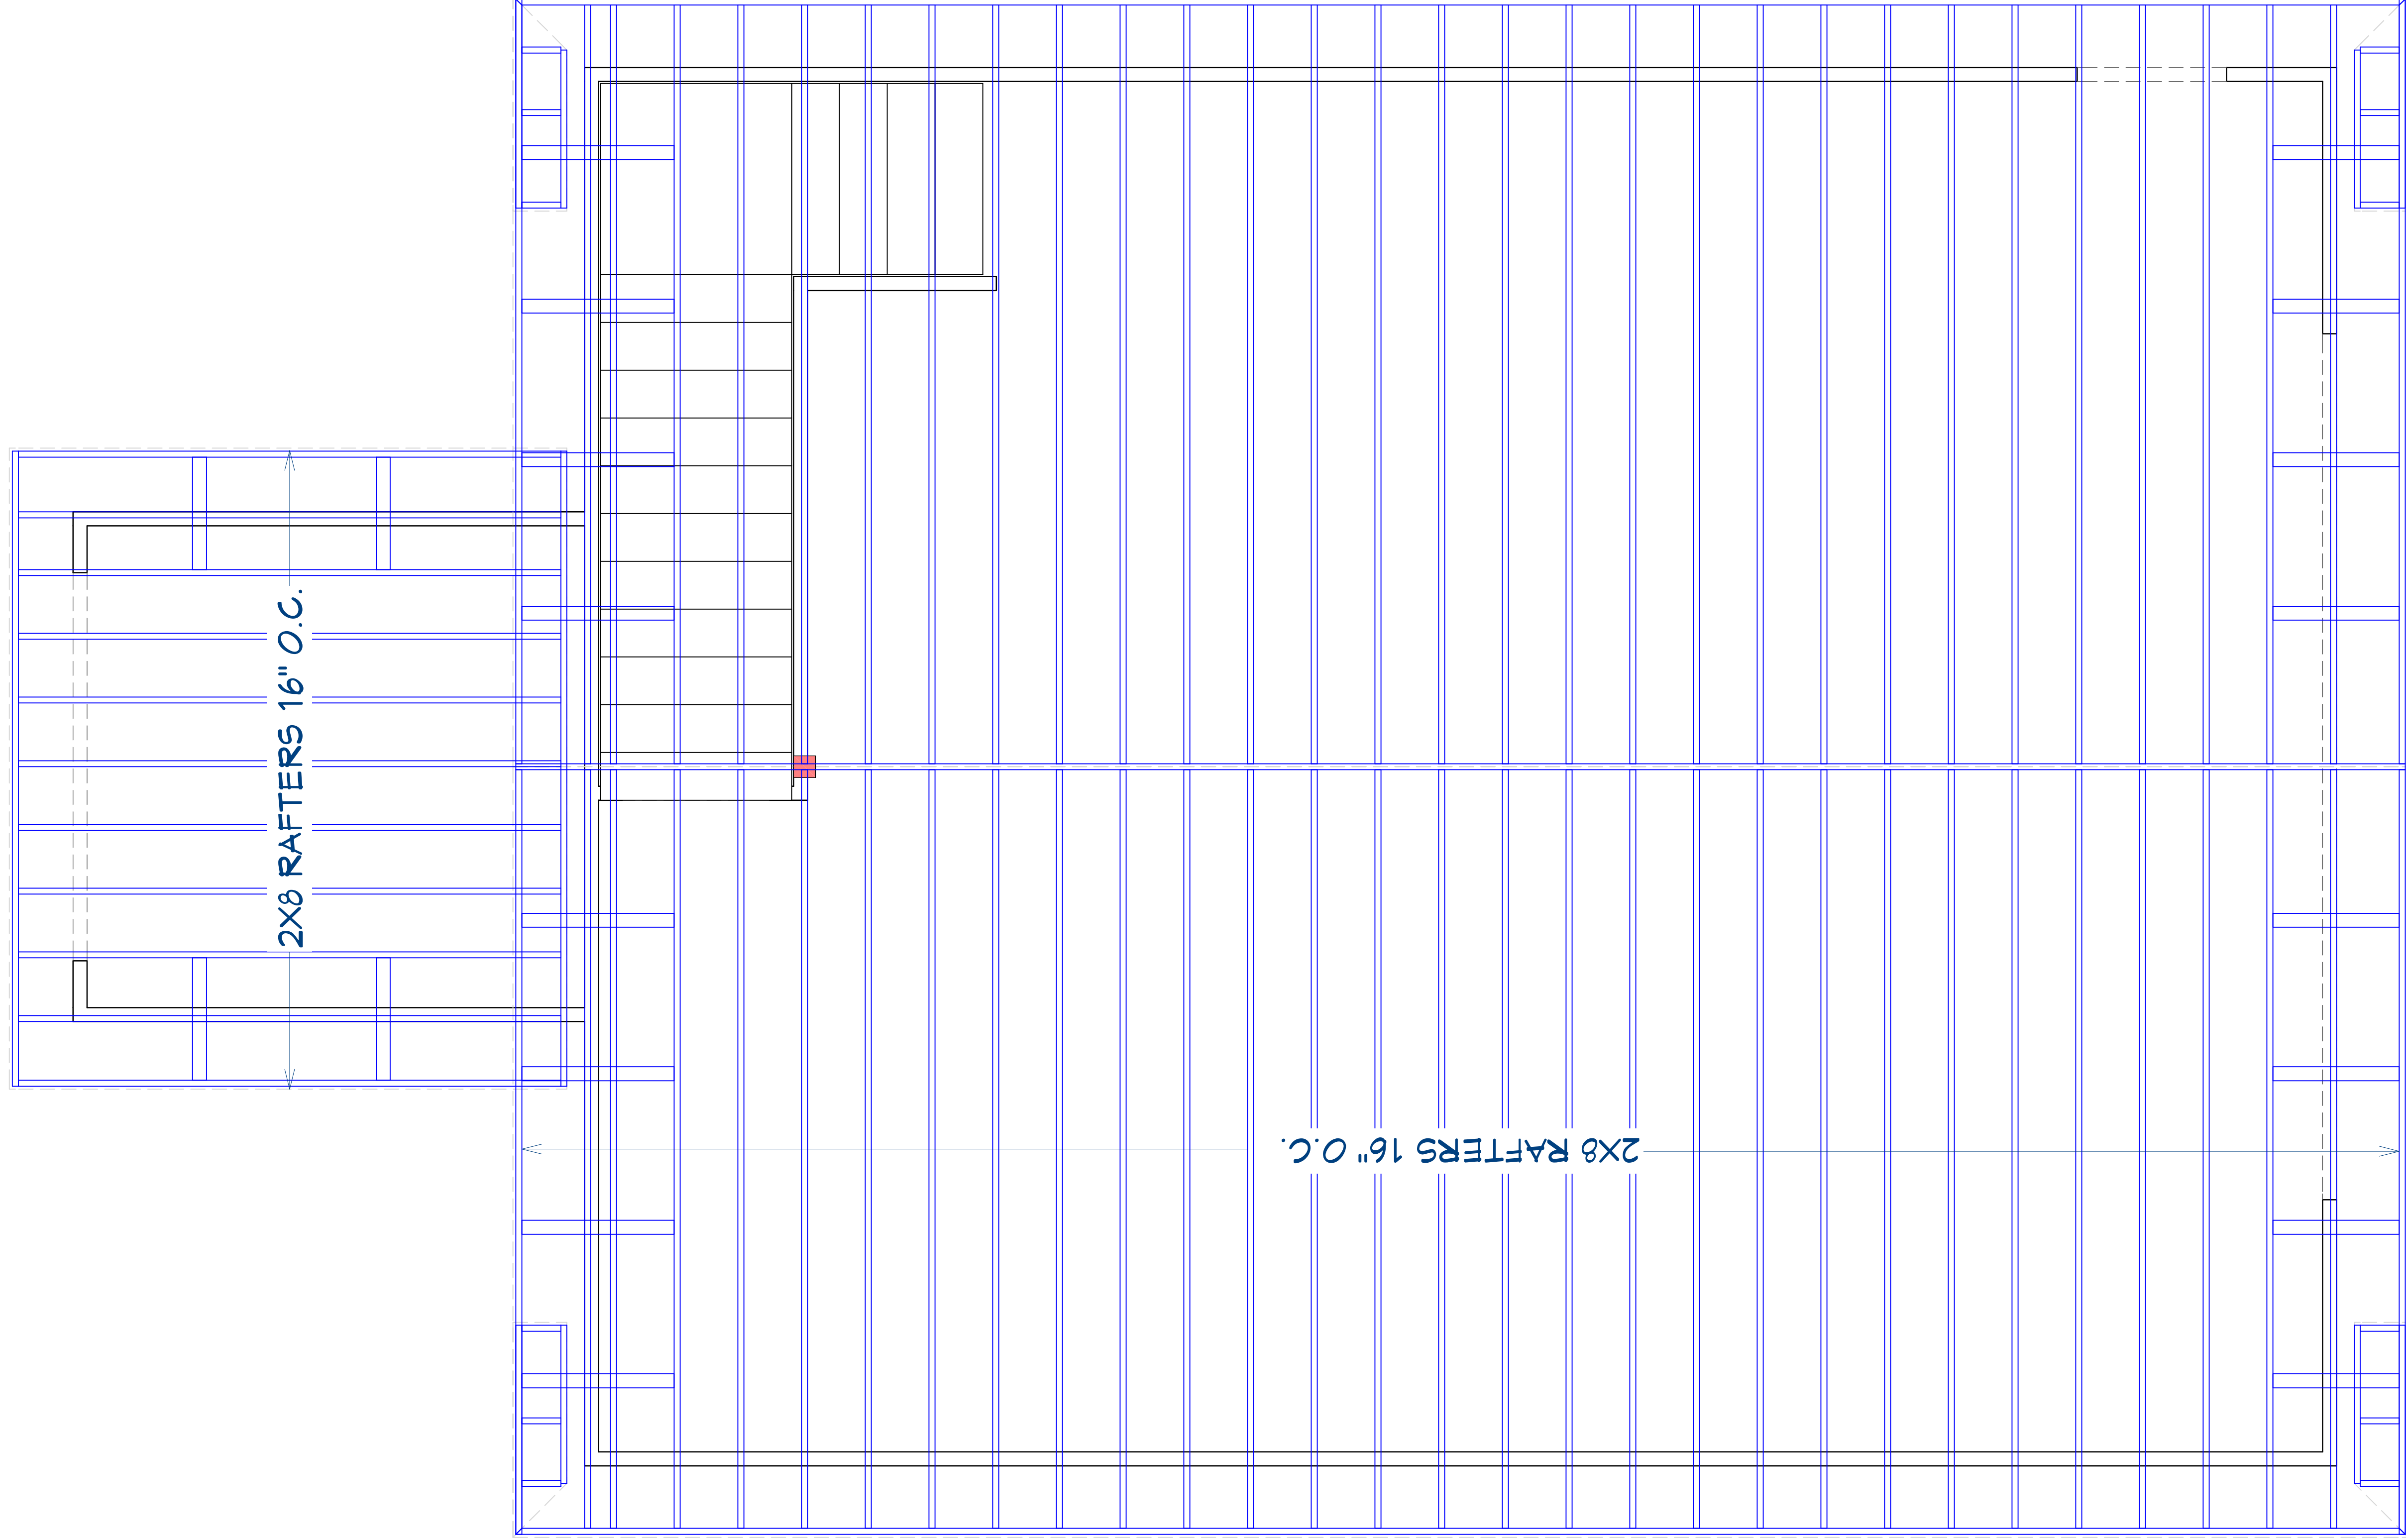

227 MARENGO DR.
RICHMOND, KY 40475

DEBOARD RESIDENCE

ROOF FRAMING PLAN


DATE

JUNE 12,
2025

SHEET #

A08

ADD OUTLETS PER CODE
OPTION FOR ELECTRIC CAR CHARGER

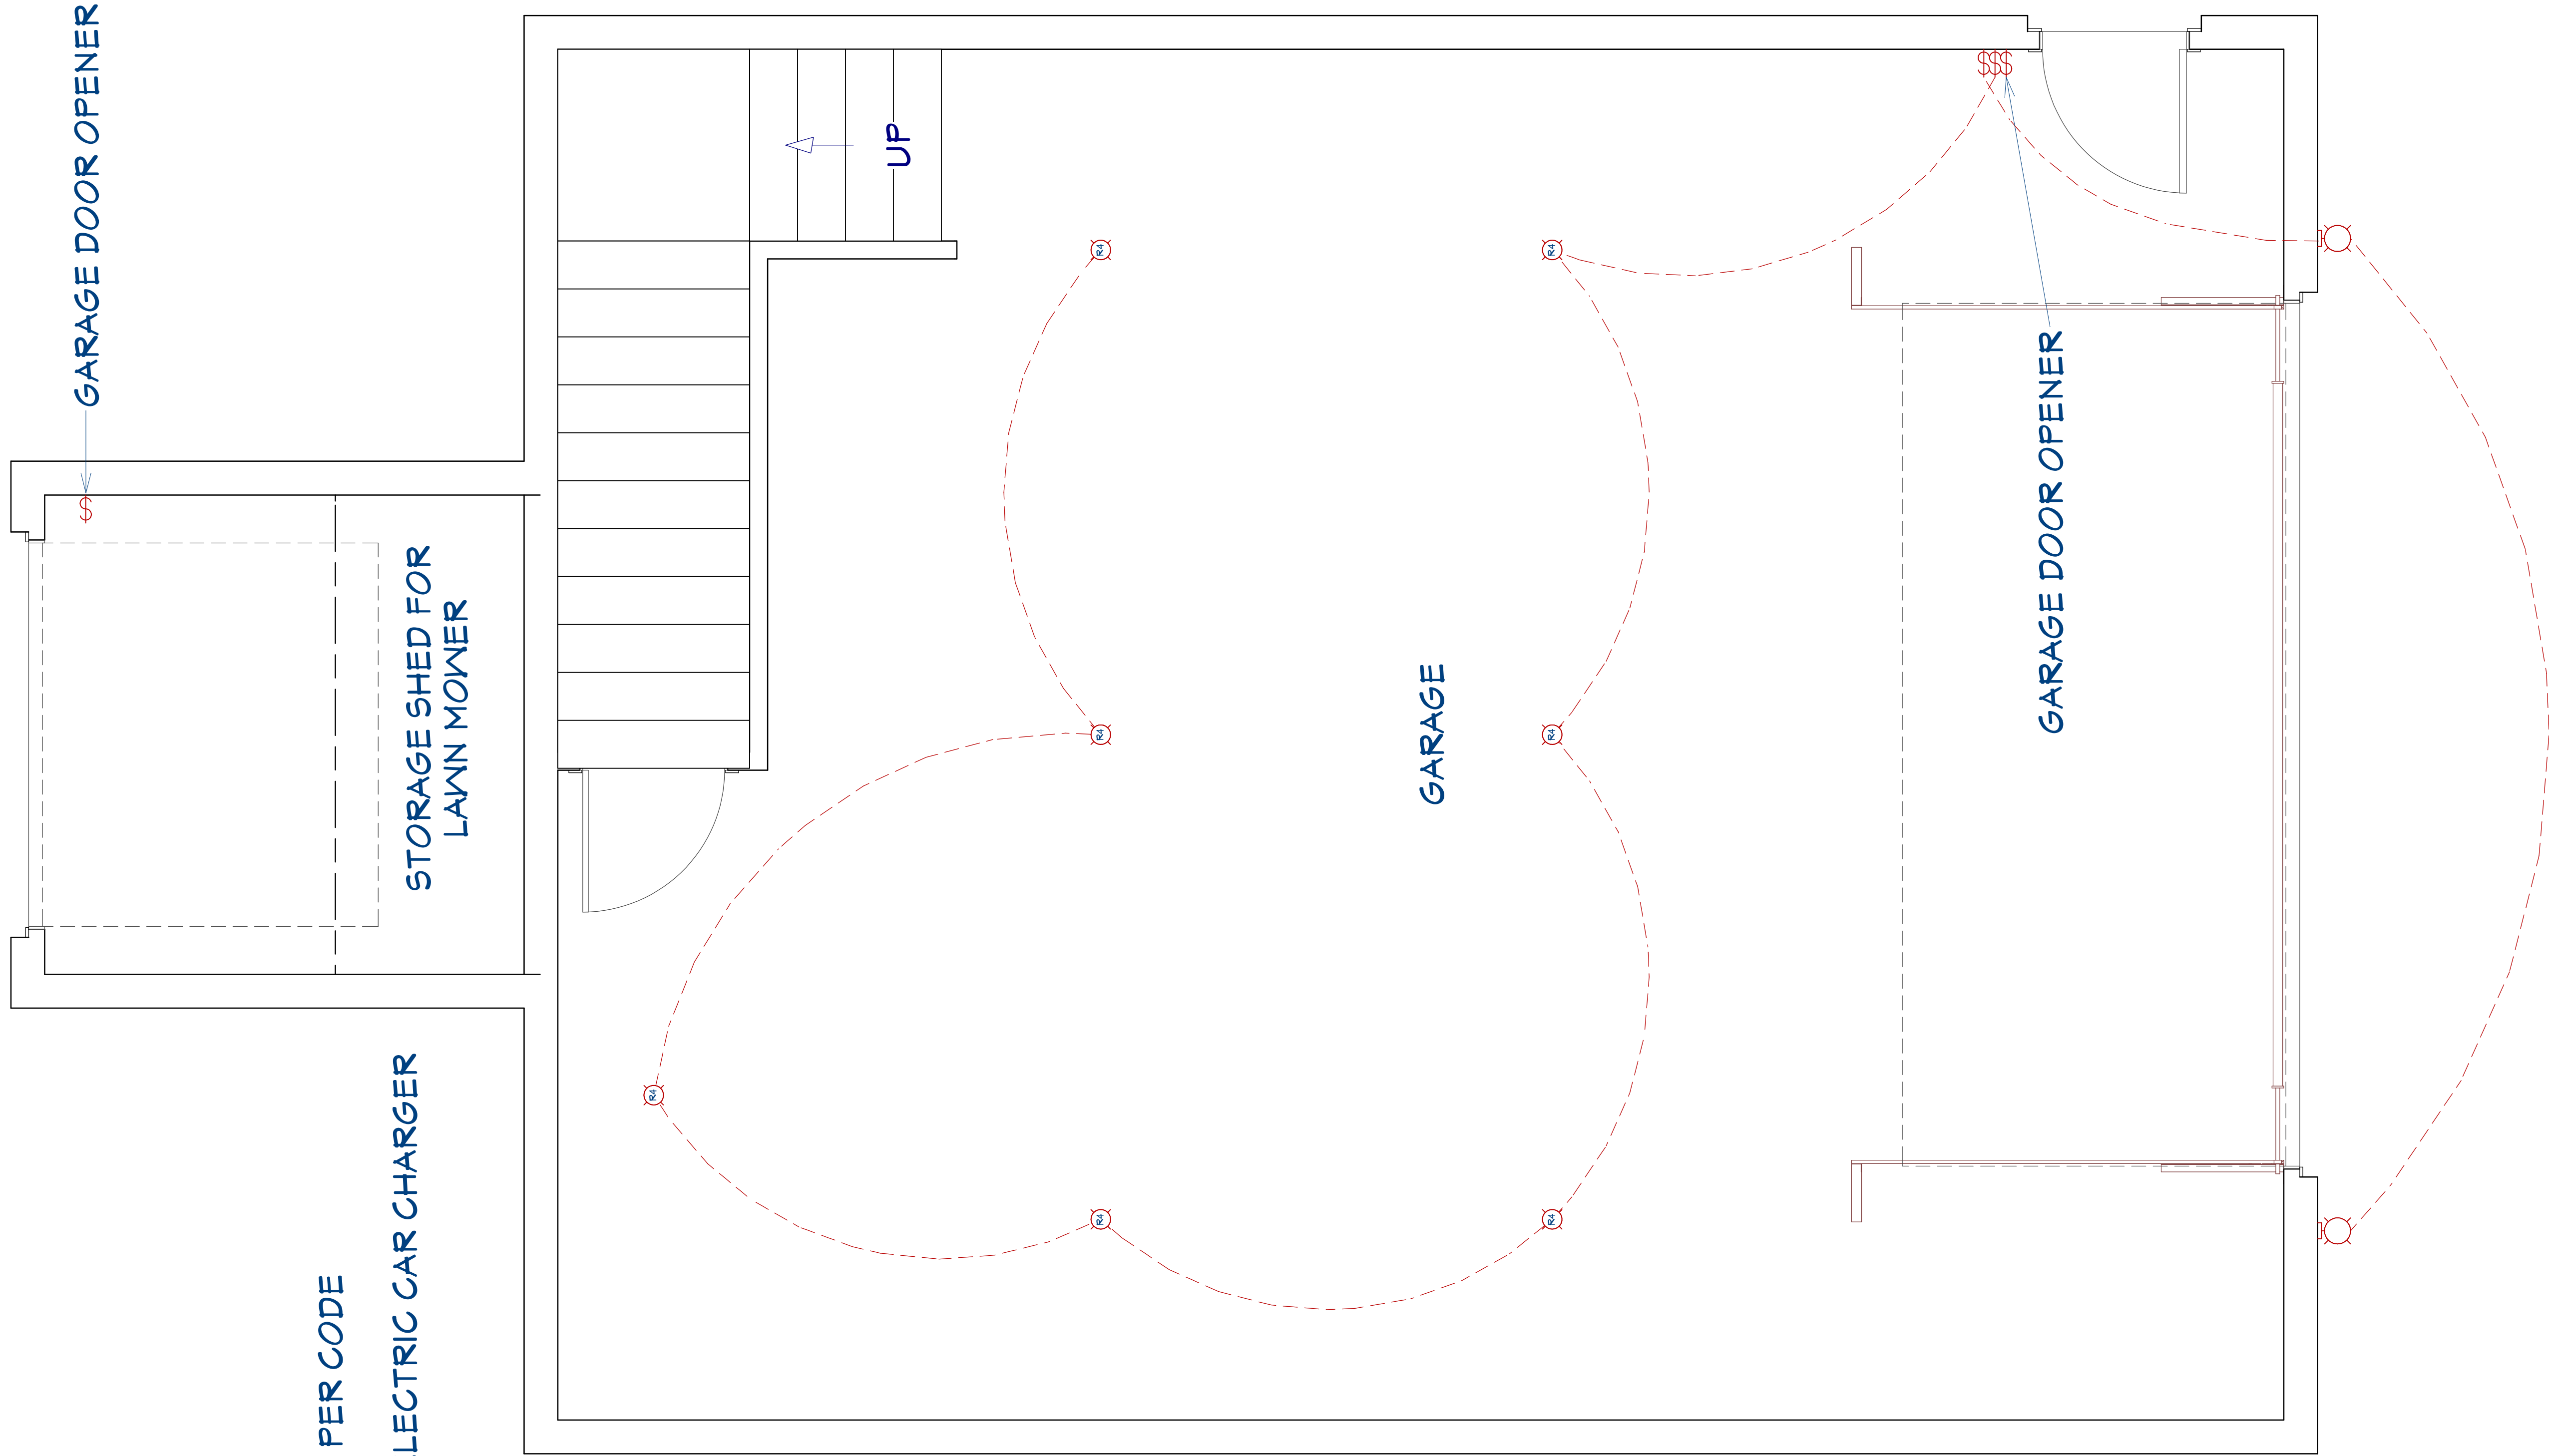

227 MARENGO DR.
RICHMOND, KY 40475

DEBOARD RESIDENCE

ELECTRIC PLAN (GARAGE)


DATE

JUNE 12,
2025

SHEET #

A09

[]

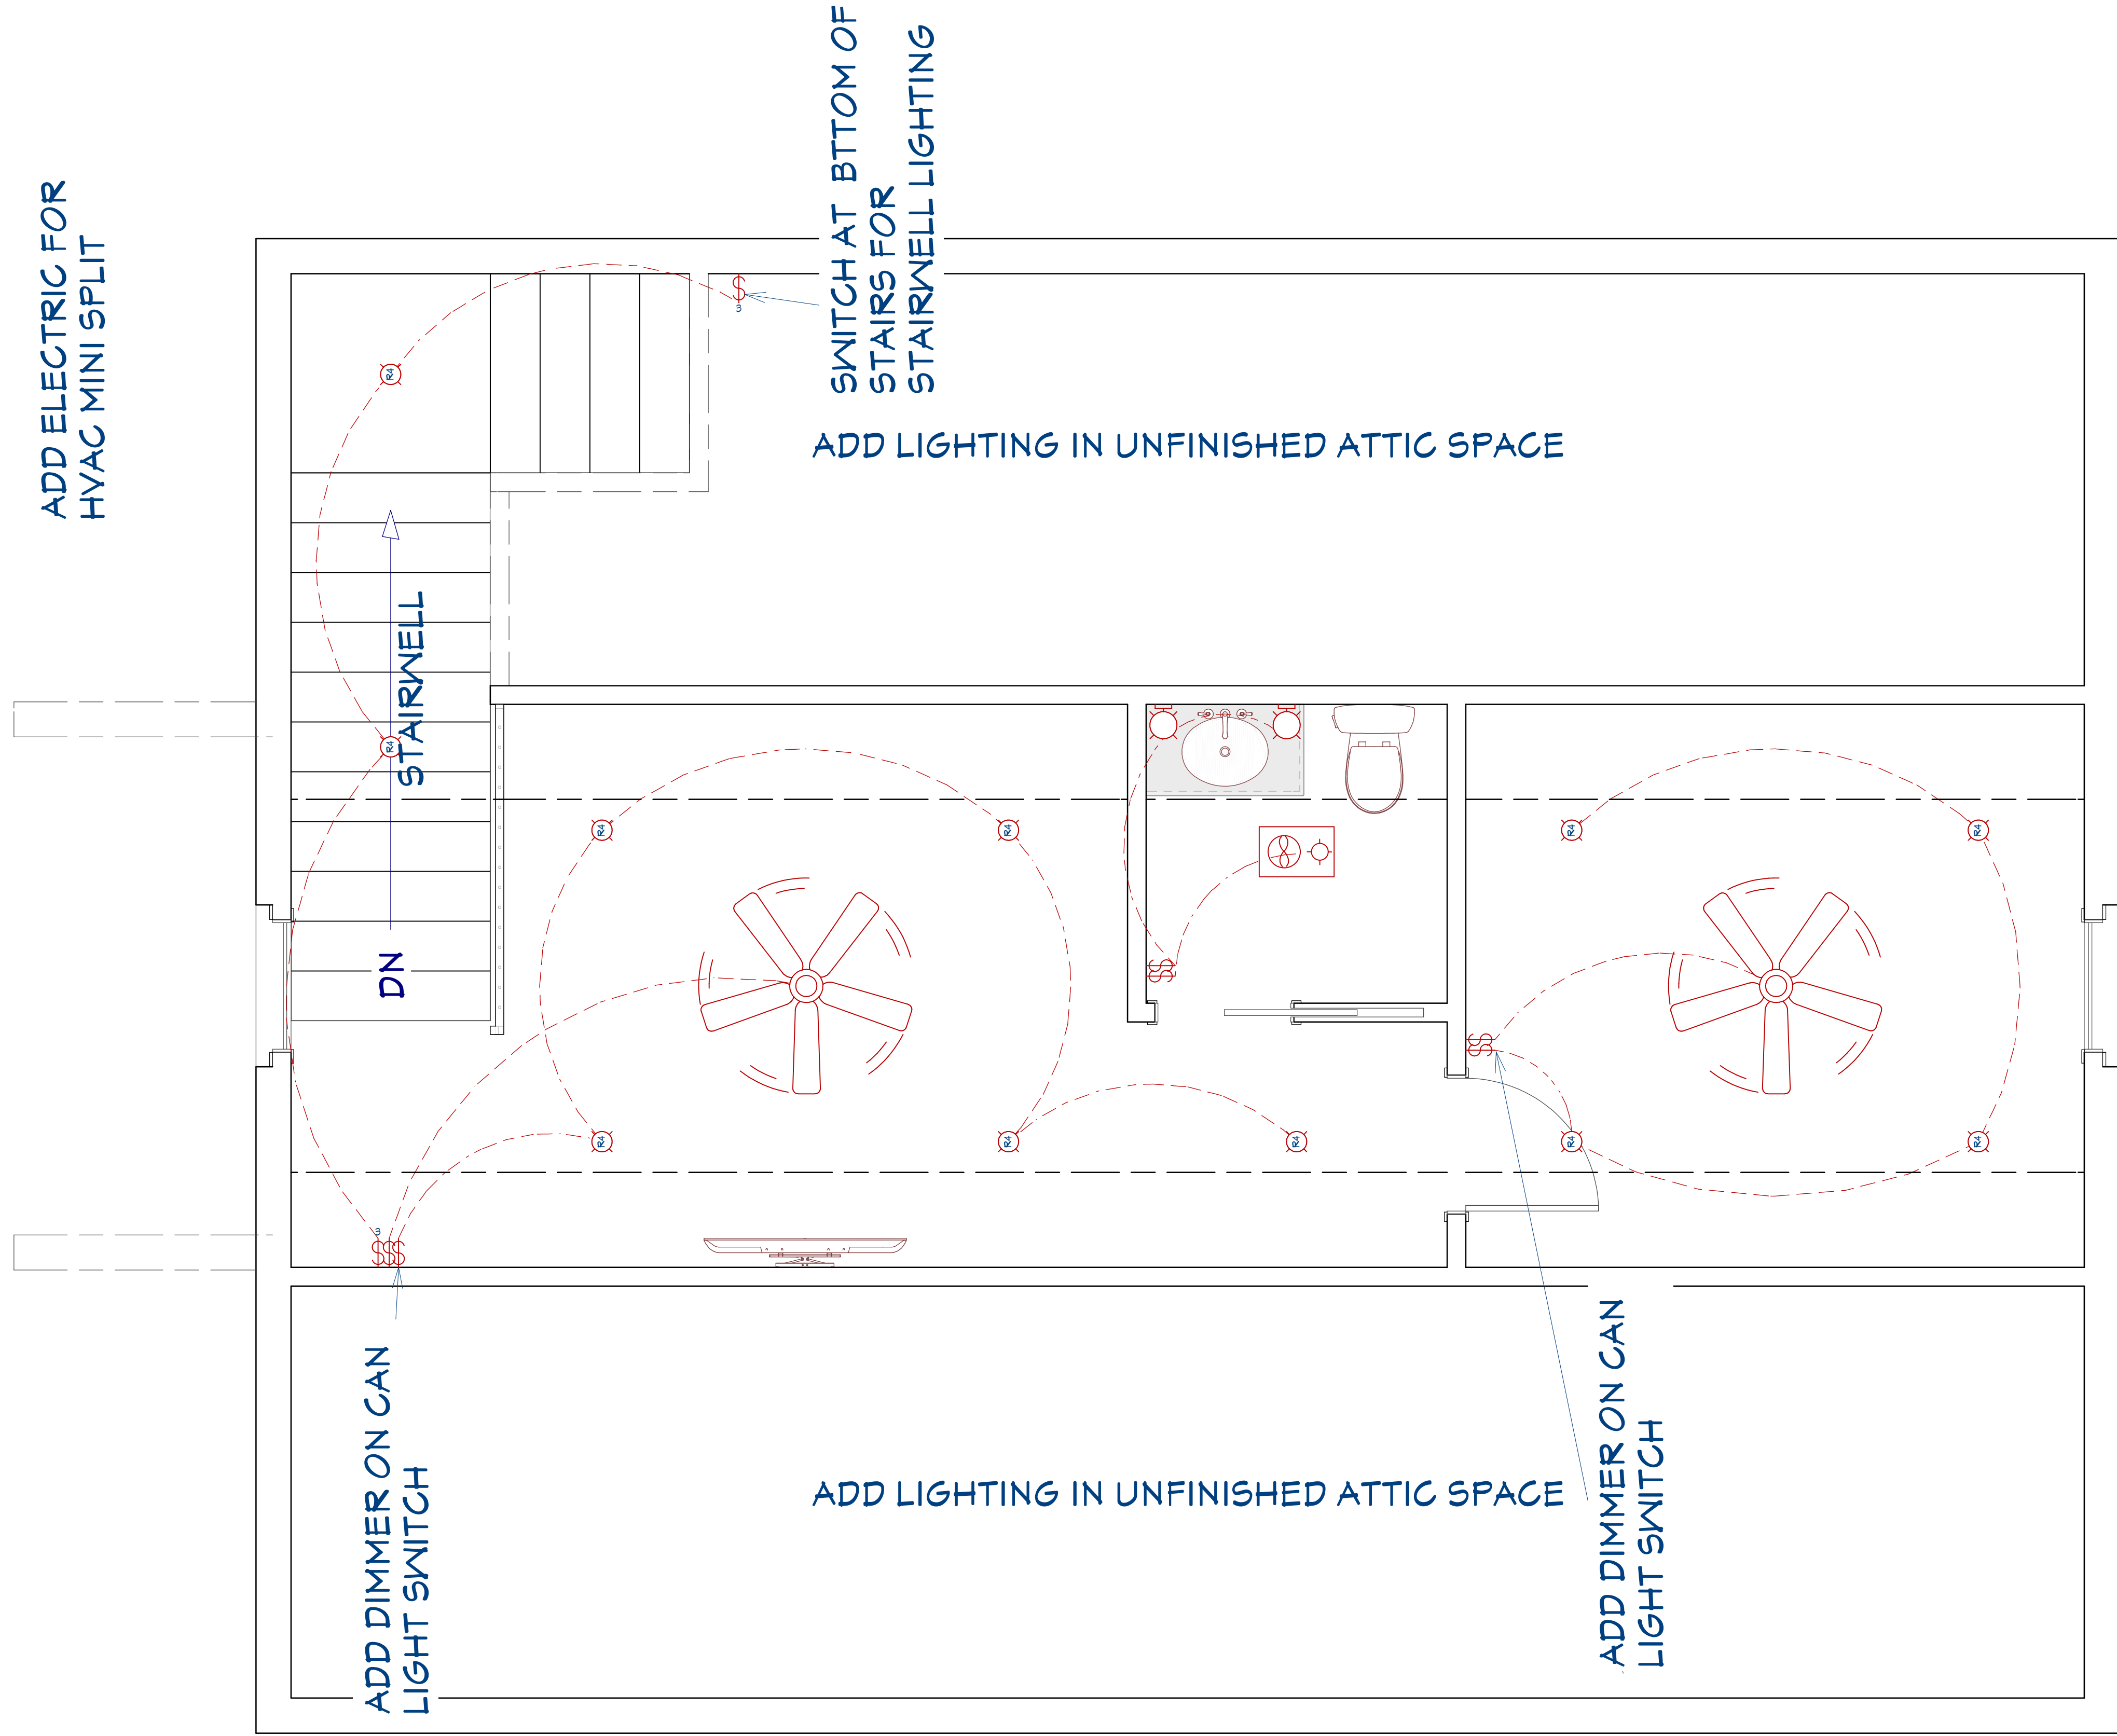


227 MARENGO DR.
RICHMOND, KY 40475

DEBOARD RESIDENCE

ELECTRIC
PLAN
(ATTIC)

DATE
JUNE 12,
2025

SHEET #
A10

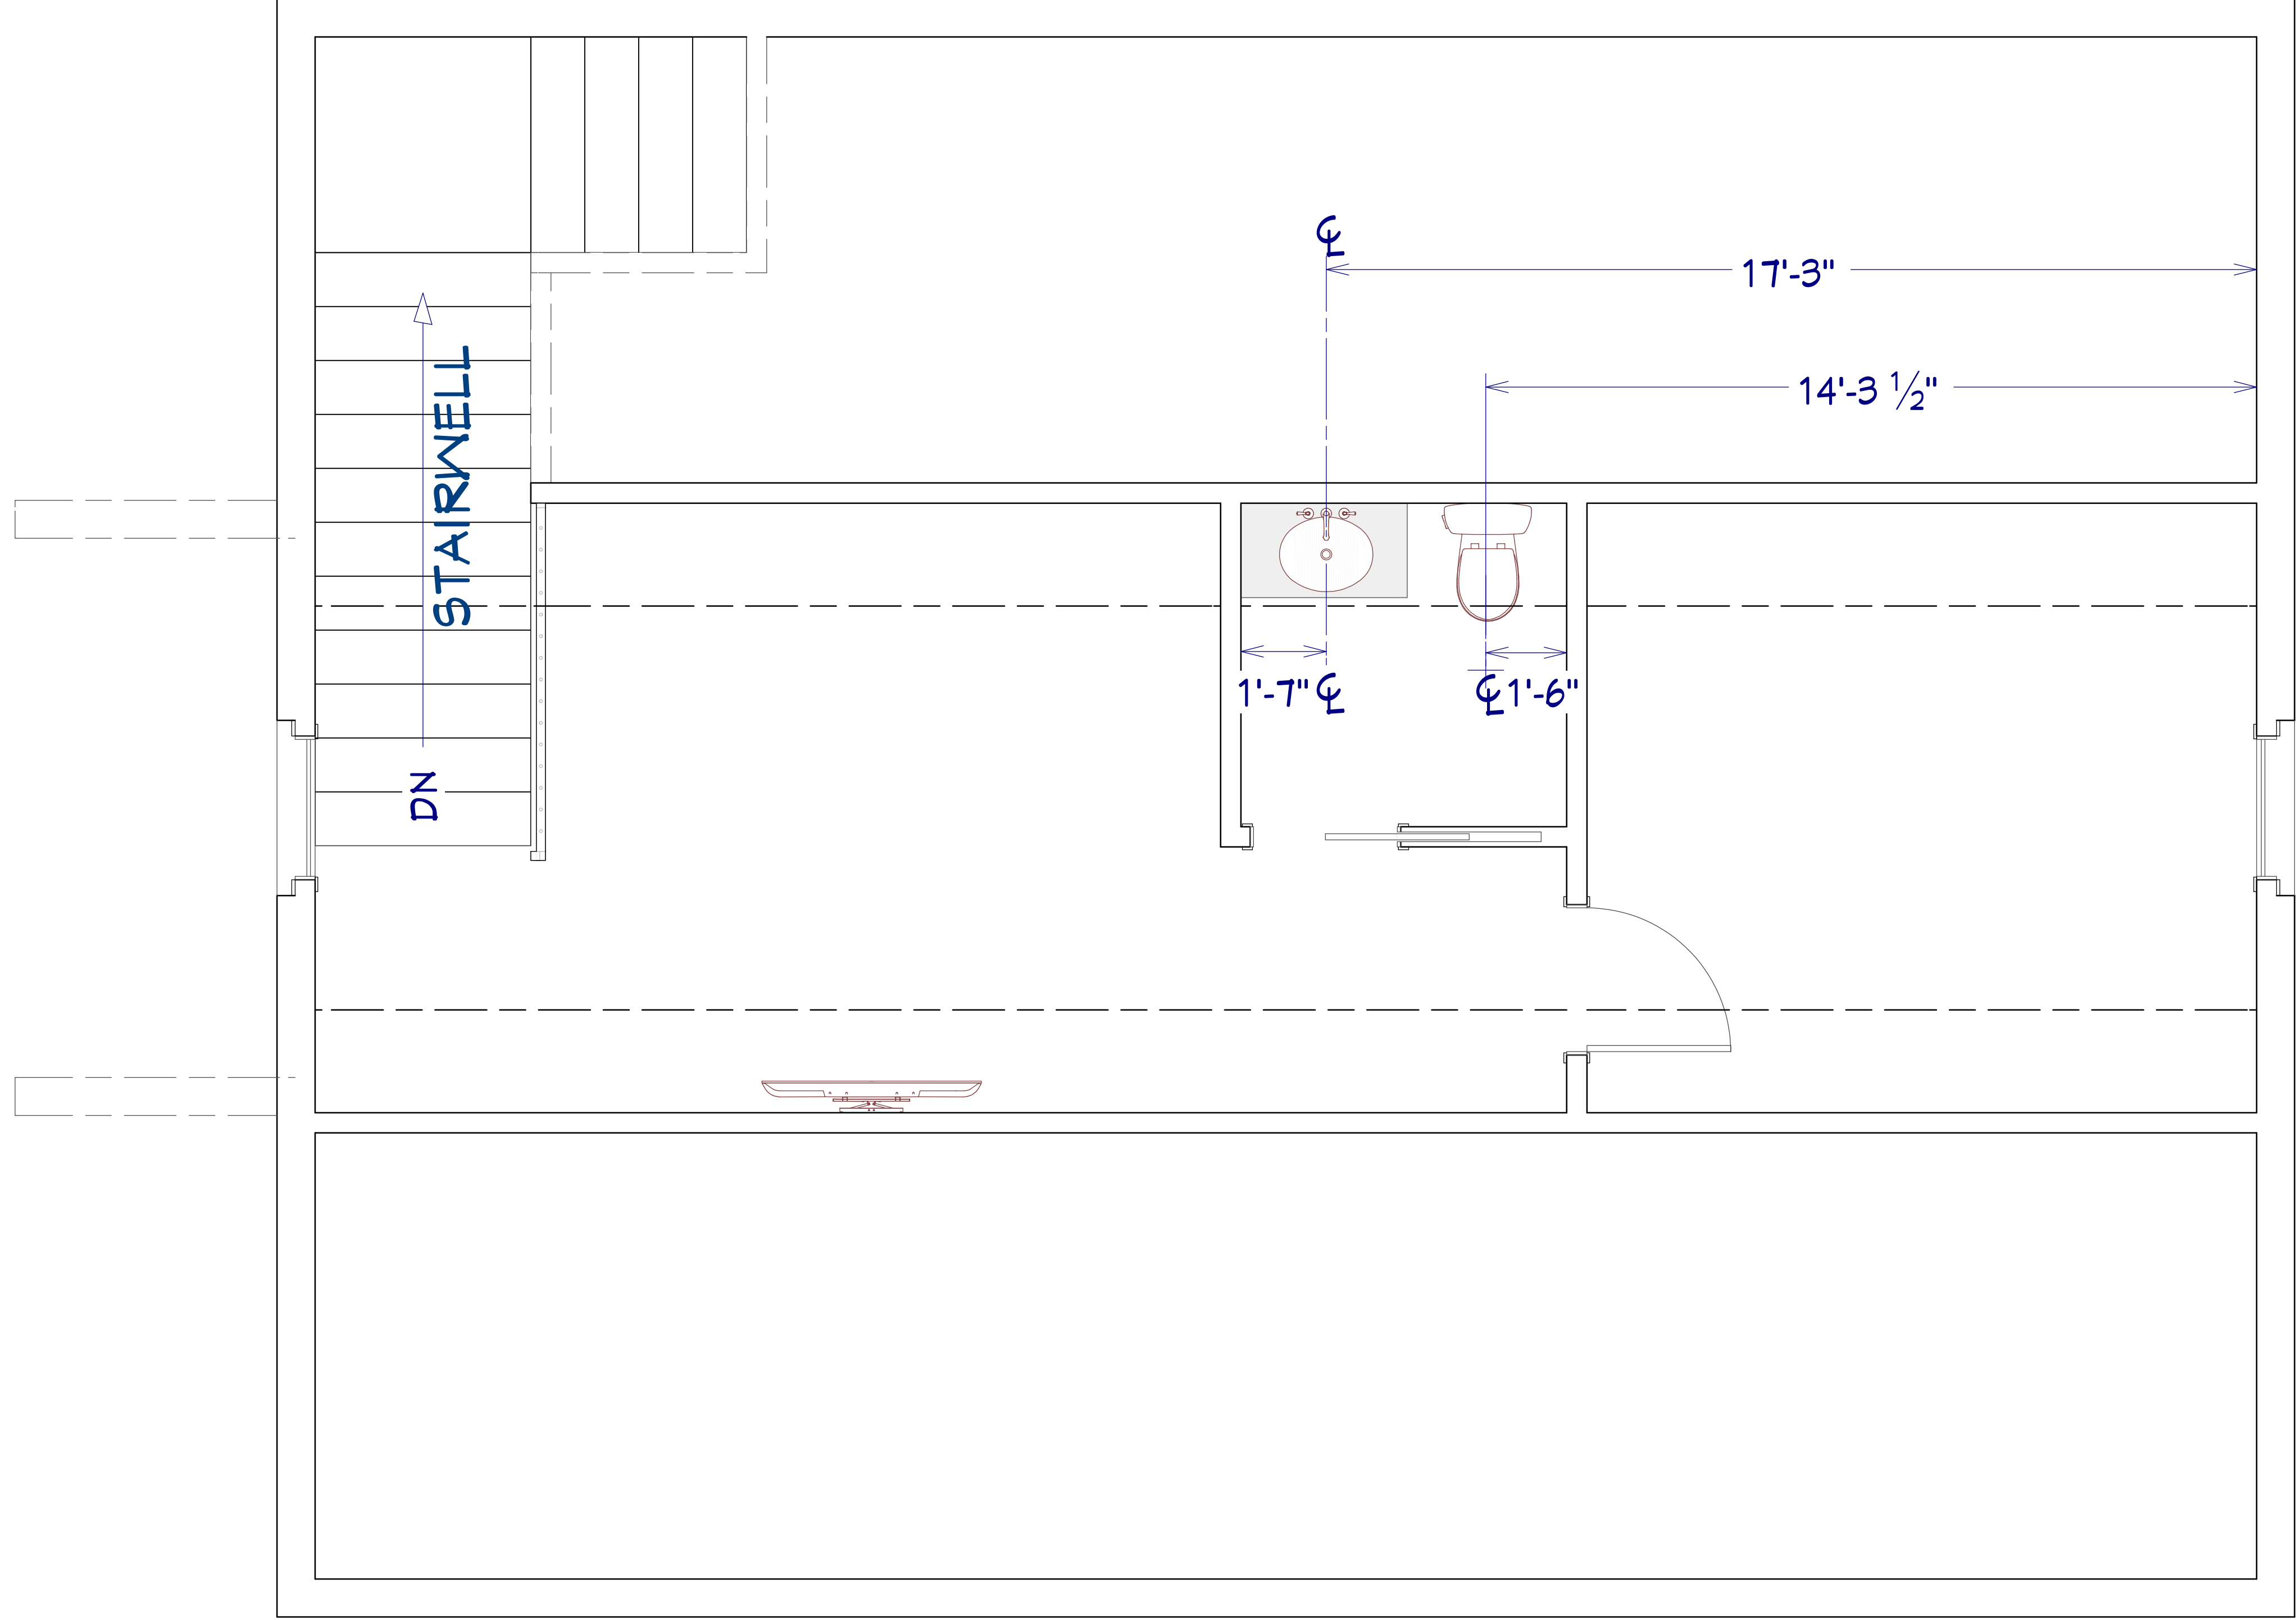

OPTION TO LOOK AT PUTTING HALF BATH IN GARAGE FOR ACCESS FROM POOL



227 MARENGO DR.
RICHMOND, KY 40475

DEBOARD RESIDENCE


PLUMBING PLAN

DATE

JUNE 12,
2025

SHEET #

A11

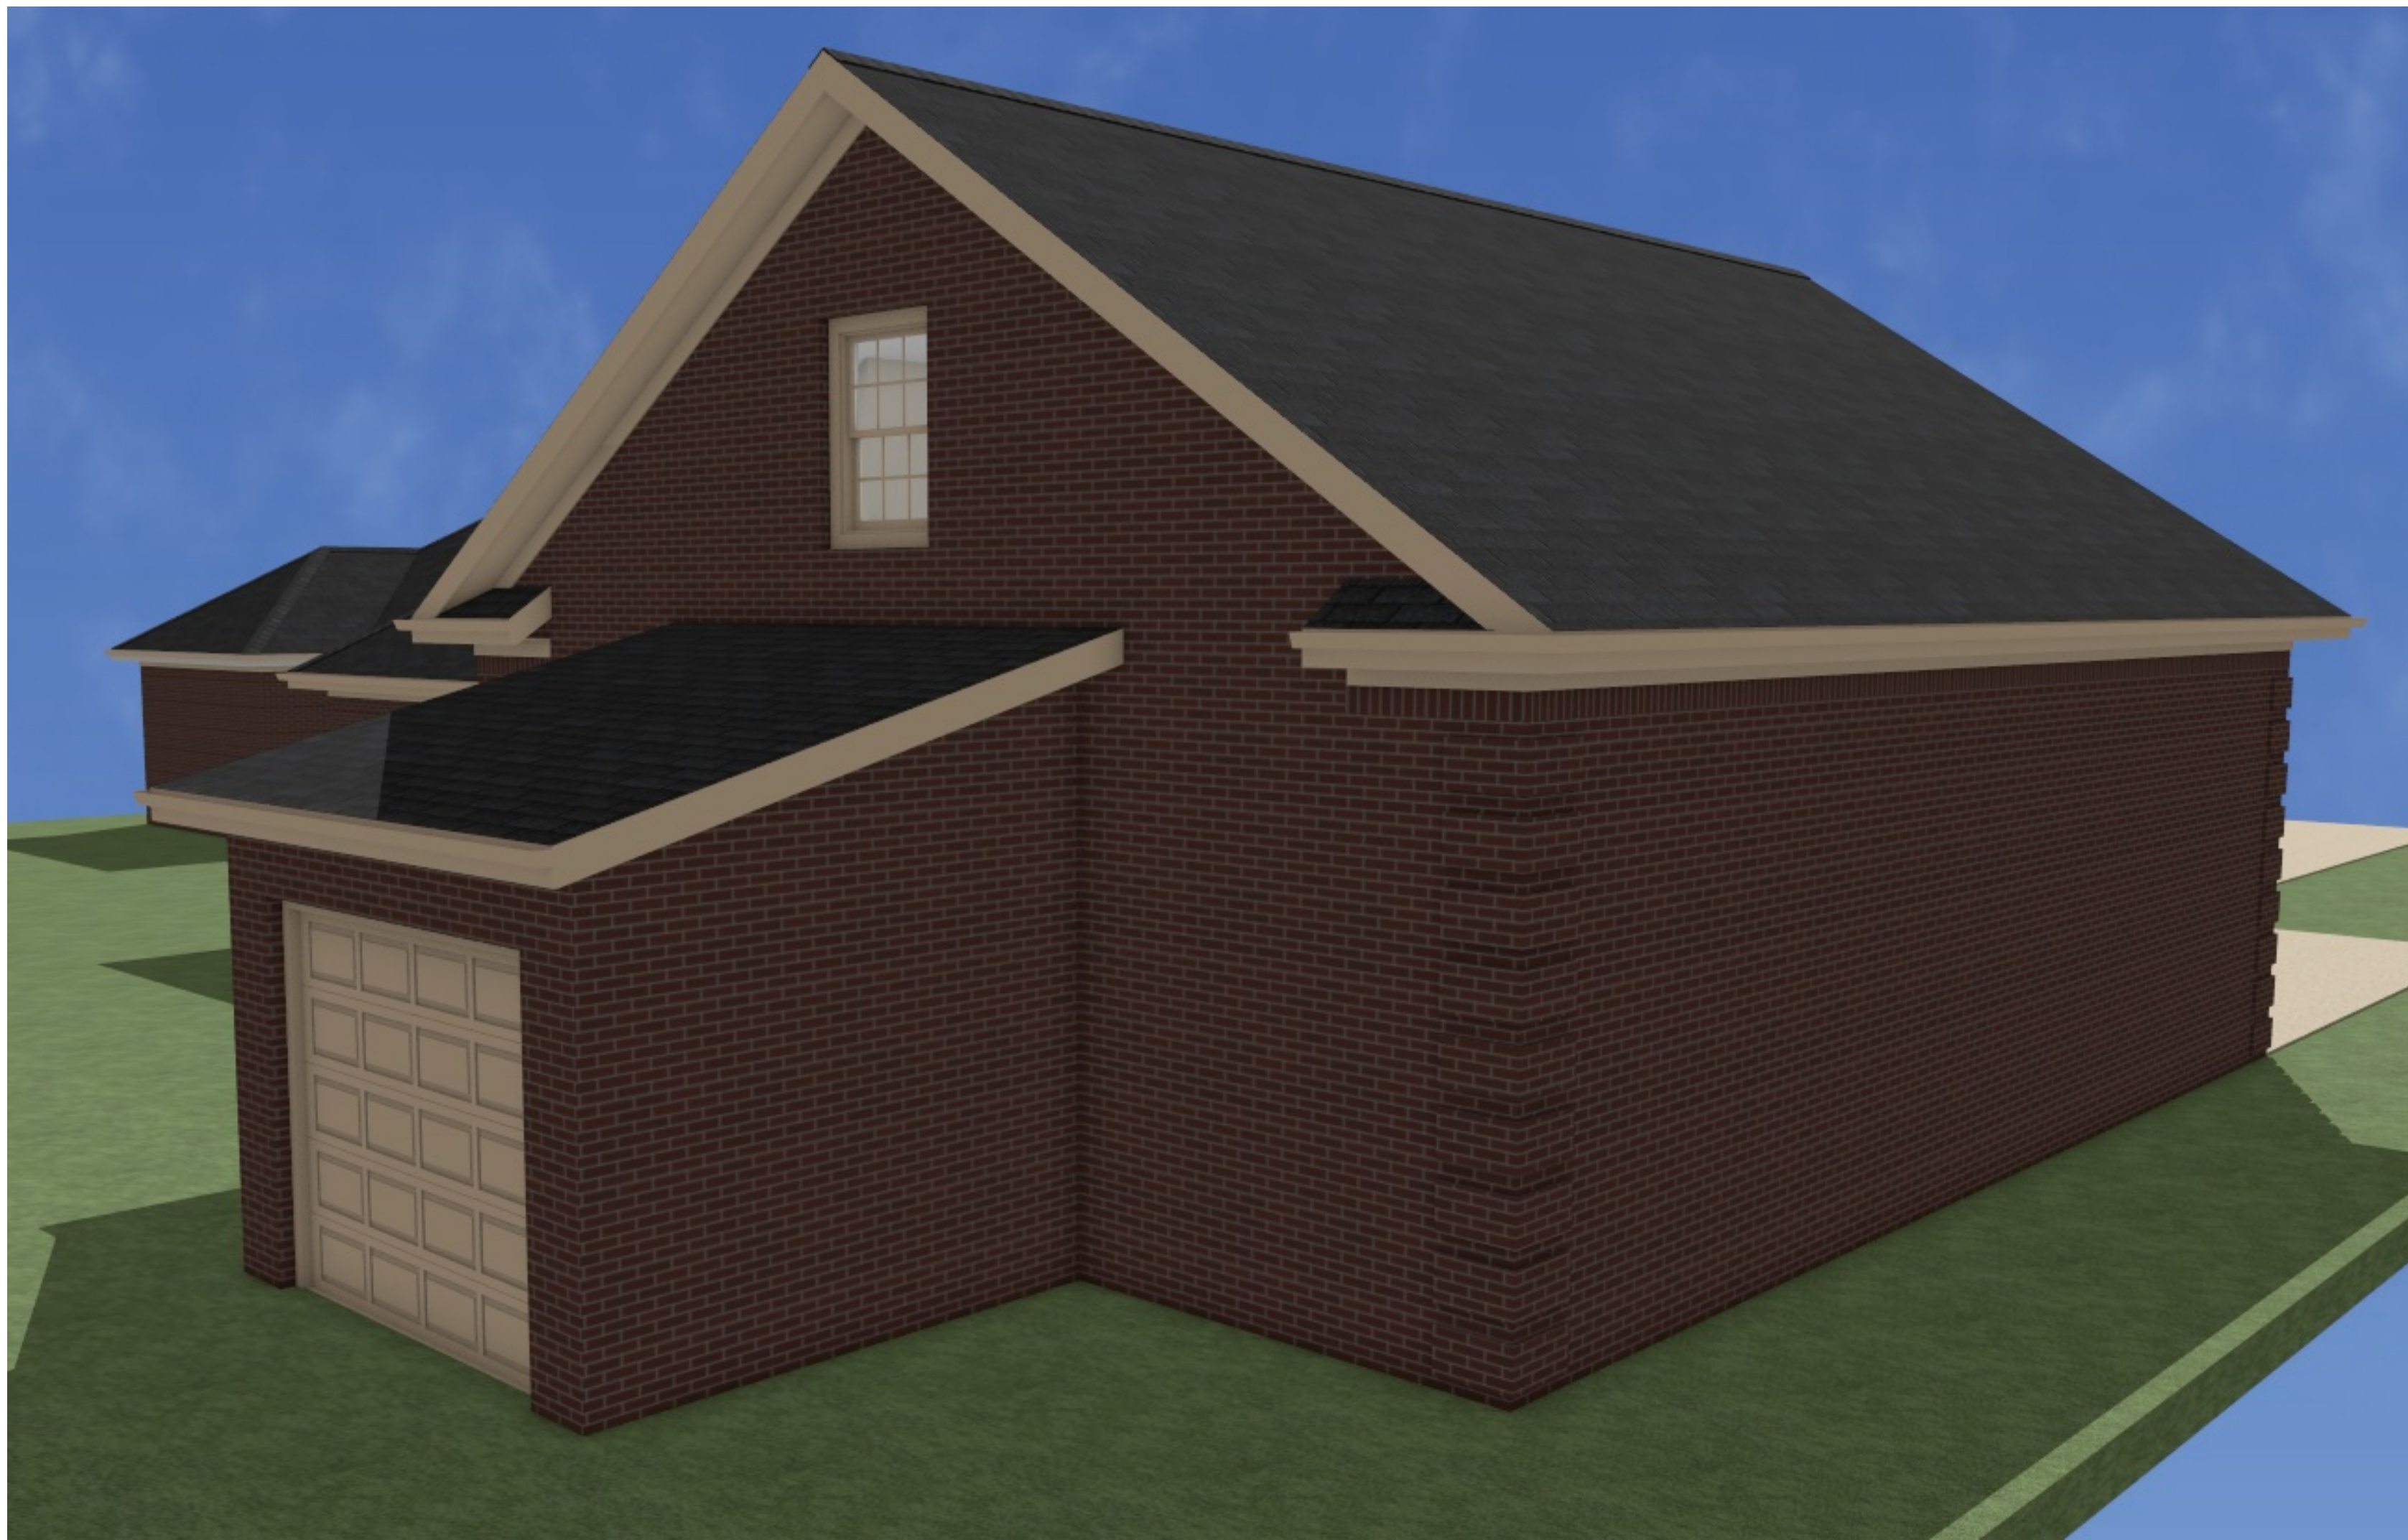



227 MARENGO DR.
RICHMOND, KY 40475

DEBOARD RESIDENCE

3D
CAPTURE

DATE
JUNE 12,
2025

SHEET #

A13



SHEET #		A14
DATE		JUNE 12, 2025
3D CAPTURE		
227 MARENGO DR. RICHMOND, KY 40475		DEBOARD RESIDENCE
J & Construction DESIGN - BUILD - REMODEL		