



CARVER/JULIAN
RESIDENCE


EXISTING FLOOR PLAN

DATE	JUNE 4, 2026
------	-----------------

SHEET #	A01
---------	-----

REMOVE VANITY CABINETS,
VANITY TOP, SINKS, FAUCETS,
MIRROR, AND LIGHTS.

REMOVE TOILET
AND REPLACE
WITH NEW IN SAME
LOCATION

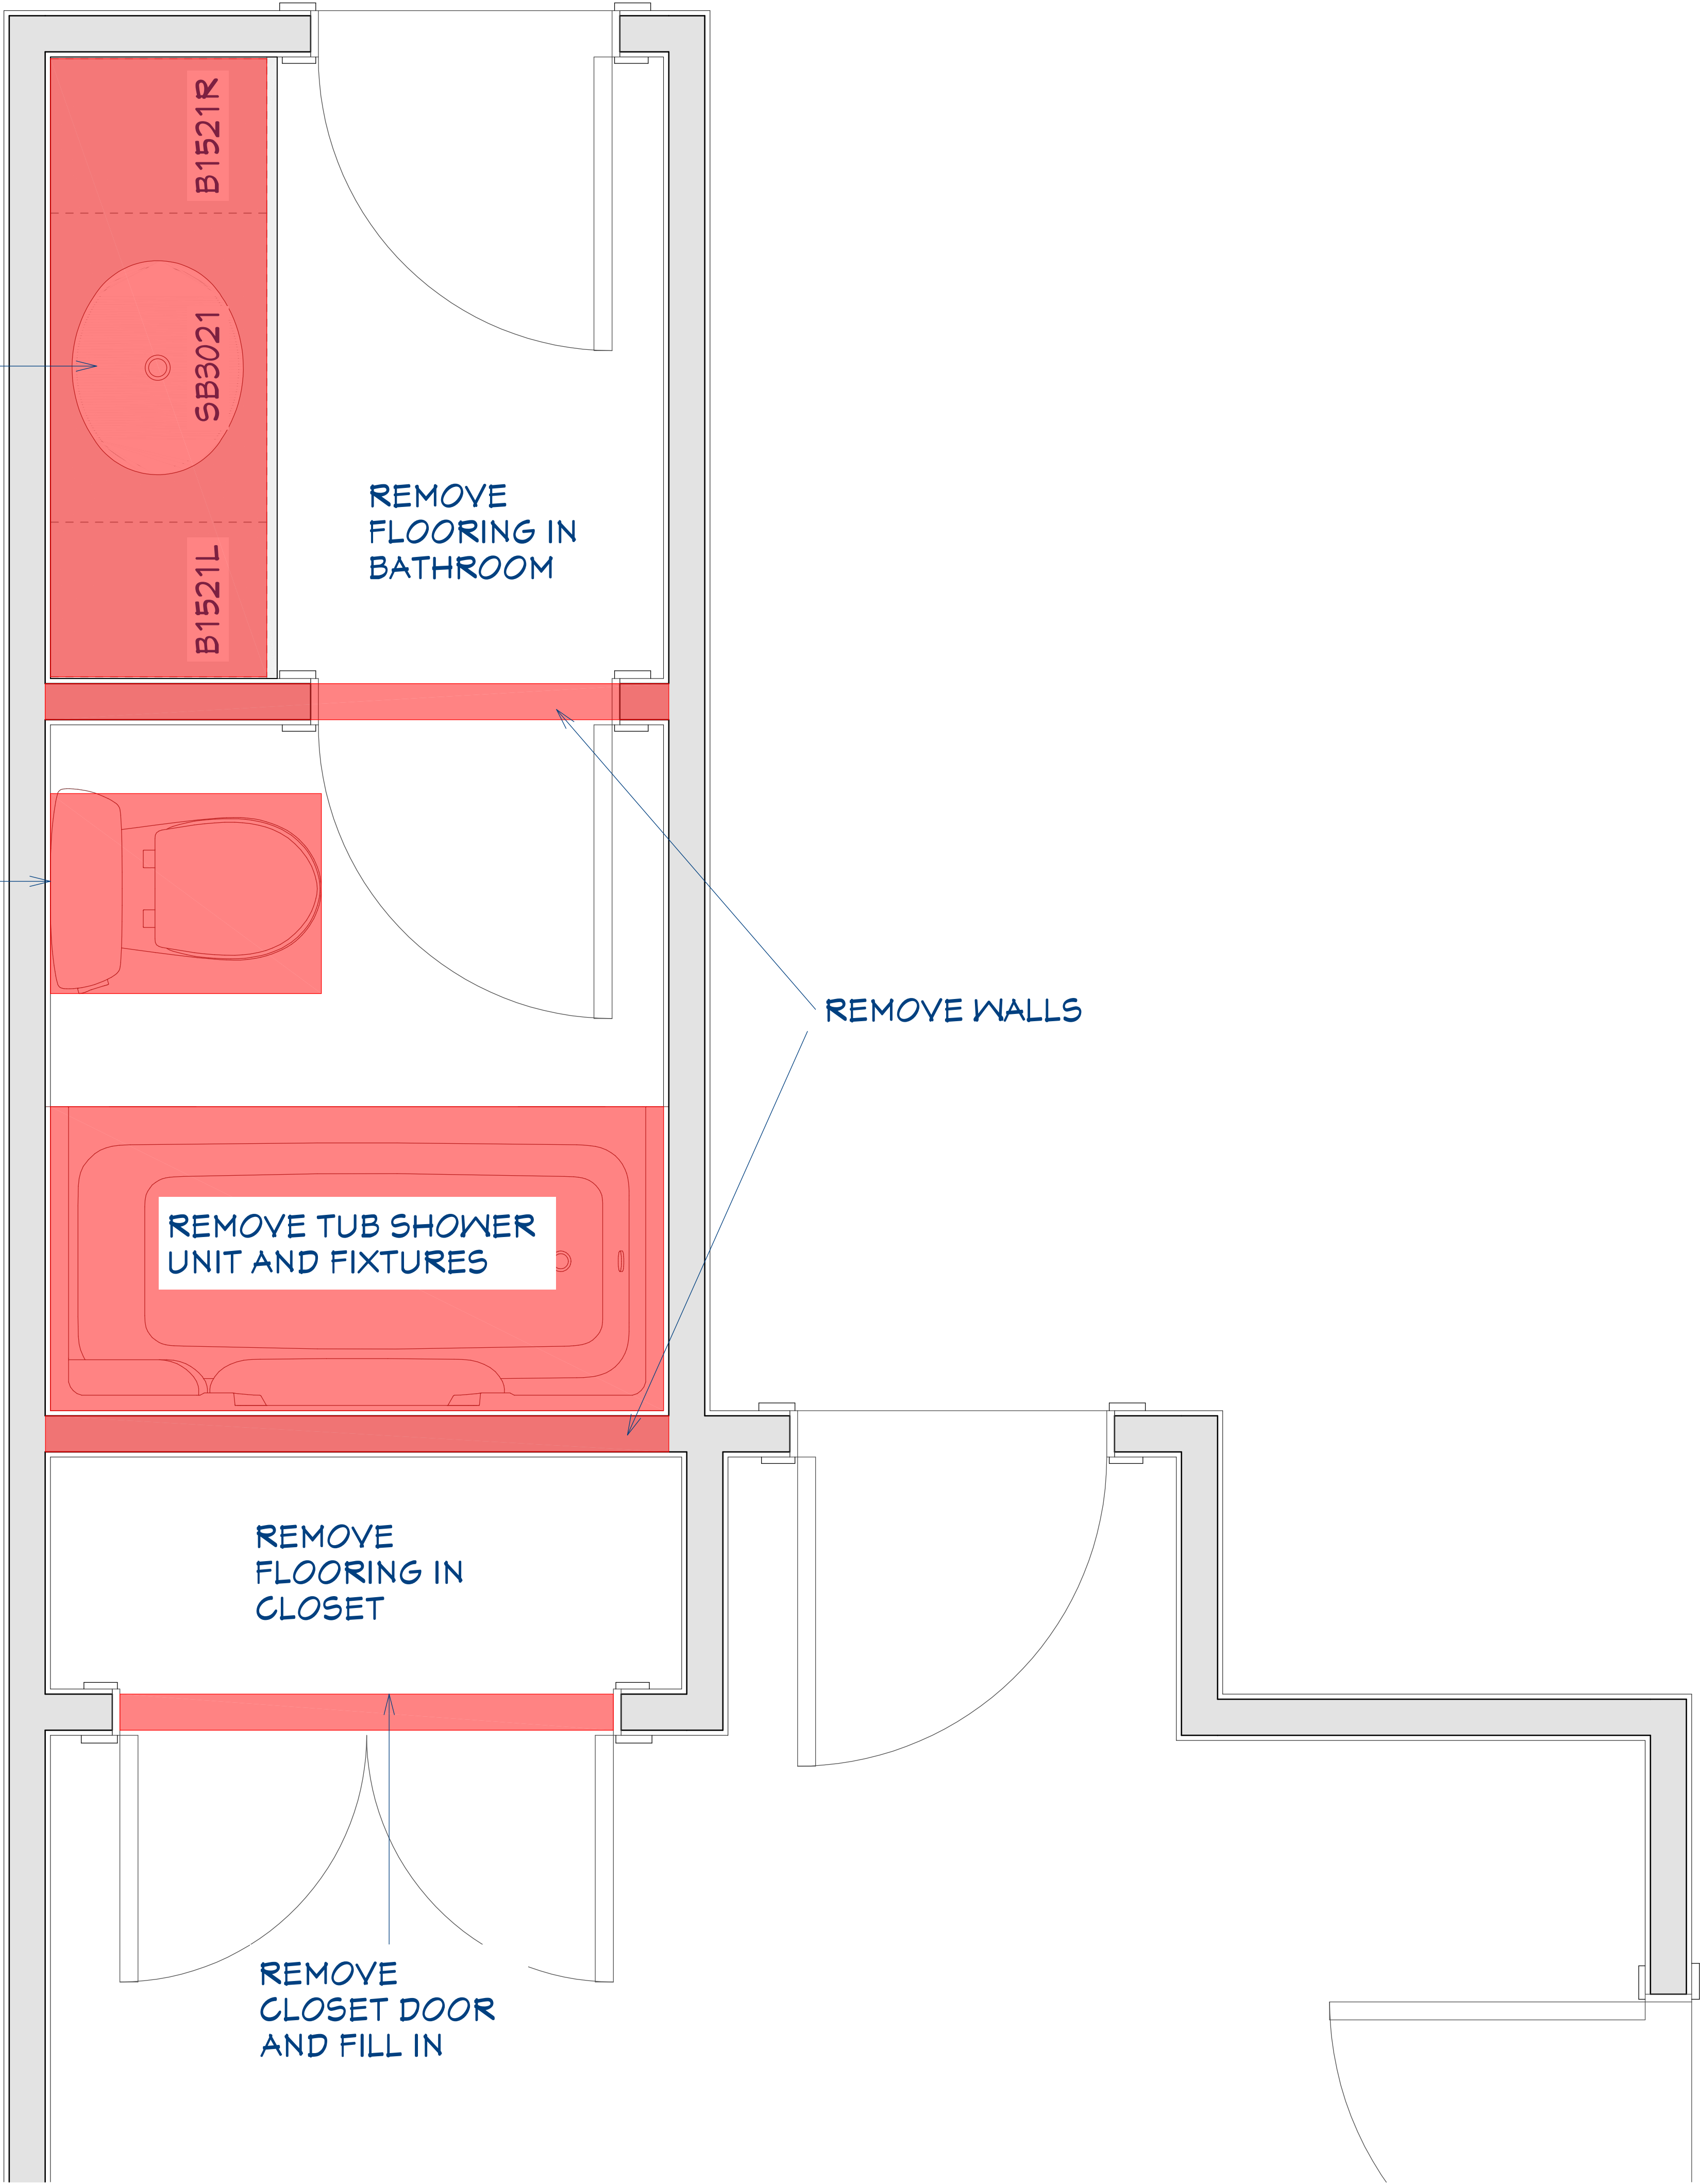

SHEET #		A02	
DATE		JUNE 4, 2026	
DEMO PLAN			
1035 WIL ROSE LN. VERSAILLES, KY 40383		CARVER/JULIAN RESIDENCE	
 J&R Construction DESIGN · BUILD · REMODEL			



CONFIRM ALL LOCATIONS & HEIGHTS WITH CLIENT

INSTALL NEW 8" TOWEL BAR 20" FROM VANITY TOP

INSTALL TP HOLDER 26" FROM FLOOR

INSTALL NEW 24" TOWEL BAR 48" FROM FLOOR

ADD BLOCKING FOR SHOWER DOOR HINGES

ADD BLOCKING FOR HANDHELD ON VERTICAL GRAB BAR

ADD BLOCKING FOR FUTURE FOLDING TEAK BENCH


INSTALL 24" GRAB BAR 36" FROM FLOOR

ADD BLOCKING FOR GRAB BAR



ADD HEADER FOR 24" WIDE NICHE

SHEET #	A04
DATE	JUNE 4, 2026
FRAMING/ ACCESSORY PLACEMENT	
1035 WIL ROSE LN. VERSAILLES, KY 40383	CARVER/JULIAN RESIDENCE


CONFIRM ALL LOCATIONS & HEIGHTS WITH CLIENT

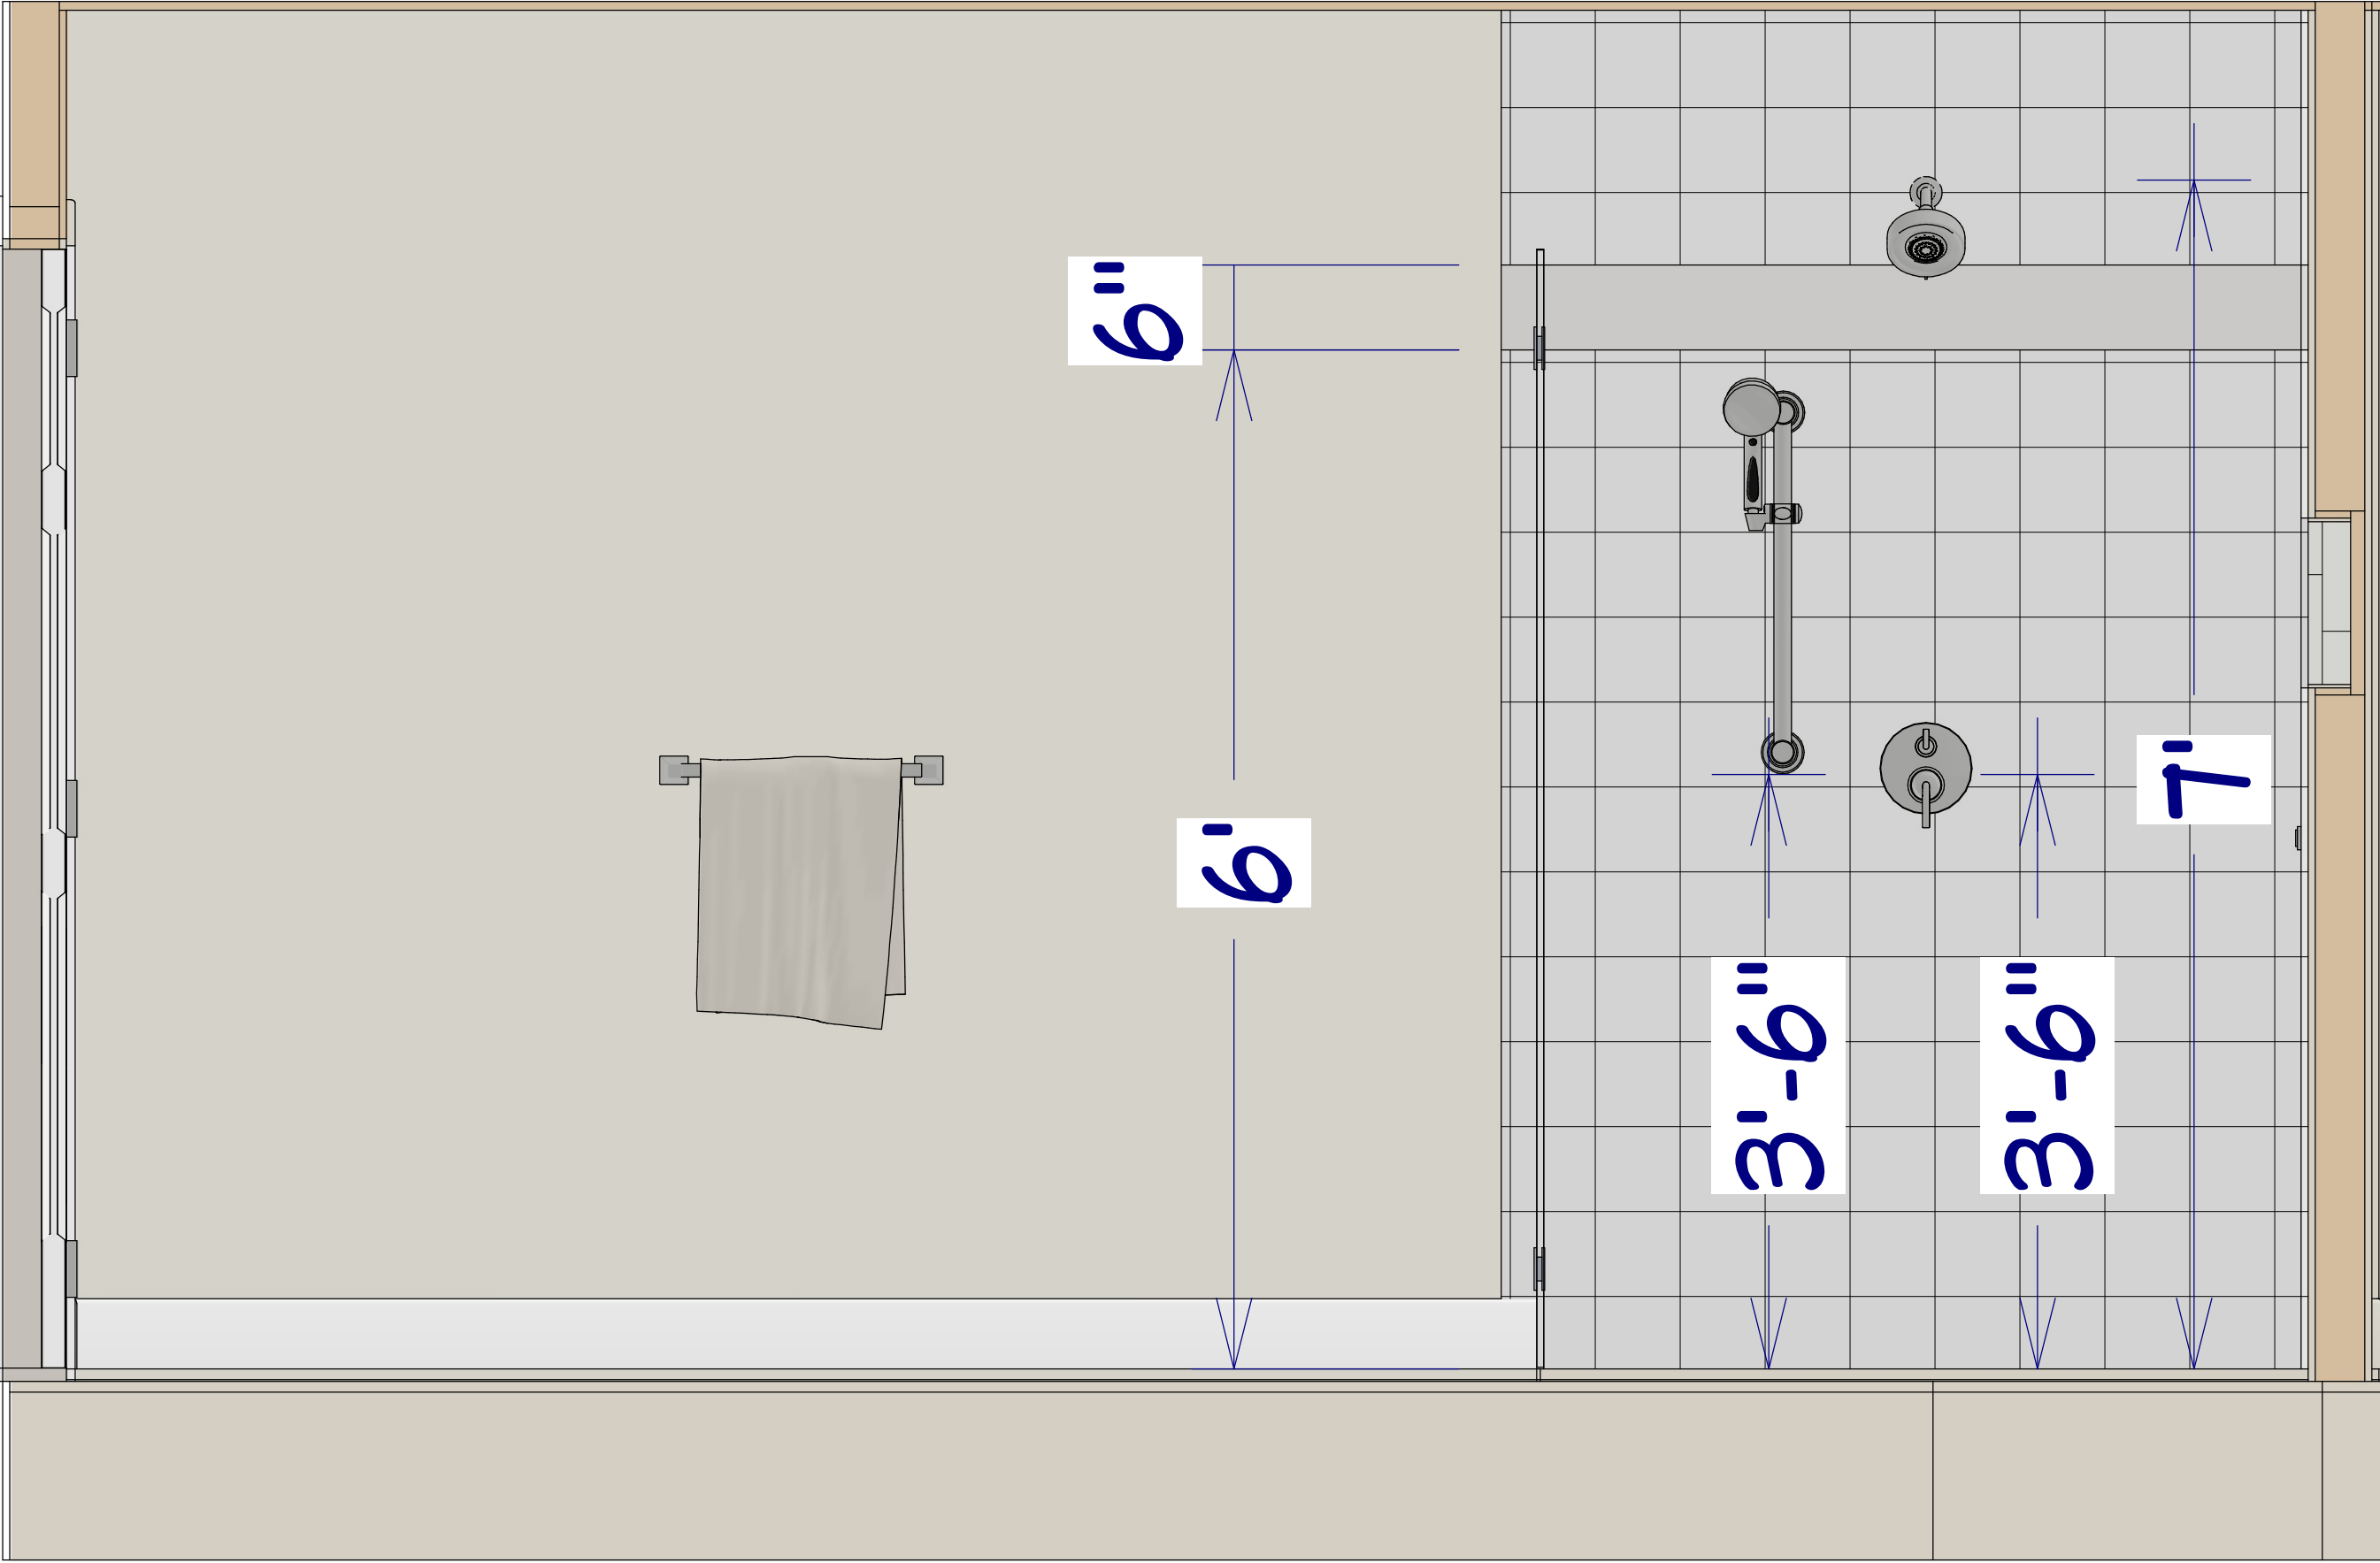

NICHE IS TO BE ADJUSTED
AS NEEDED TO BE INLINE
WITH TILE ROW

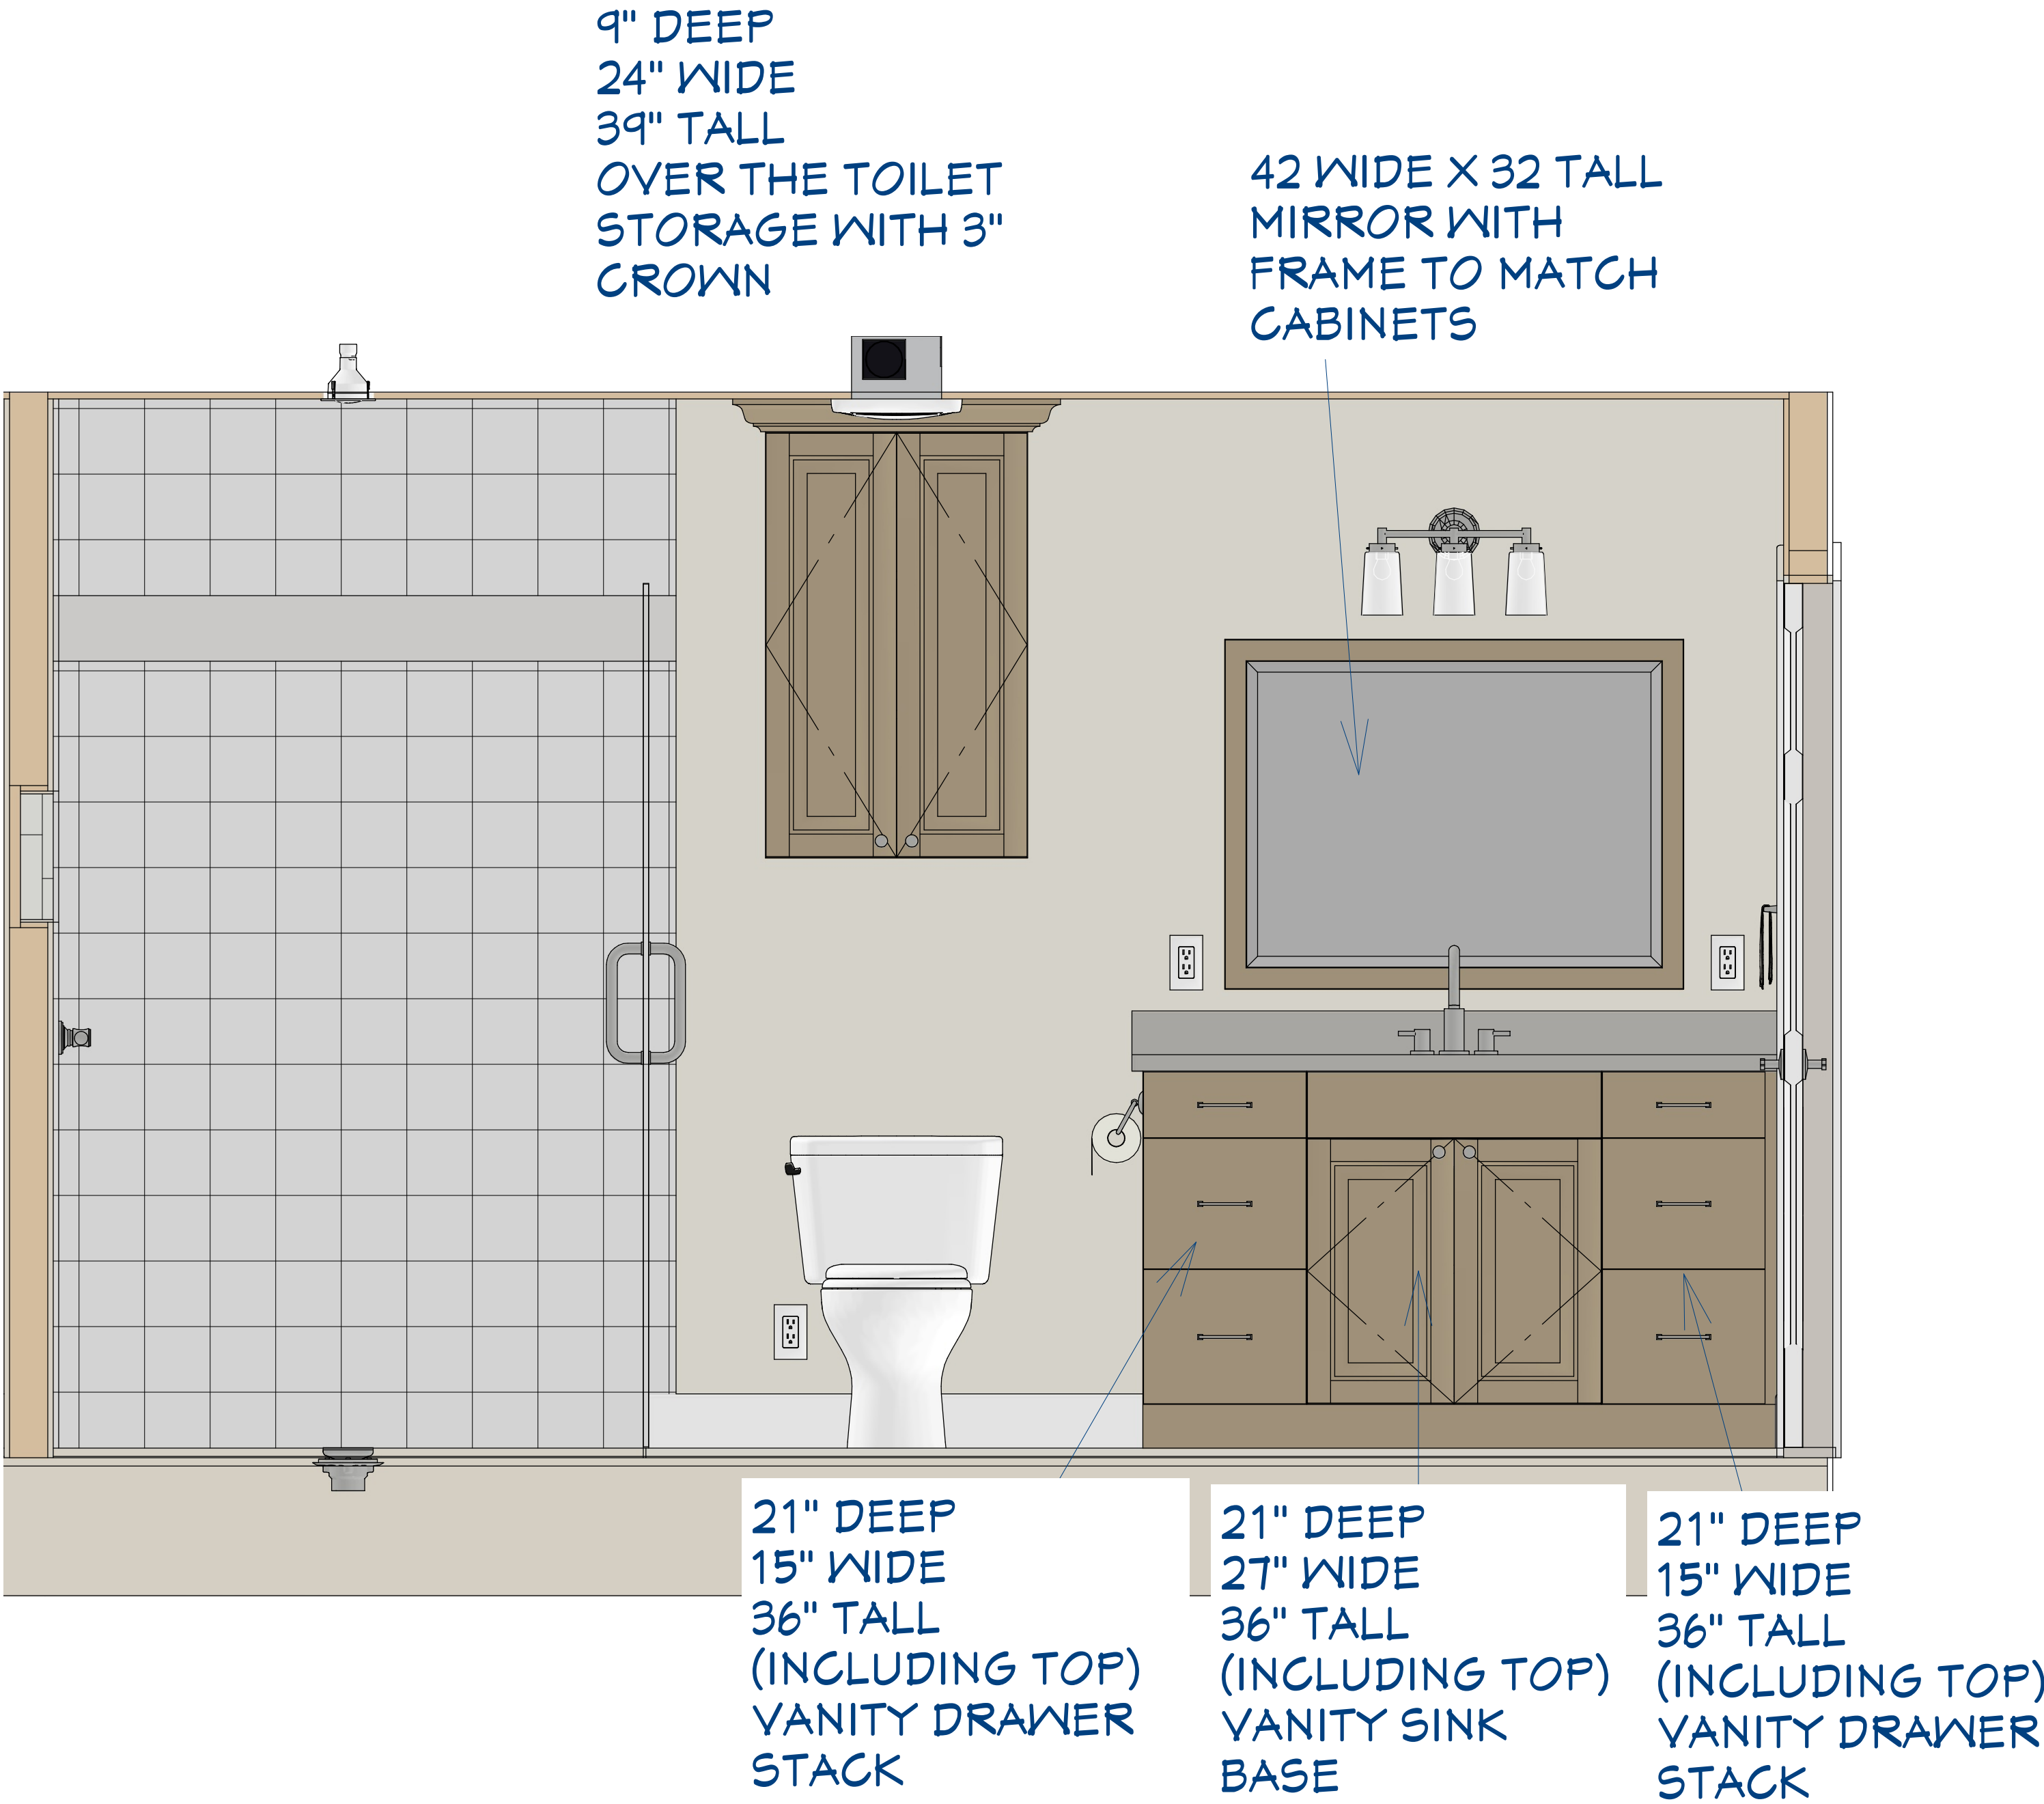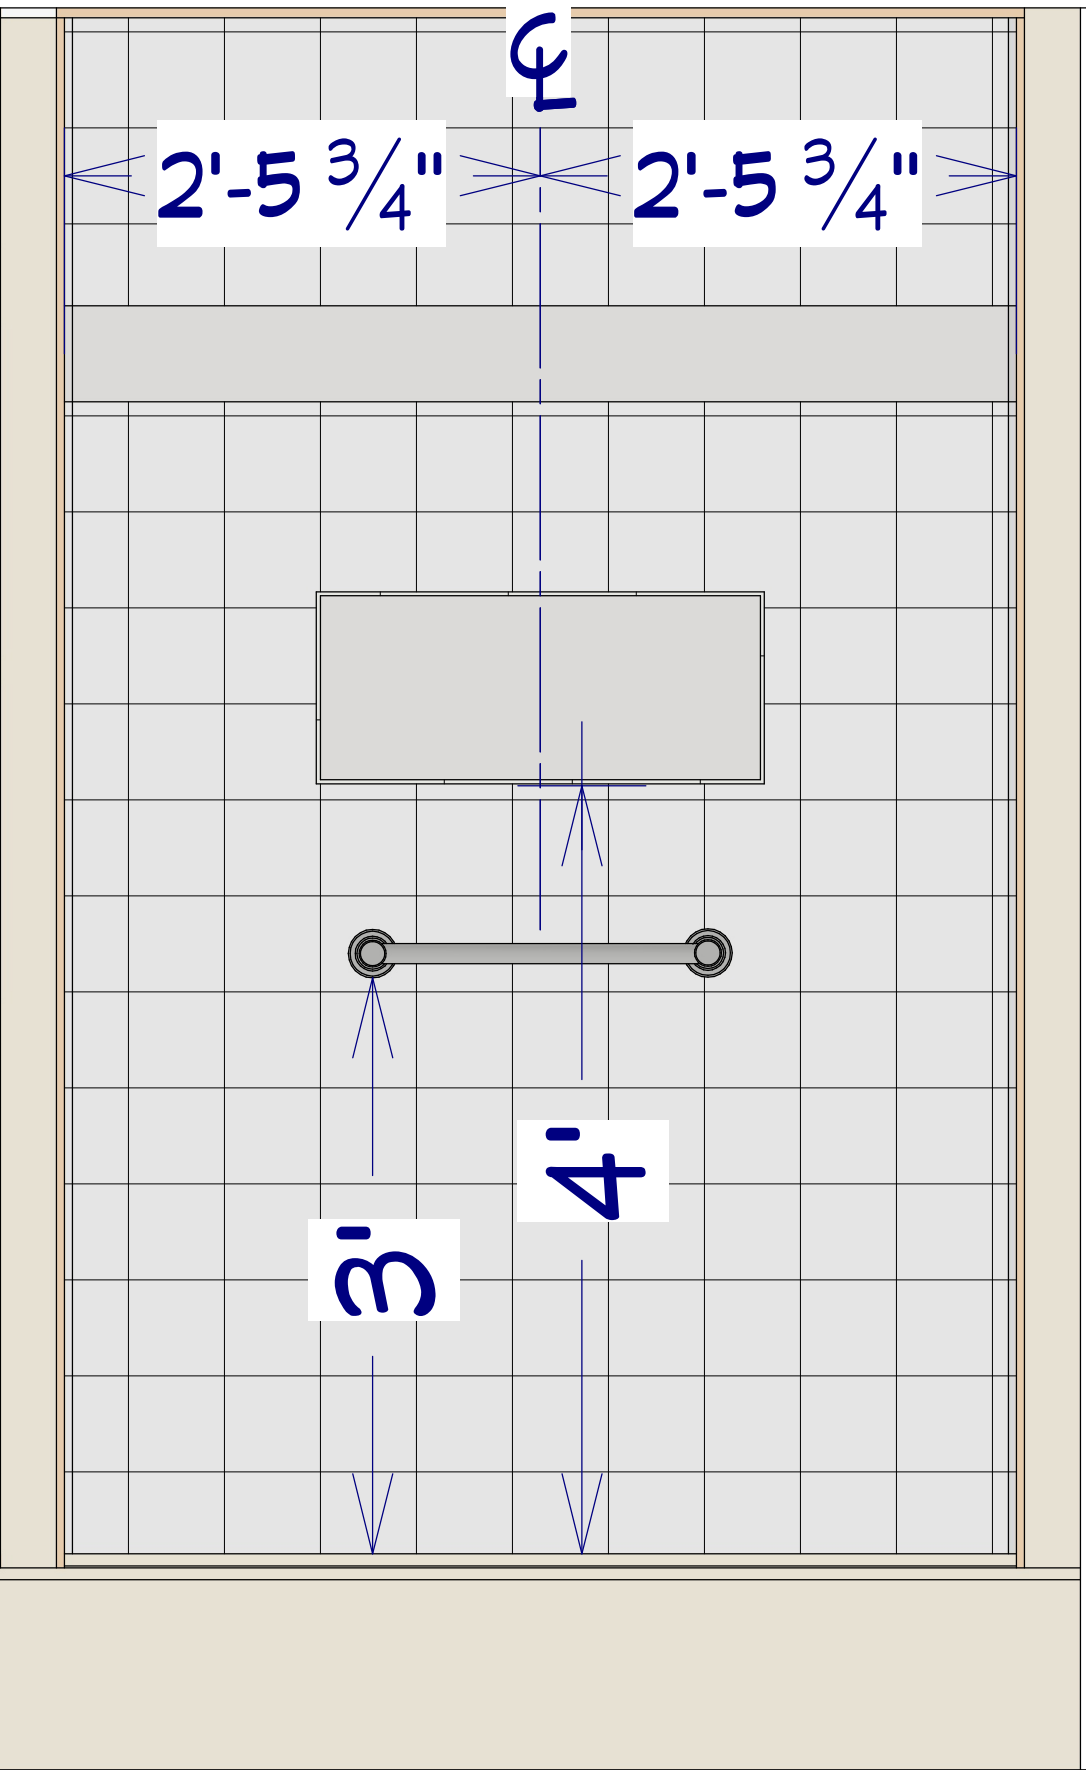

CONFIRM ALL LOCATIONS & HEIGHTS WITH CLIENT

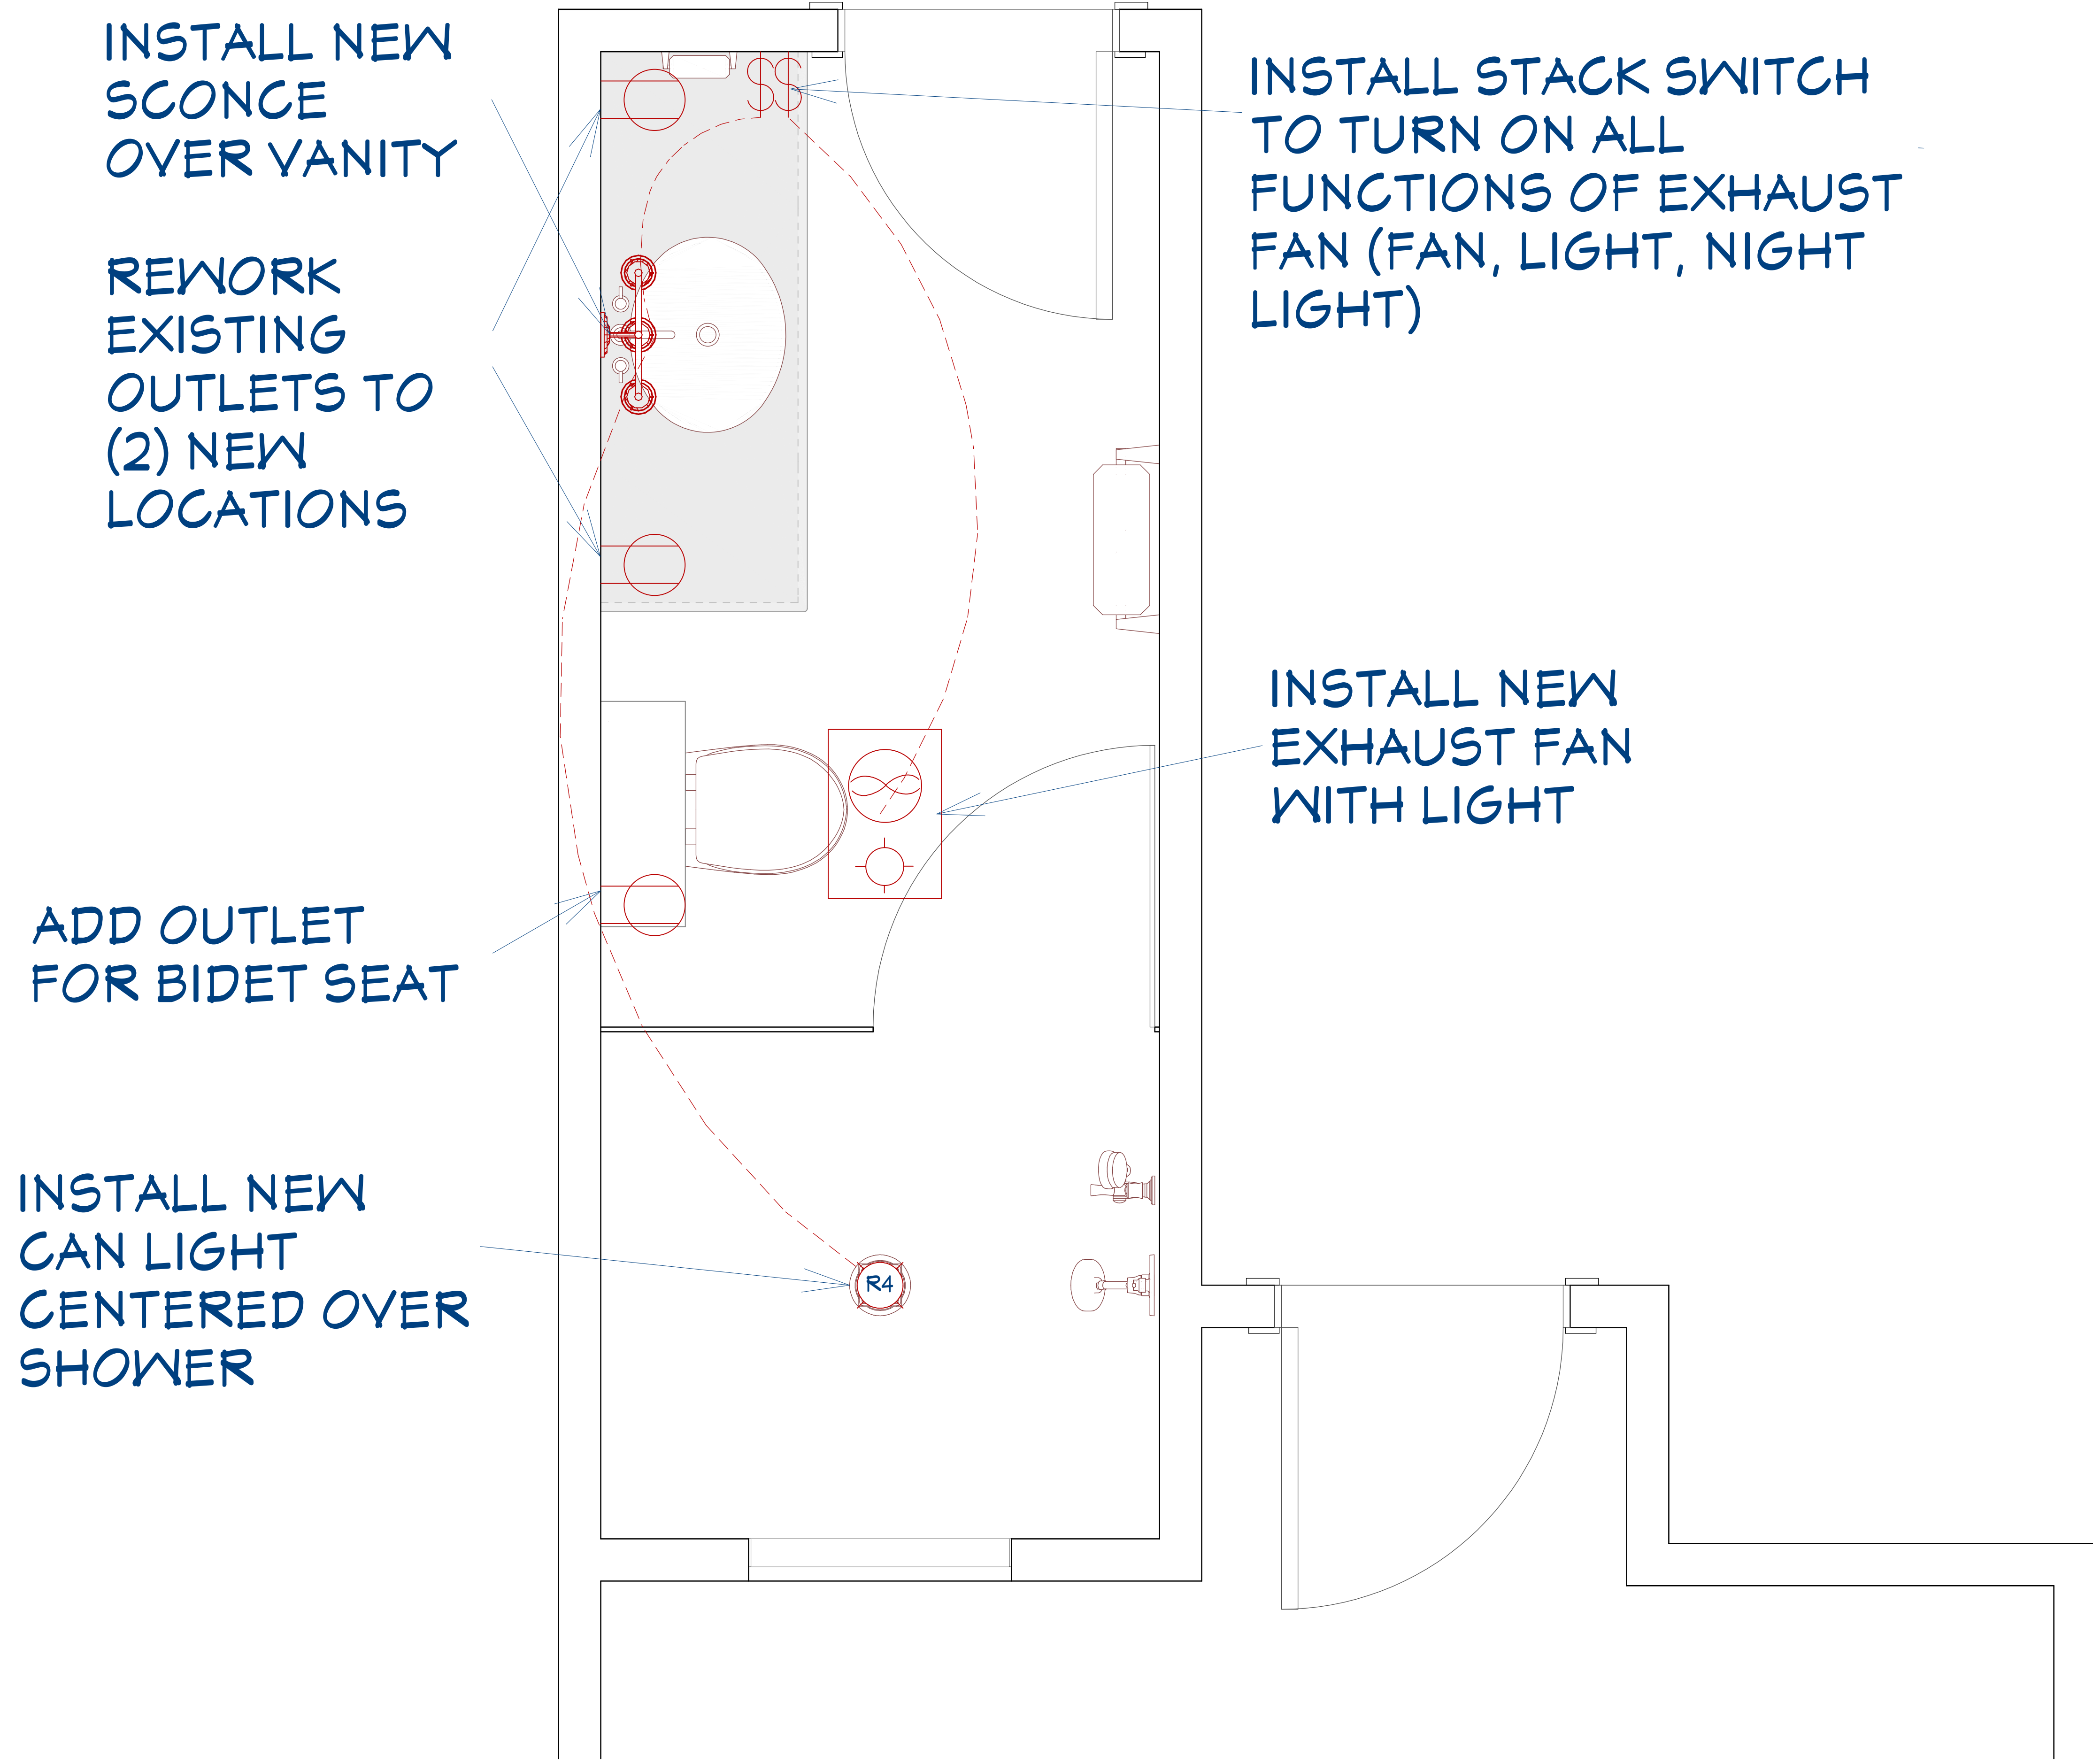

INSTALL NEW
SCONCE
OVER VANITY

REWORK
EXISTING
OUTLETS TO
(2) NEW
LOCATIONS

ADD OUTLET
FOR BIDET SEAT

INSTALL NEW
CAN LIGHT
CENTERED OVER
SHOWER

INSTALL STACK SWITCH
TO TURN ON ALL
FUNCTIONS OF EXHAUST
FAN (FAN, LIGHT, NIGHT
LIGHT)

INSTALL NEW
EXHAUST FAN
WITH LIGHT

SHEET #	A06
DATE	JUNE 4, 2026
ELECTRIC PLAN	
1035 WIL ROSE LN. VERSAILLES, KY 40383	CARVER/JULIAN RESIDENCE

