




	
1035 WIL ROSE LN. VERSAILLES, KY 40383	
CARVER/JULIAN RESIDENCE	
EXISTING FLOOR PLAN	
DATE JUNE 4, 2026	SHEET # A01

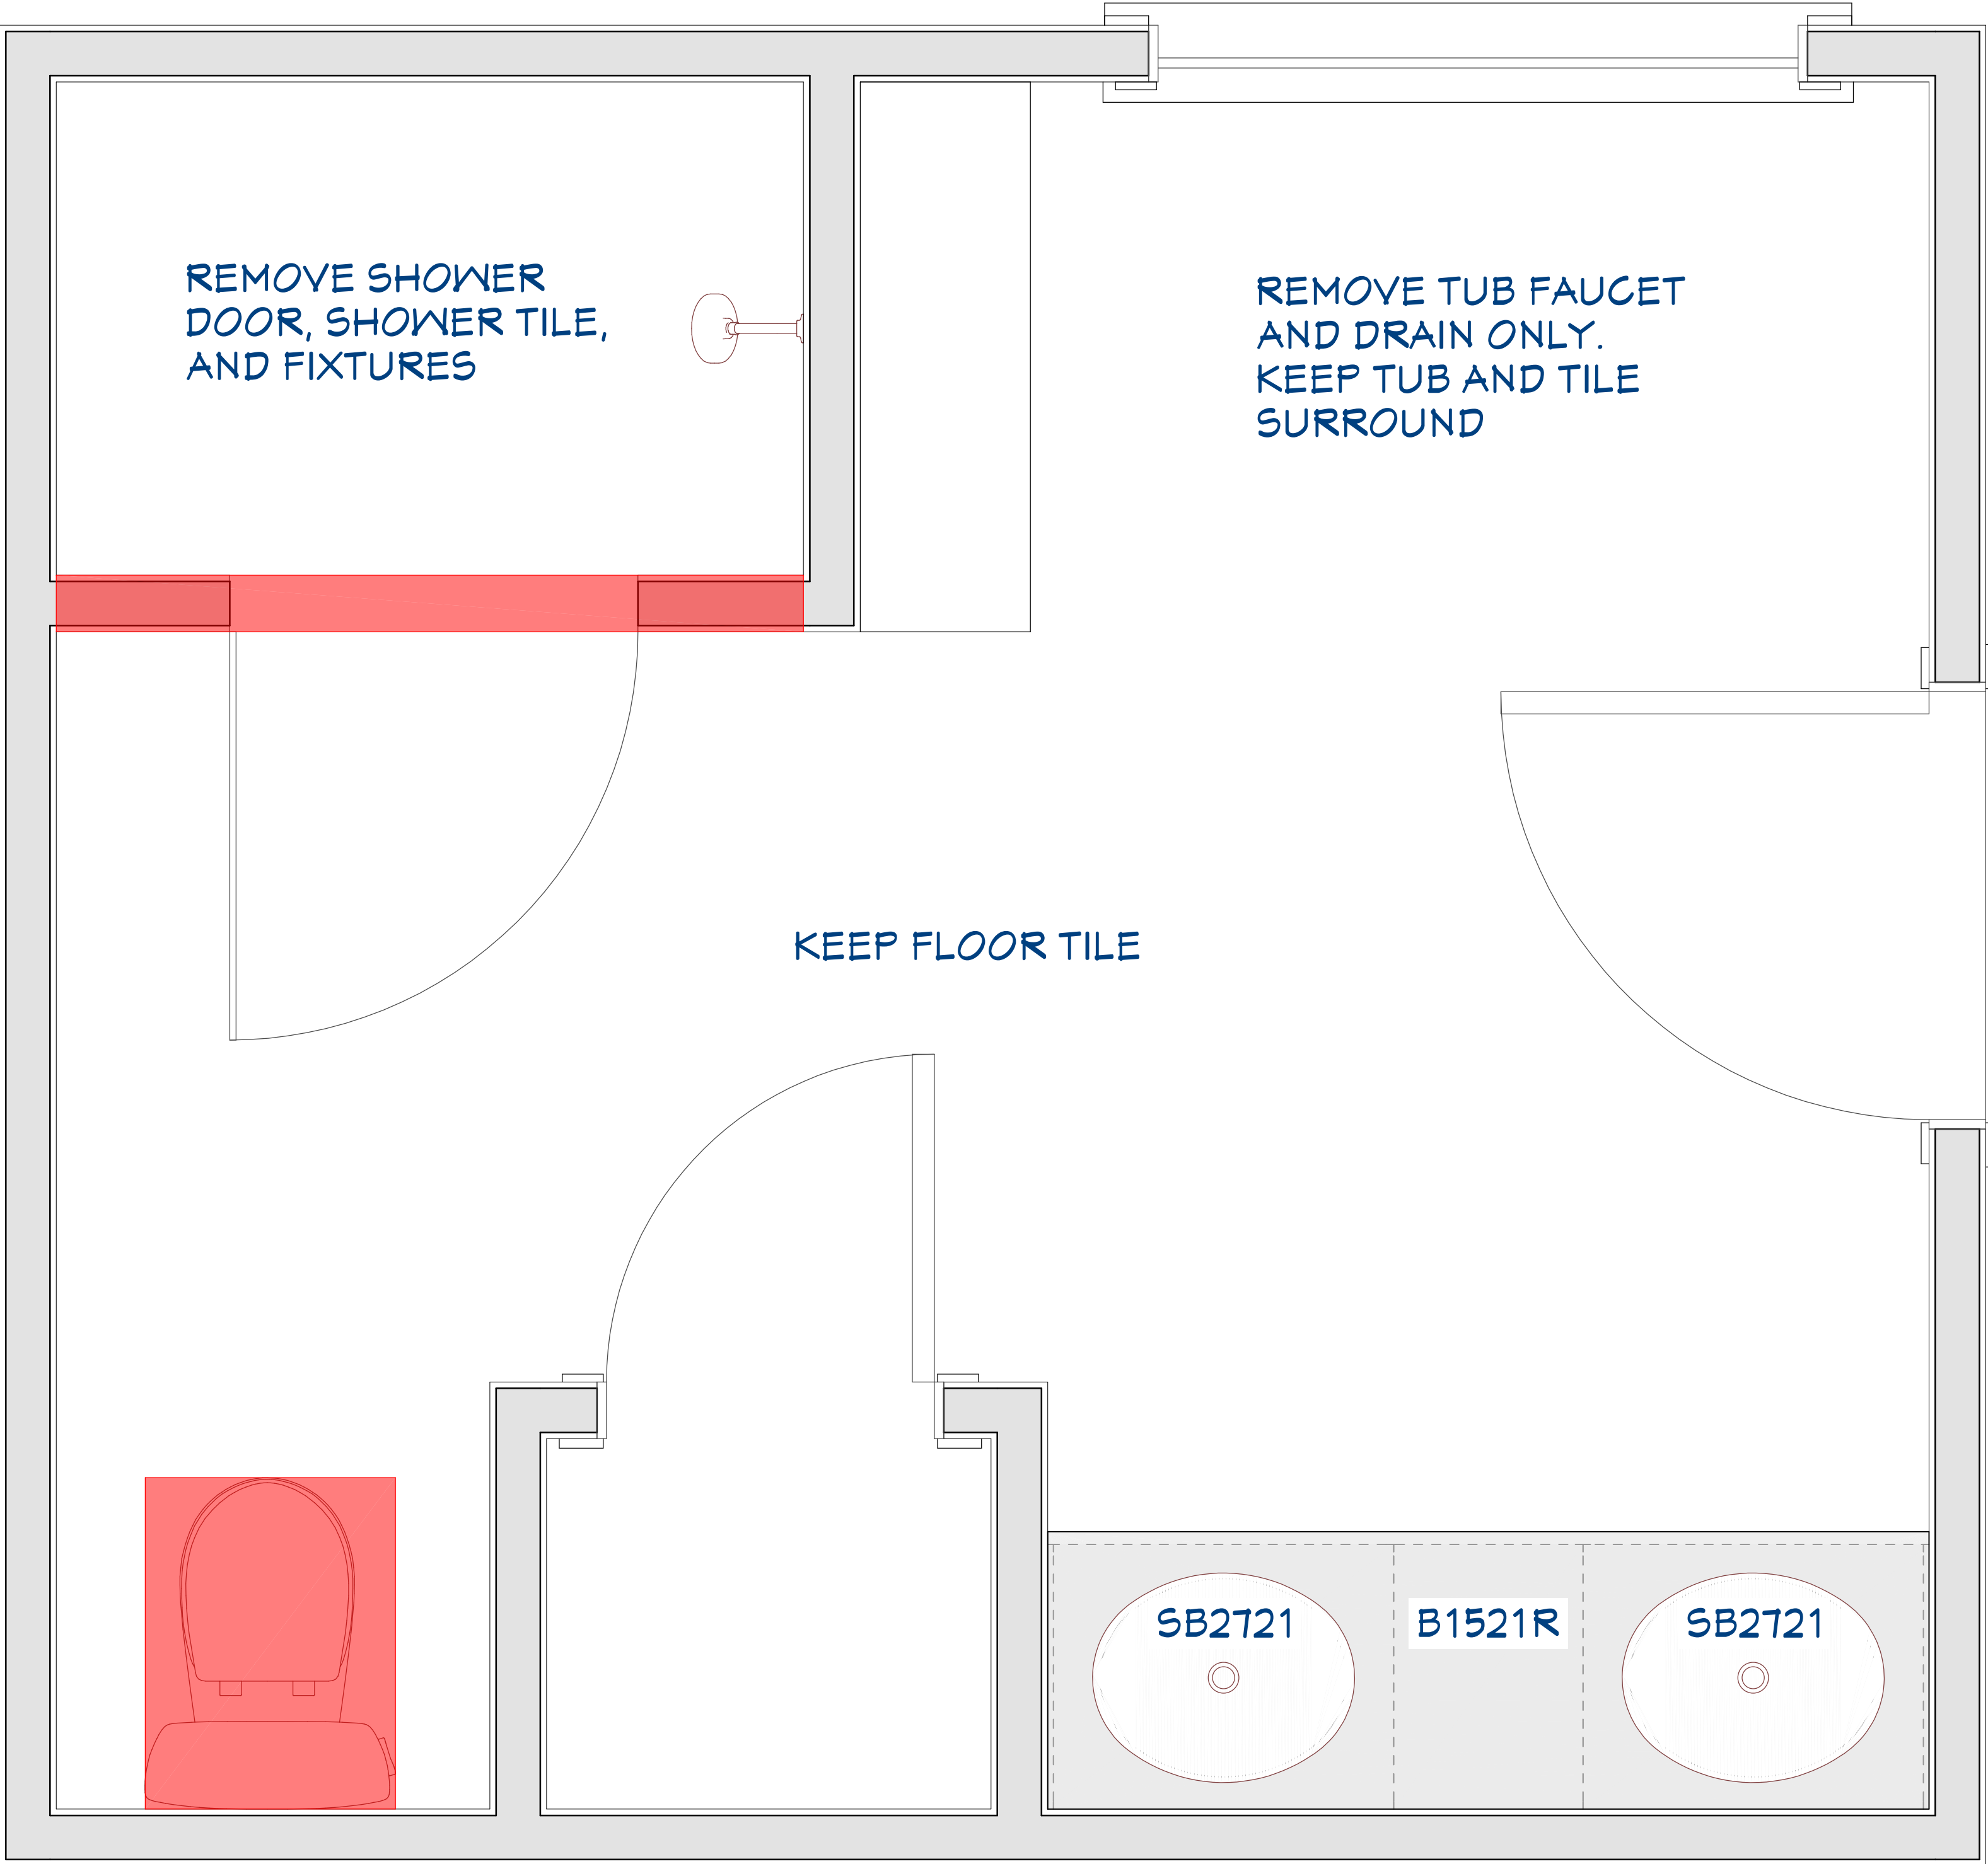

REMOVE TOILET
AND REPLACE
WITH NEW IN SAME
LOCATION

REMOVE VANITY TOP, SINKS,
FAUCETS, MIRROR, AND LIGHTS.
KEEP VANITY CABINETS

REMOVE SHOWER
DOOR, SHOWER TILE,
AND FIXTURES

REMOVE TUB FAUCET
AND DRAIN ONLY.
KEEP TUB AND TILE
SURROUND

KEEP FLOOR TILE



1035 WIL ROSE LN.
VERSAILLES, KY 40383

CARVER/JULIAN
RESIDENCE


DEMO
PLAN

DATE

JUNE 4,
2026

SHEET #

A02

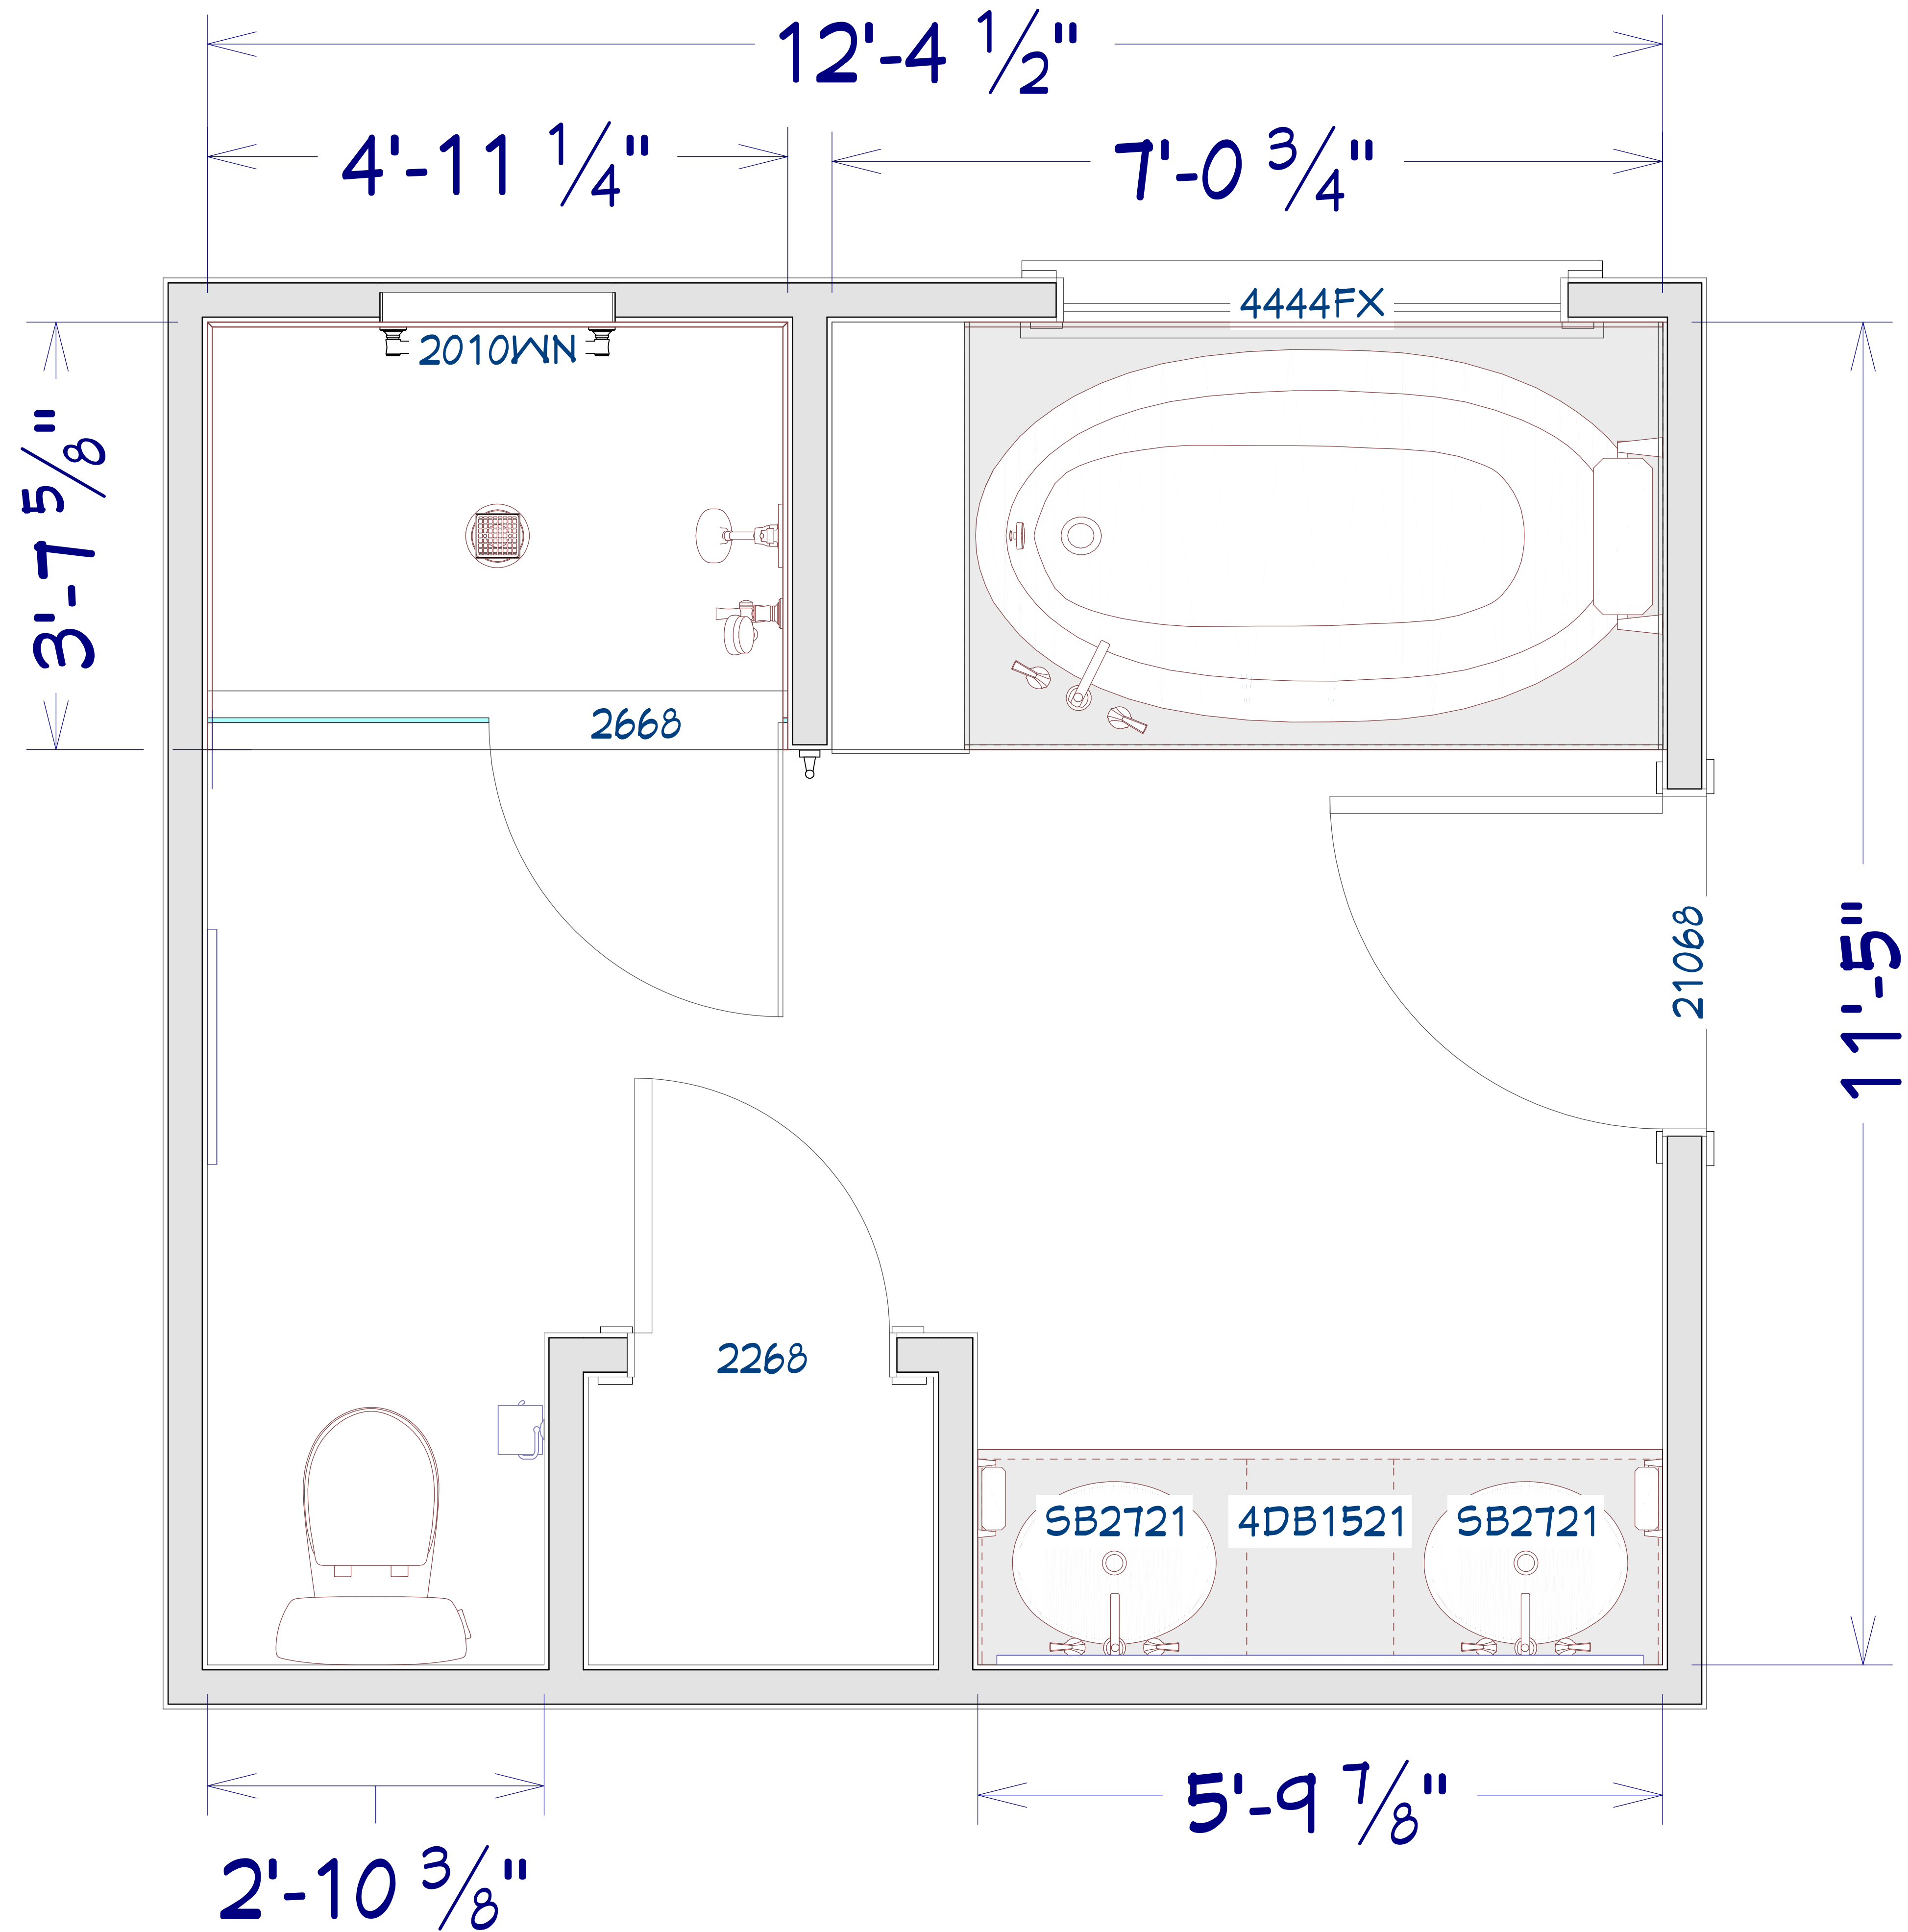

	
1035 WIL ROSE LN. VERSAILLES, KY 40383	
CARVER/JULIAN RESIDENCE	
PROPOSED FLOOR PLAN	
DATE	JUNE 4, 2026
SHEET #	A03

INSTALL 24" GRAB BAR 36" FROM FLOOR

ADD BLOCKING FOR GRAB BAR

ADD HEADER FOR 24" WIDE NICHE

ADD BLOCKING
FOR HANDHELD ON
VERTICAL GRAB
BAR

CONFIRM ALL
LOCATIONS &
HEIGHTS WITH
CLIENT

ADD BLOCKING
FOR FUTURE
FOLDING TEAK
BENCH


INSTALL NEW 24" TOWEL
BAR 60" FROM FLOOR
CENTERED ON TUB

ADD BLOCKING
FOR SHOWER
DOOR HINGES

INSTALL NEW
ROBE HOOK
66" FROM
FLOOR

INSTALL TP
HOLDER 26"
FROM FLOOR

INSTALL NEW 8" TOWEL
BAR 20" FROM VANITY TOP

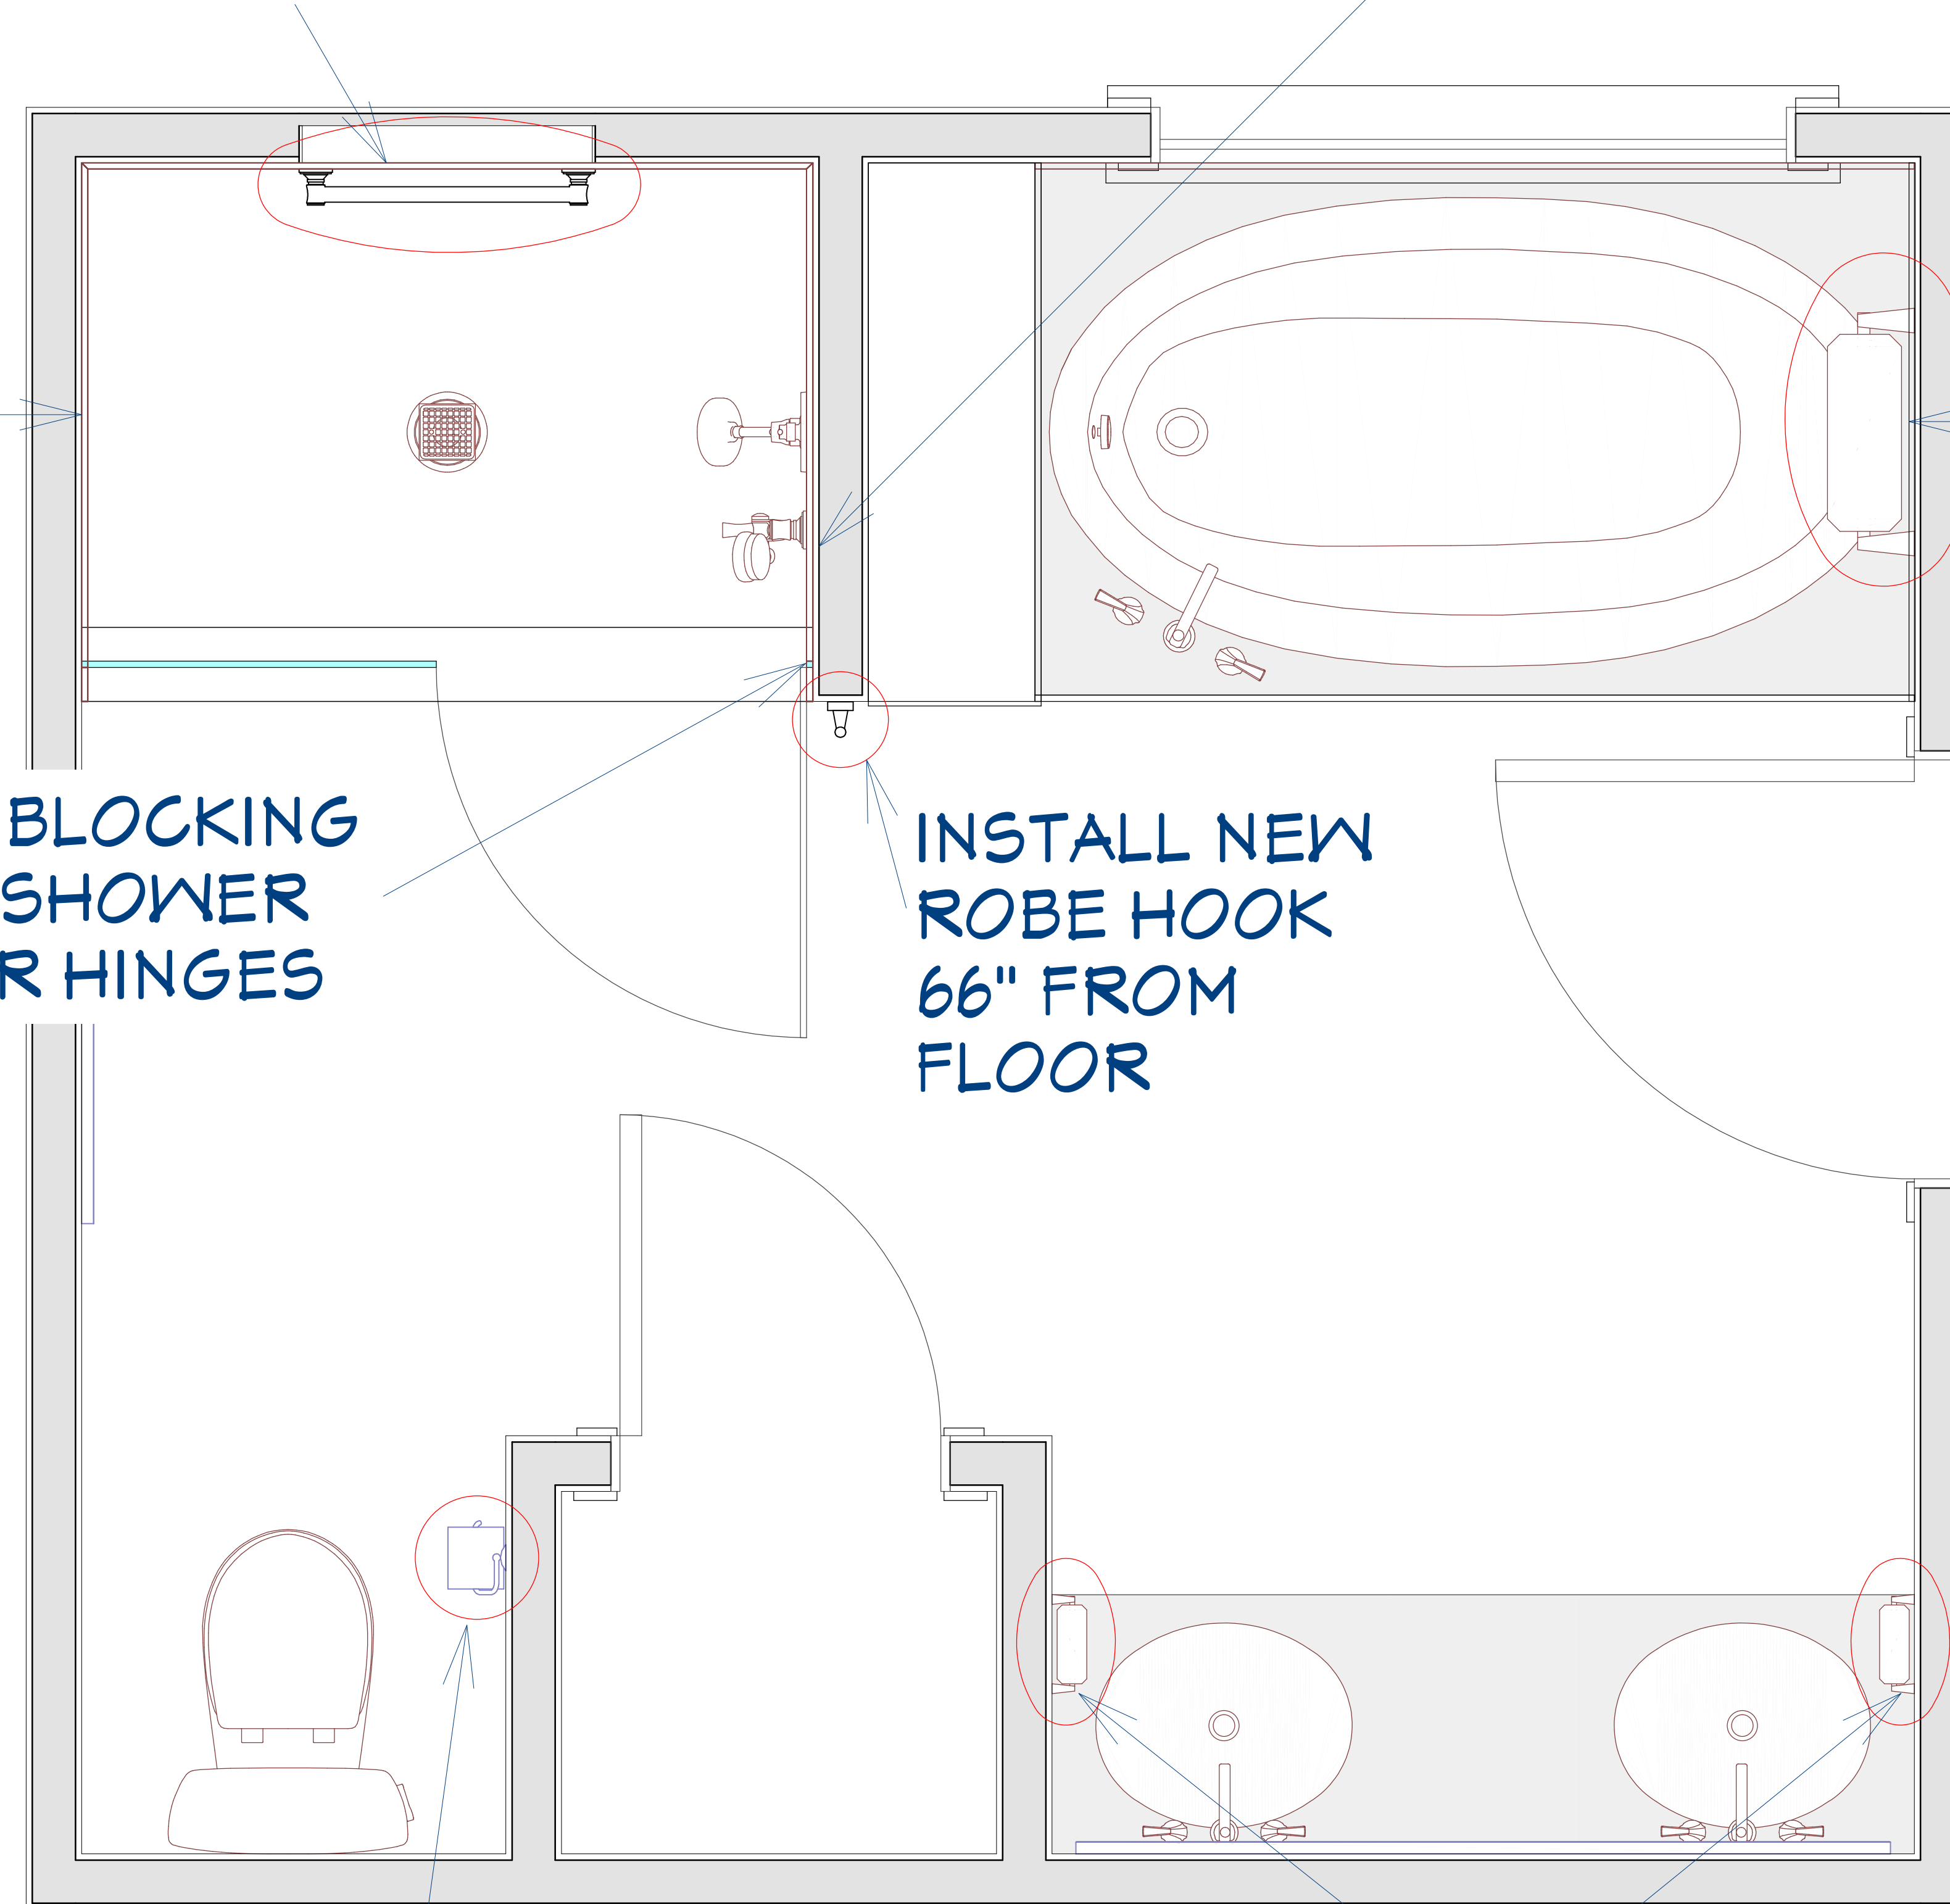

SHEET #

A04

DATE

JUNE 4,
2026


FRAMING/
ACCESSORY
PLACEMENT

1035 WIL ROSE LN.
VERSAILLES, KY 40383


CARVER/JULIAN
RESIDENCE

J & R Construction
DESIGN - BUILD - REMODEL

CONFIRM ALL LOCATIONS & HEIGHTS WITH CLIENT

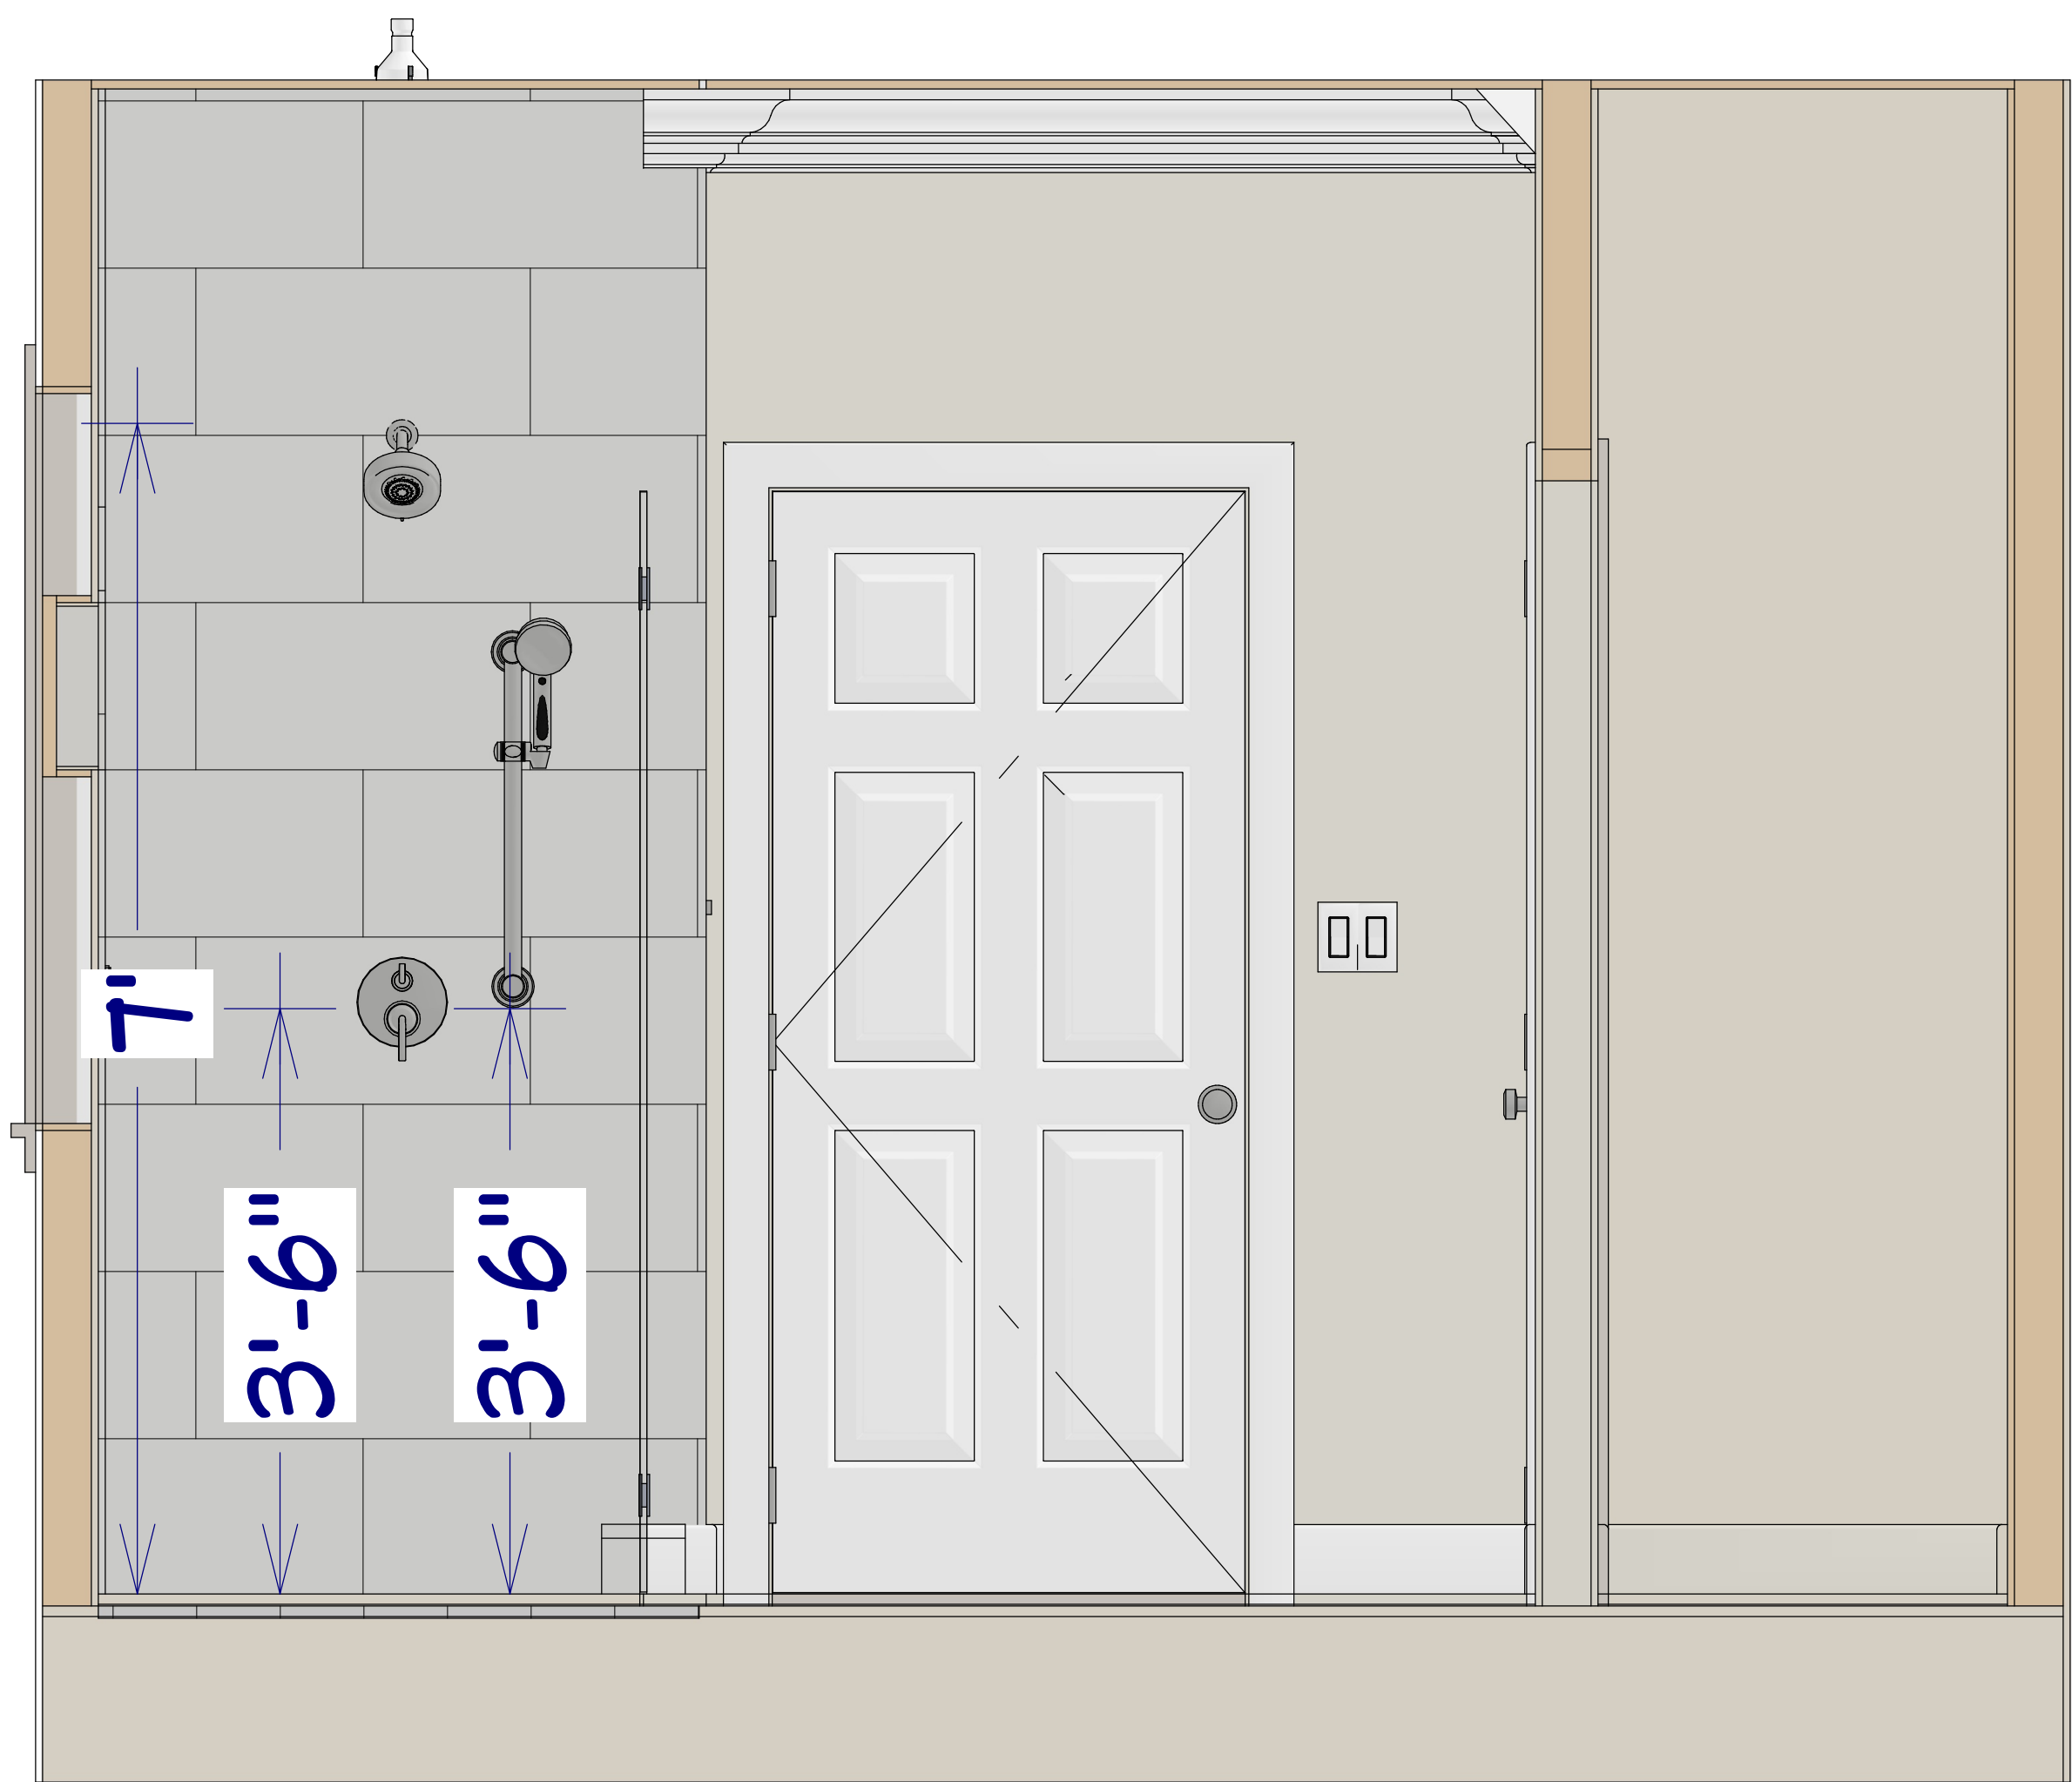



NICHE IS TO BE ADJUSTED
AS NEEDED TO BE INLINE
WITH TILE ROW

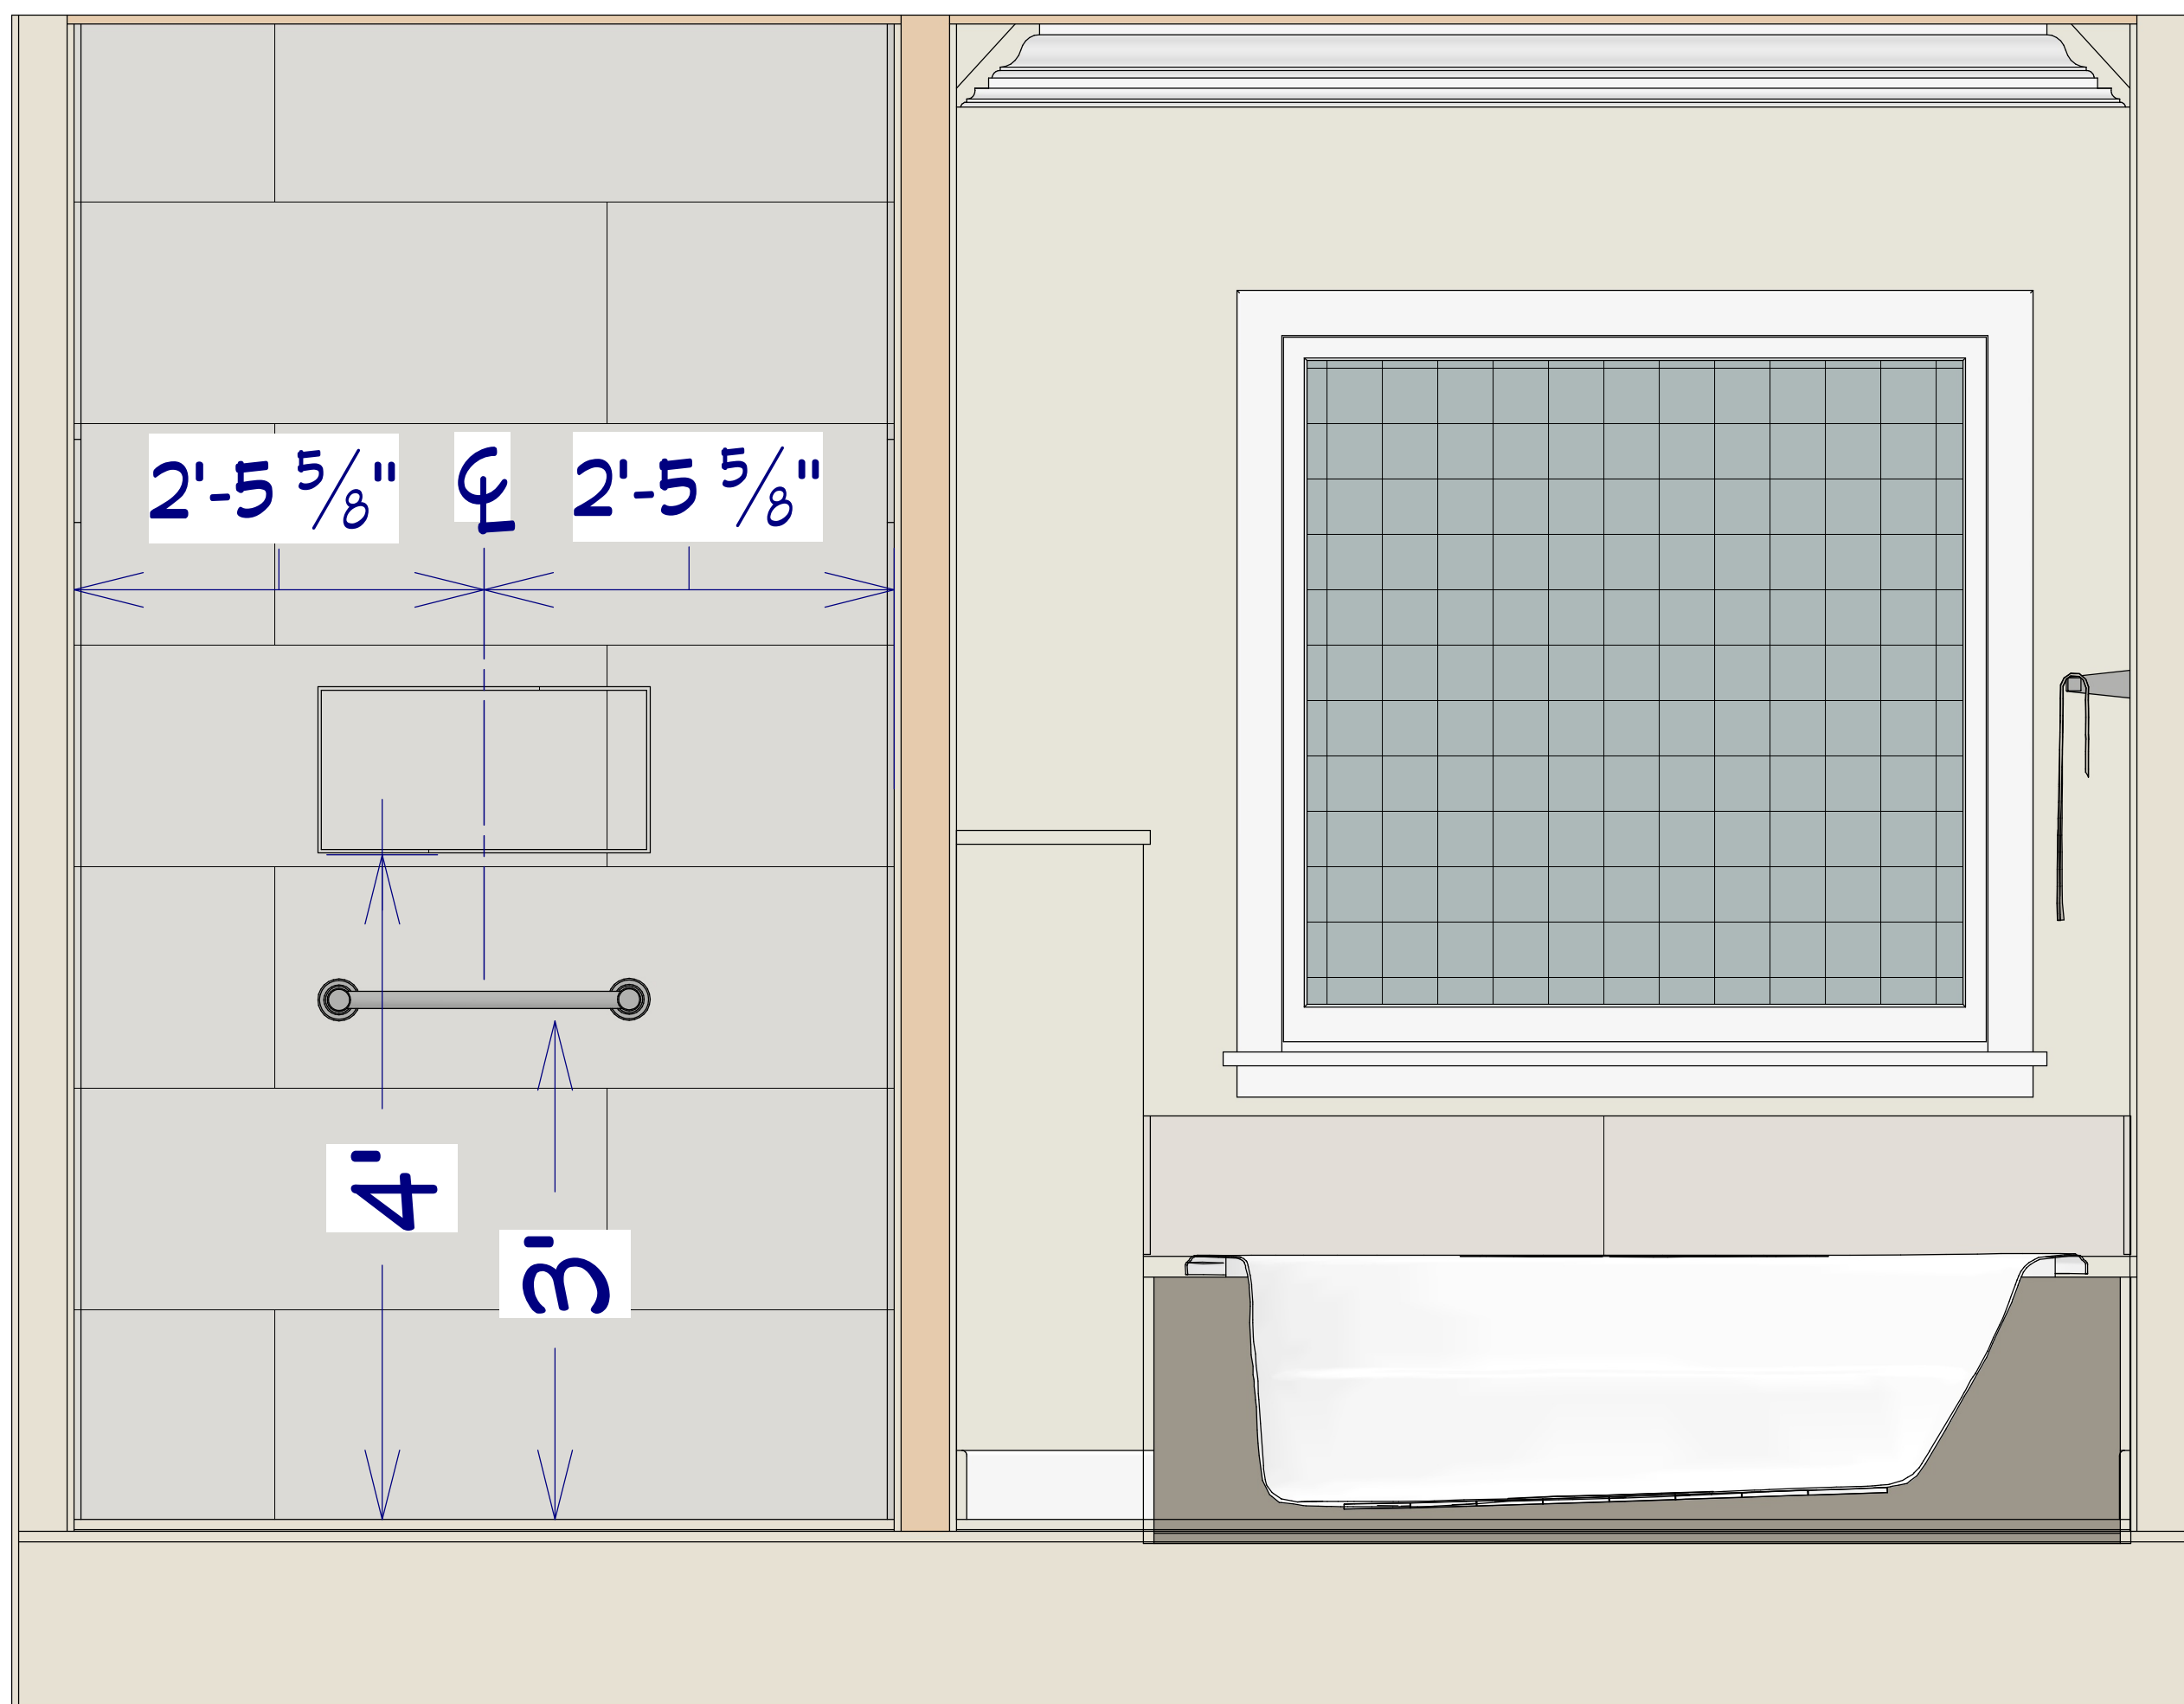

CONFIRM ALL LOCATIONS & HEIGHTS WITH CLIENT

SHEET #	A06
DATE	JUNE 4, 2026
ELECTRIC PLAN	
1035 WIL ROSE LN. VERSAILLES, KY 40383	CARVER/JULIAN RESIDENCE

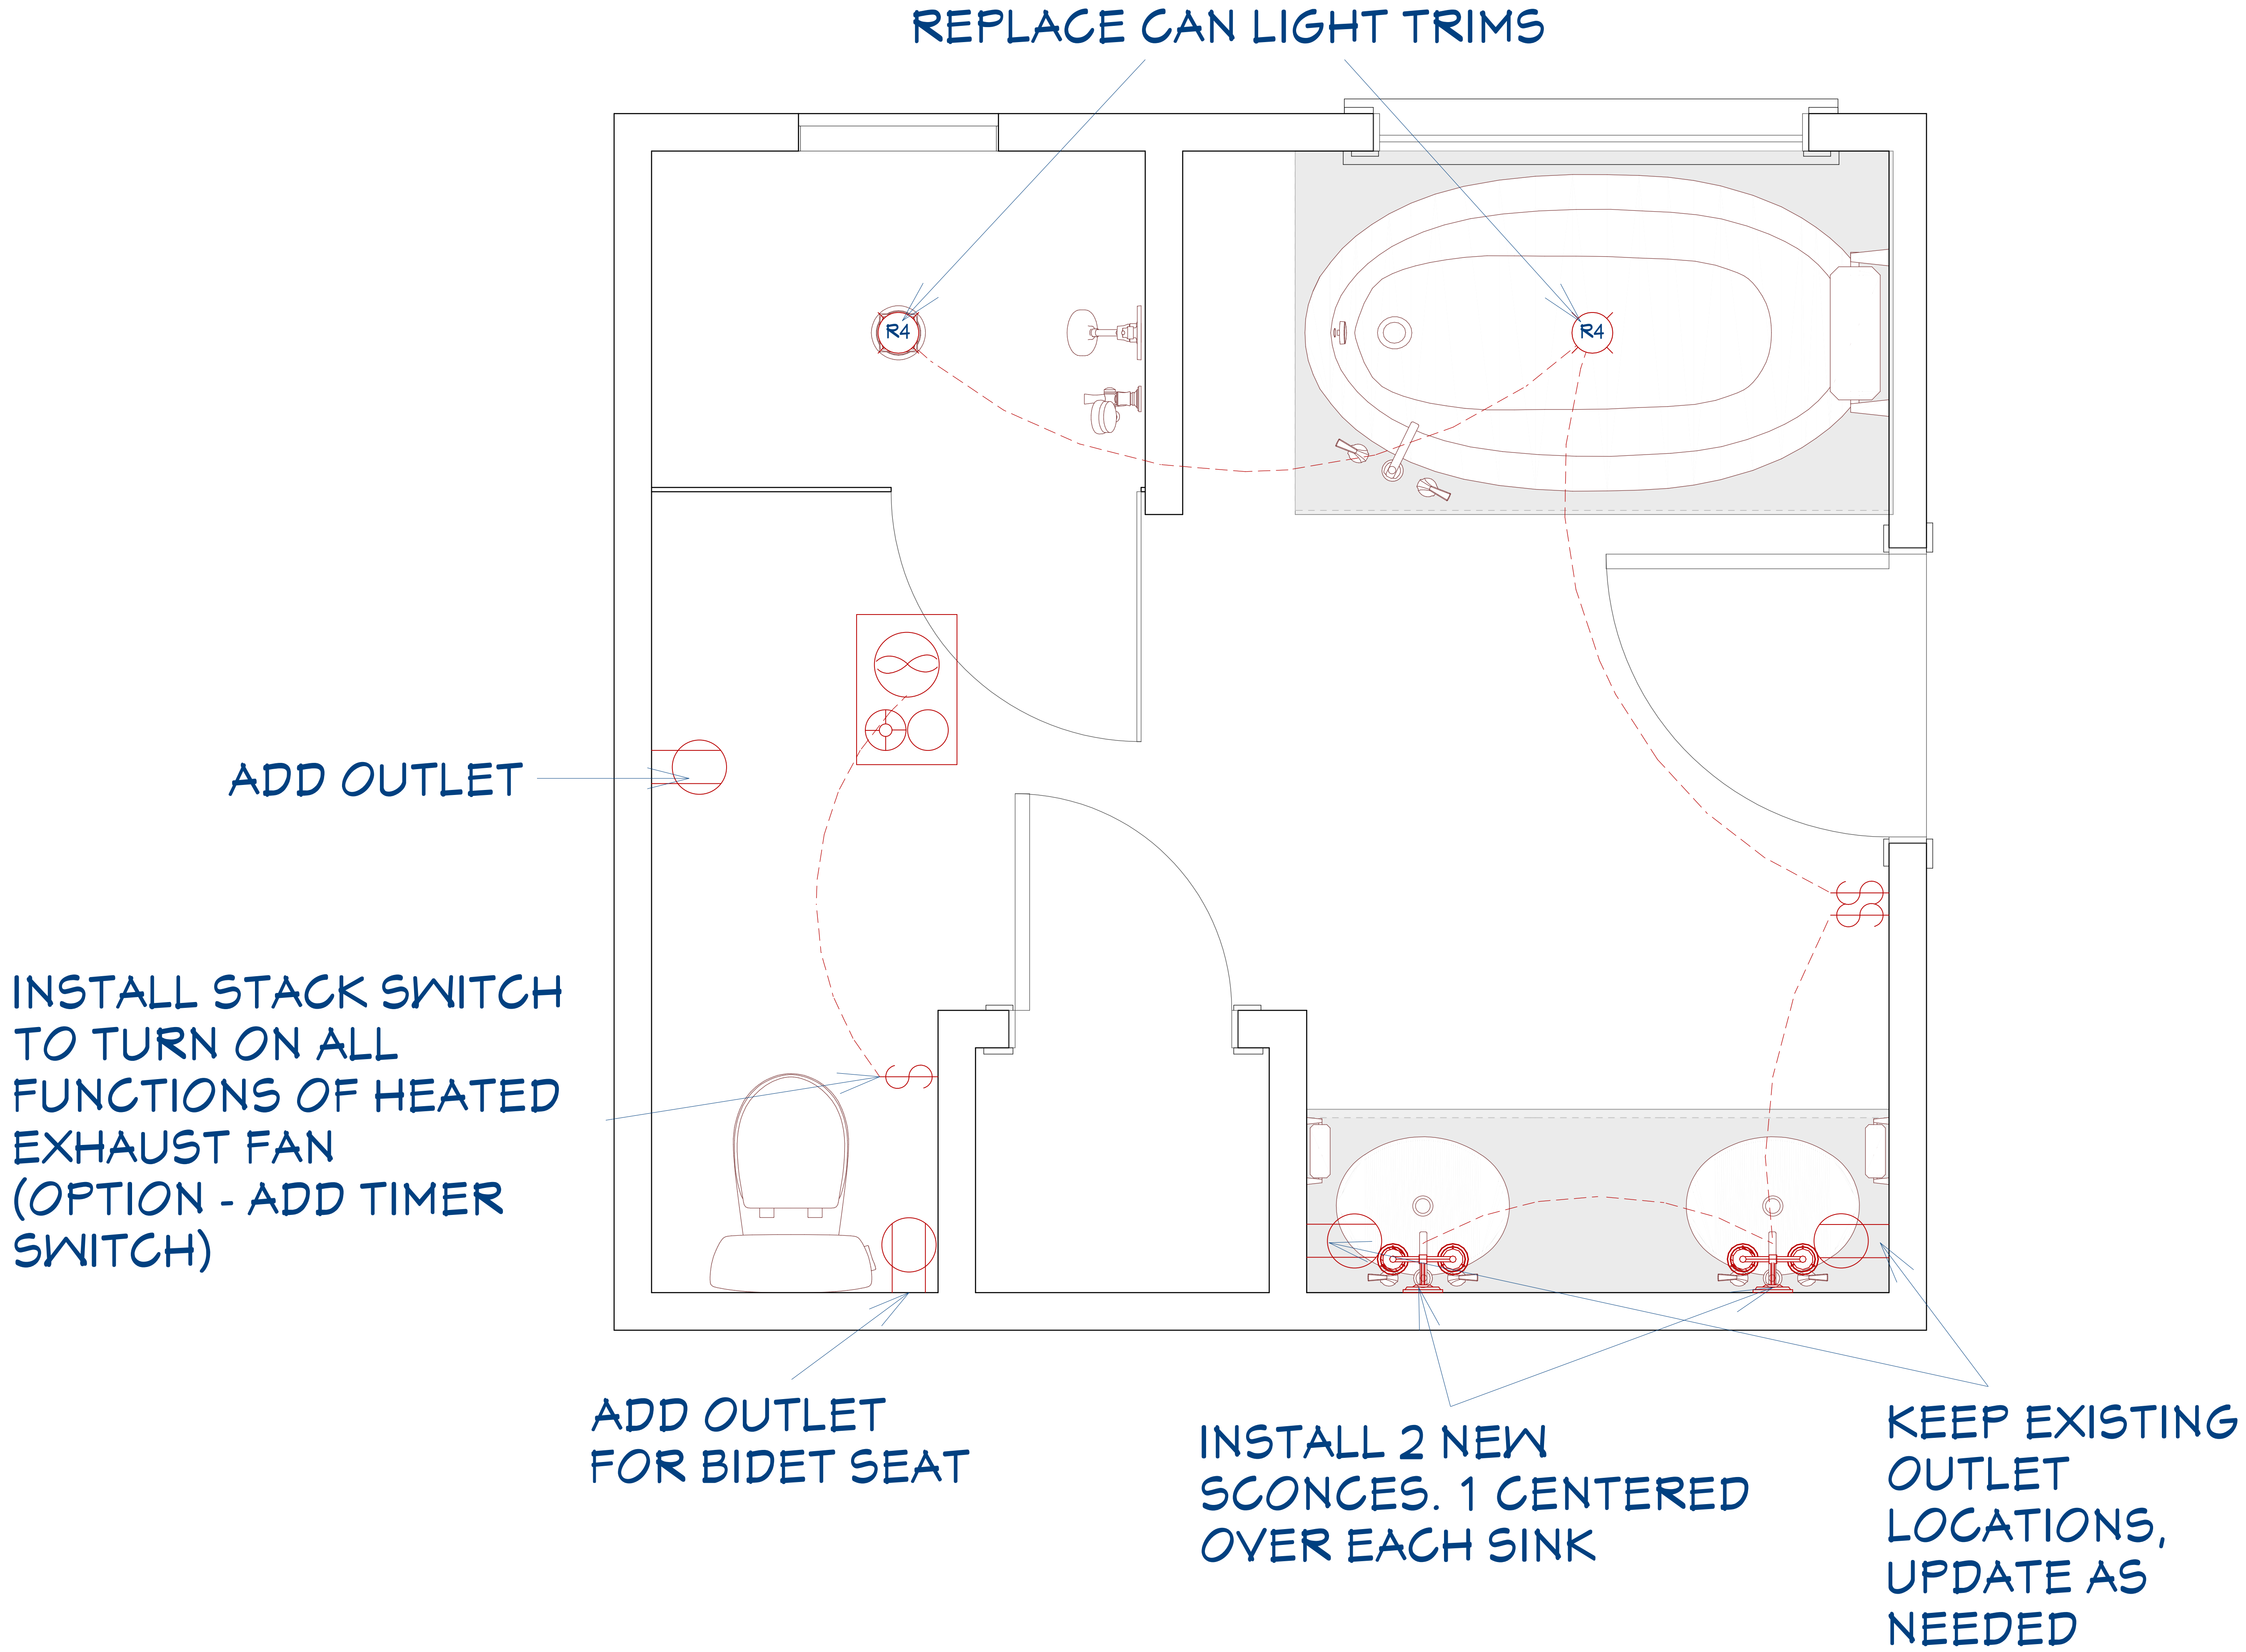

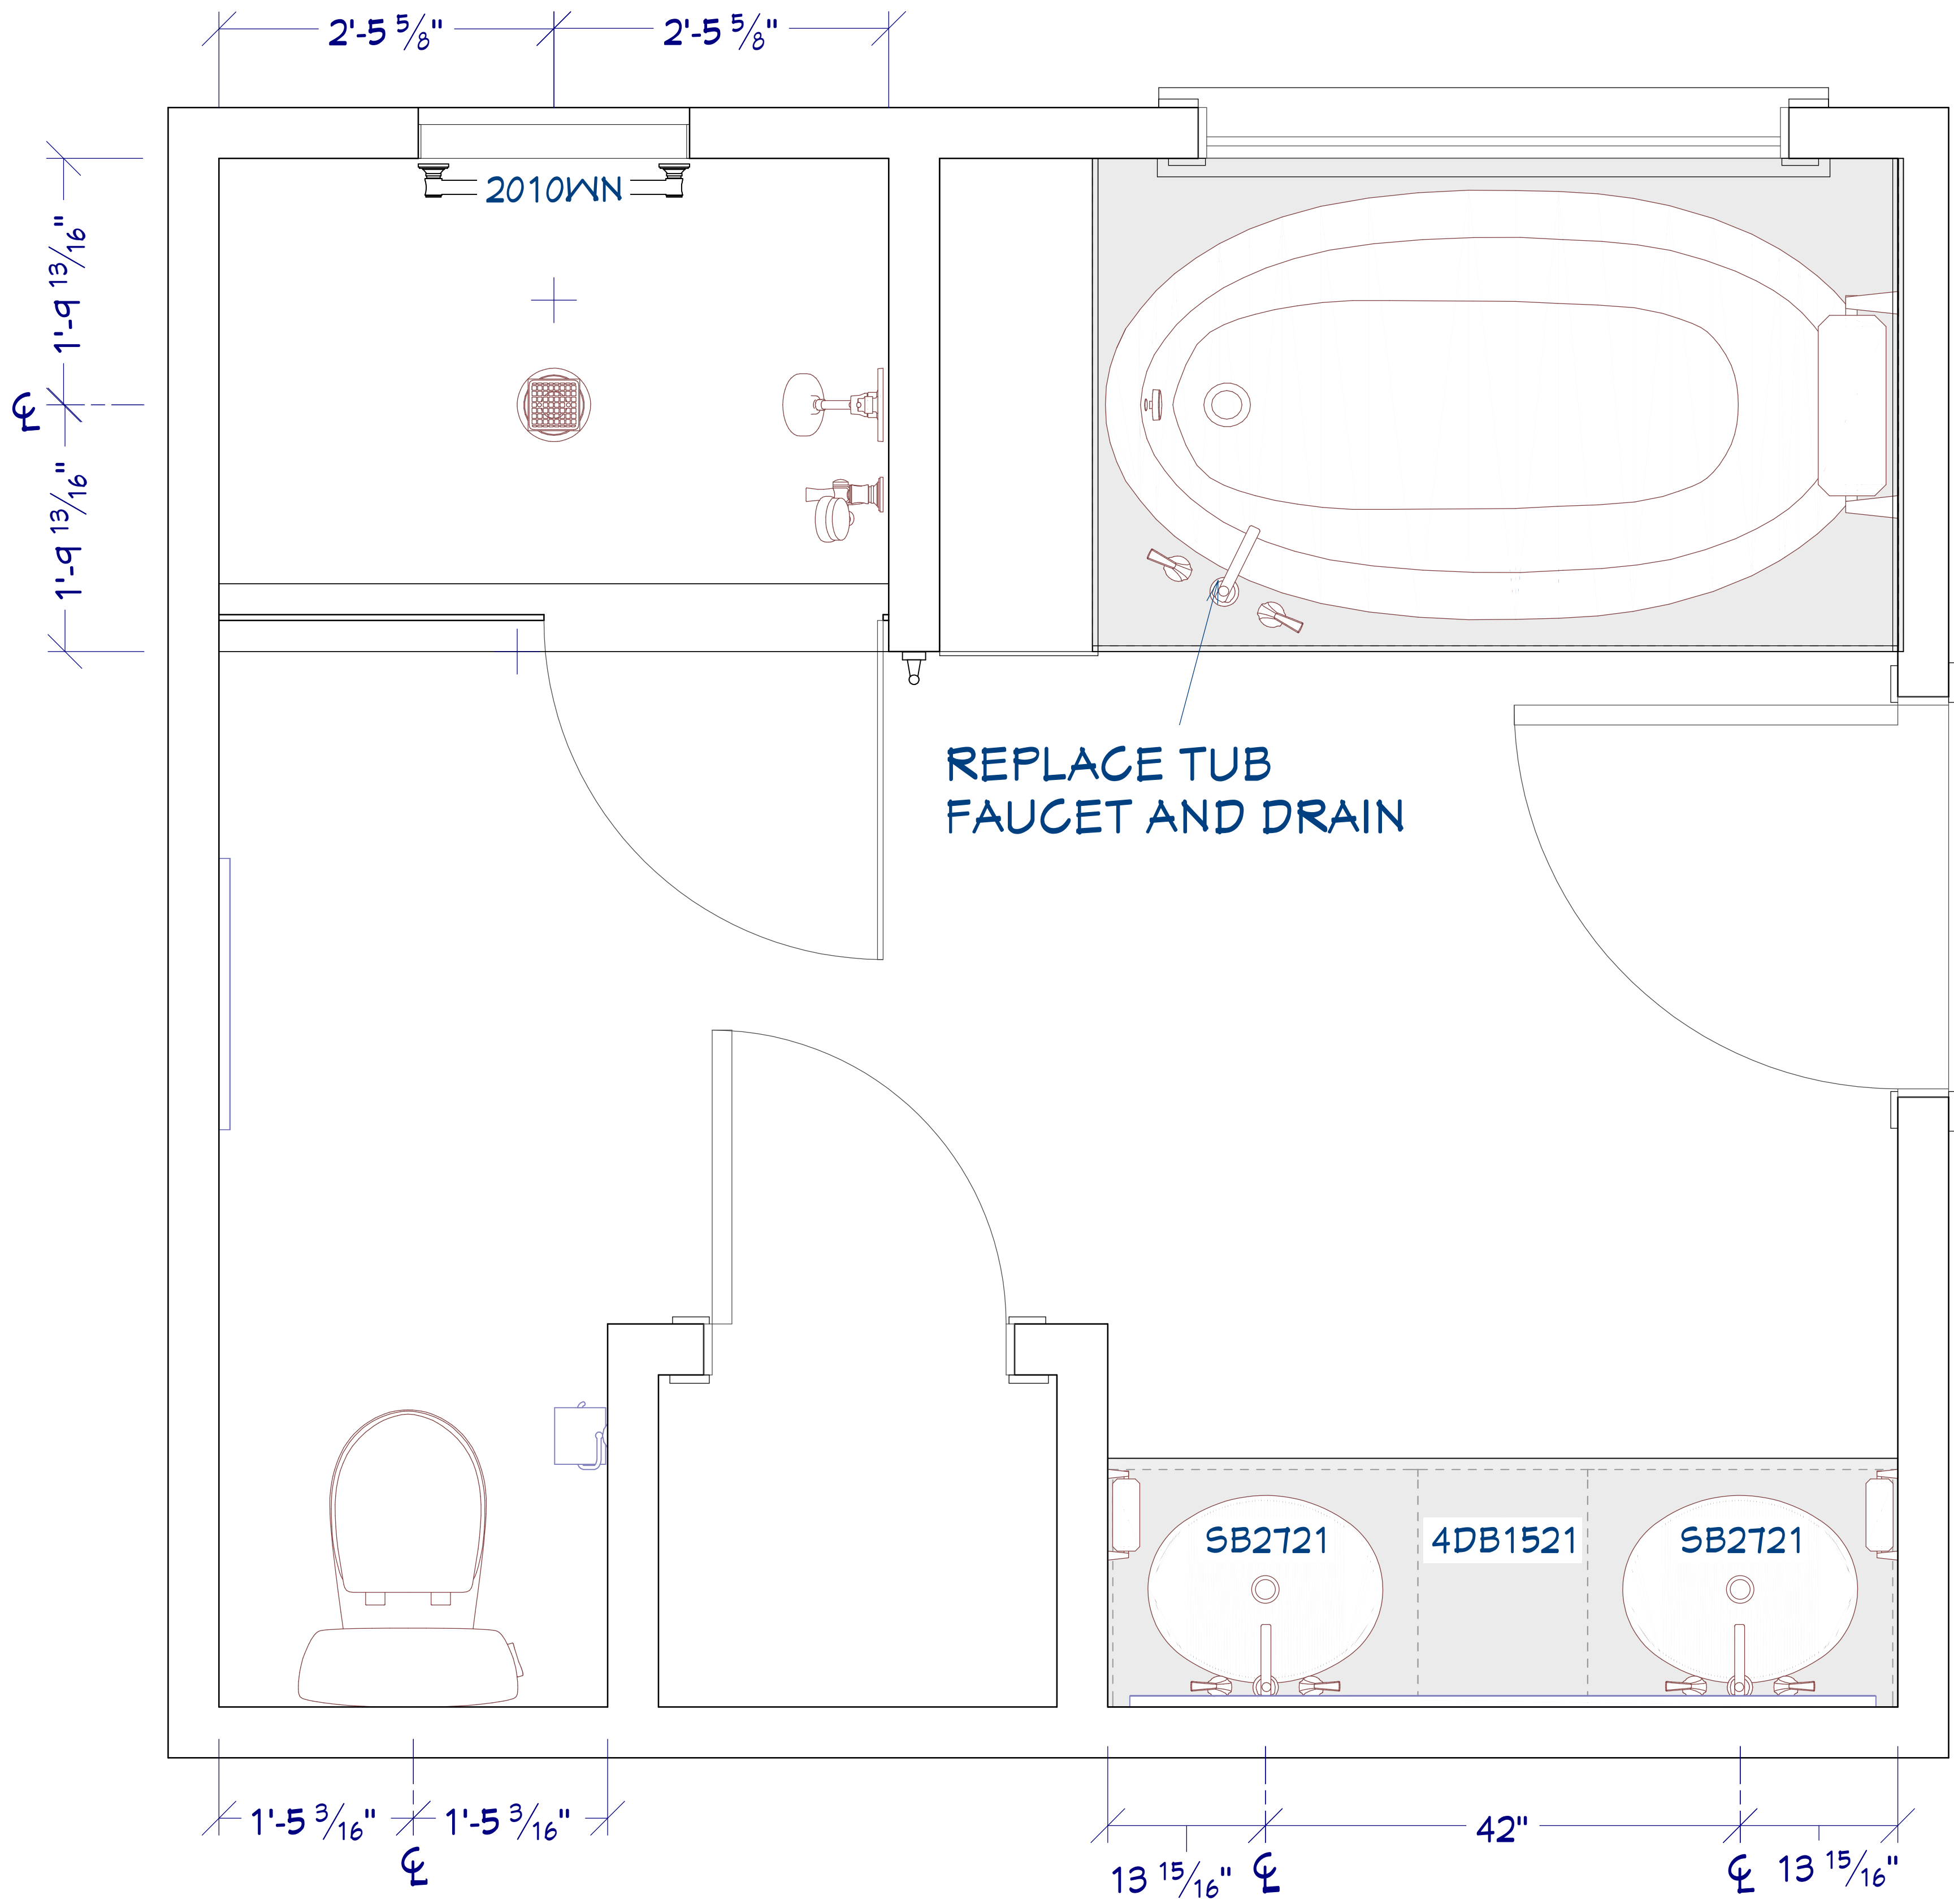

SHEET #		A07	
DATE		JUNE 4, 2026	
PLUMBING PLAN			
1035 WIL ROSE LN. VERSAILLES, KY 40383		CARVER/JULIAN RESIDENCE	
 J&R Construction DESIGN · BUILD · REMODEL			

